201427.CHARALAMBOUS

752 HIGH ST, THORNBURY

SCOPE OF WORKS:

DEMOLITION
- DEMOLITION OF EXISTING HOUSE + ASSOCIATED EXTERNAL WORKS BY OWNER UNDER SEPERATE COVER

STRUCTURAL CONCRETE
- LEVEL BA, GR + 01 SLAB/LEVEL (REFER ENGINEERING)
- LEVEL BA + GR STRUCTURE (REFER ENGINEERING)
- ALL WORKS BY BUILDER

STRUCTURAL TIMBER
- ALL WORK STRUCTURAL CLT TIMBER WORKS TO BE PRE-FABRICATED BY XLAM
- ALL STRUCTURAL STUD WALLS, LEVELS 01-04 TO BE PRE-FABRICATED BY XLAM

BRICK CLADDING
- PGH BRICK TILE CLADDING SYSTEM
(REFER WALL AND FLOOR TYPE BUILDUPS FOR DETAIL)

REMAINING BUILDING WORKS
- ALL REMAINING WORKS BY BUILDER

EXTERNAL WORKS
- ALL HARD LANDSCAPE WORKS INCLUDING ROOF TERRACE TO BE CONSTRUCTED BY BUILDER
- PLANTING BY OTHERS
- PEBBLE ROOF WORKS (REFER PROVISIONAL SUM)

PROTOTYPE
- PROTOTYPE OF TYPCIAL WALL BUILD-UP IS SCHEDULED FOR TO BE CONSTRUCTED IN XLAM WORKSHOP IN CONJUNCTION WITH SELECTED BRICK CLADDING

PROJECT STAGING:
- N/A

TITLE INFORMATION

LOT 1 (NORTH) CROWN PORTION 137 (PT)
DERIVED FROM VOL. 3768 FOL. 475
TP 703011P

LOT 2 (SOUTH) CROWN PORTION 137 (PT)
FROM VOL. 4120 FOL. 814
TP 687047A

GENERAL NOTES:
1. DO NOT SCALE FROM DRAWINGS & CHECK ALL DIMENSIONS ON SITE PRIOR TO COMMENCEMENT OF WORKS.
2. DRAWINGS TO BE READ IN CONJUNCTION WITH SPECIFICATION OF WORKS AND ENGINEER'S DETAILS AND COMPUTATIONS.
3. REFER TO SCHEDULES FOR PROVISIONAL SUMS

FURTHER INFORMATION:
1. STRUCTURAL ENGINEERING - REFER TO ENGINEER'S DRAWINGS
BY 4 SITE ENGINEERS
STRUCTURAL: REF 15-148 DWG NOS: S01(F), S02(C), S03-S06(D), S07(E), S08-12(C)
2. CIVIL ENGINEERING - REFER TO ENGINEER'S DRAWINGS
BY 4 SITE ENGINEERS
CIVIL: REF 15-148 DATED - 26/07/18, REV:A
3. SERVICES ENGINEERING - REFER TO ENGINEER'S DRAWINGS
BY BRT CONSULTING
REF: 9323 DATED - 18/14/17 (CONSTRUCTION ISSUE)
4. FIRE ENGINEERING - REFER TO FIRE ENGINEERING BRIEF
BY RED FIRE ENGINEERS
REF: JV17-00036 (DRAFT) DATED - 25/05/17
5. ACOUSTIC ENGINEERING - REFER TO ENGINEER'S REPORT
BY OCTAVE ACOUSTICS
REF: AA027748-01E02, DATED - 04/08/18)
6. ESD - REFER TO ESD REPORT
BY LID CONSULTING
DATED - 24/08/19
7. THERMAL PERFORMANCE ASSESSMENT - REFER TO REPORT
BY GRAHAM ENERGY
REF: GE1771 DATED - AUGUST 2017 (PRELIMINARY)
8. REFER A.001 FOR LAND SURVEYOR'S DRAWING FOR AHD LEVELS AND EXACT BOUNDARY & FENCE LOCATIONS
9. CLT STRUCTURAL ENGINEERING
BY VISTEK
REF: TBC
10. GEOTECH REPORT
BY GEOAUST GEOTECHNICAL ENGINEERS
REF: 5227-3-R (REVISION 1), DATED: 30 OCTOBER 2019

BCA COMPLIANCE:

READ IN CONJUNCTION WITH BUILDING SURVEYOR REPORT
BY DU CHATEAU CHUN
EARLY WORKS AND FULL PERMIT
(REF ..... DATED - .....)

1. **INSULATION**
GENERALLY NEW WORKS IN EXCESS OF BCA REQUIREMENTS
- REFER TO A.106 + 107 FOR WALL TYPE SCHEDULE

2. **VENTILATION**
PASSIVE VENTILATION:
GENERALLY OPENABLE SASHES TO ALL HABITABLE ROOMS GREATER THAN 5% OF THE FLOOR AREA OF THE ROOM REQUIRED TO BE VENTILATED.

ACTIVE VENTILATION:
WINDOW TRICKLE VENTS + EXHAUST FANS FOR MECHANICAL AIR EXCHANGE
REFER SERVICES PLANS, RCPS + WINDOW AND DOOR SCHEDULE

3. **NATURAL LIGHT**
GENERALLY ALL ROOMS TO HAVE NATURAL LIGHT AREA GREATER THAN 10% OF FLOOR AREA OF THE ROOM

4. **GLAZING GENERALLY**
GENERALLY IN ACCORDANCE WITH AS.1288 - 2006 SPECIFICALLY
- GLAZING WITHIN 500MM OF FFL TO BE SAFETY GLASS
- GLAZING TO DOORS & SIDE PANELS TO BE SAFETY GLASS
- GLAZING WITHIN 1.5M OF A BATH OR 500MM OF A SHOWER TO BE SAFETY GLASS

GENERALLY NEW WINDOWS & GLAZED DOORS TO BE DOUBLE GLAZED U.O.N.
SEE WINDOW + DOOR SCHEDULE FOR NOTES + SPEC A.501

5. **WATERPROOFING WET AREAS**
WET AREAS SHALL GENERALLY BE WATERPROOFED IN ACCORDANCE WITH AS.3740 - 2004
- SHOWERS WATERPROOFED TO 2100mm HIGH INCLUDING BASE IF APPROPRIATE
- FLOOR SURFACE TO BATHROOMS & TOILETS TO BE WATERPROOFED FULLY
- WALLS BEHIND BASINS, TROUGHS & SINKS TO BE WATERPROOFED TO MIN. 150mm HIGH ABOVE FIXTURE
- WALLS AROUND BATHS TO BE WATERPROOFED TO MIN. 600mm ABOVE BATH EDGE

6. **ENERGY RATING**
COMPLIANCE WITH NatHERS THERMAL PERFORMANCE ASSESSMENT
ENERGY RATING AS PER ATTACHED ASSESSMENT
BY GRAHAM ENERGY REF: GE1771 DATED - AUGUST 2017 (PRELIMINARY)

STANDARD INCLUSIONS FOR ENERGY RATING
BUILDER TO ENSURE THAT:
- ALL GAPS + CRACKS TO WINDOW/DOOR FRAMES ARE SEALED ON CONSTRUCTION
- SEALATION (AS PER ABOVE INSULATION NOTES) IS APPLIED TO ALL WALLS, + GAPS/JOINS SEALED
- EXHAUST FANS ARE OF CLOSABLE TYPE
- DRAUGHT EXCLUDERS ARE FITTED TO ALL EXTERNAL HINGED DOORS
- ALL EXTERNAL DOORS ARE WEATHER-STRIPPED

7. **TERMITES**
TERMITE PROTECTION GENERALLY IN ACCORDANCE WITH AS3660.1-2000

- DAREBIN CITY COUNCIL ADVISES THAT THE SITE NOT CATEGORIZED

FIRE PROTECTION

CLT STRUCTURE	- ENCASED IN FIRE PROTECTIVE PLASTERBOARD TO ACHIEVE FRL OF 90/90/90 - REFER A.106 + A.107 FOR WALL AND FLOOR BUILDUPS - REFER A.701 FOR FIRE RATING SCHEDULE
STEEL STRUCTURE (INTERNAL)	- ENCASED IN FIRE PROTECTIVE PLASTERBOARD AS PER CLT STRUCTURE
STEEL STRUCTURE (EXTERNAL C3 COLUMNS)	- INTUMESCANT PAINT TO ACHIEVE FRL OF 90/-/-

DRAWING LIST:

DWG NO	DRAWING NAME	RevNo	DWG SCALE
A.001	COVER SHEET + SITE CONTEXT	F	AS SHOWN
A.101	SITE PLAN - EXISTING & DEMOLITION	D	1:200@A1
A.102	FLOOR PLAN - BASEMENT/GROUND	D	1:100@A1
A.103	FLOOR PLAN - LEVEL 01 + 02	F	1:100@A1
A.104	FLOOR PLAN - LEVEL 03 + 04	E	1:100@A1
A.105	ROOF PLAN - LEVEL 05	E	1:100@A1
A.106	WALL/FLOOR/ROOF TYPE SCHEDULE	E	1:10 @ A1
A.107	WALL/FLOOR/ROOF TYPE SCHEDULE	E	1:10 @ A1
A.108	SITE PLAN - PROPOSED	D	1:200@A1
A.201	RCP - GROUND FLOOR + LEVEL 01	D	1:100@A1
A.202	RCP - LEVEL 02 + LEVEL 03	D	1:100@A1
A.203	RCP - LEVEL 04 + LEVEL 05	D	1:100@A1
A.204	ELECTRICAL PLAN - GROUND FLOOR + LEVEL 01	D	1:100@A1
A.205	ELECTRICAL PLAN - LEVEL 02/LEVEL 03/LEVEL 04	D	1:100@A1
A.206	FINISHES PLAN - BASEMENT + GROUND FLOOR	D	1:100@A1
A.207	FINISHES PLAN - LEVEL 01/LEVEL 02/LEVEL 03	D	1:100@A1
A.301	ELEVATIONS - WEST & NORTH	E	1:100
A.302	ELEVATIONS EAST & SOUTH	F	1:100@A1
A.401	SECTIONS - PROPOSED	F	1:100@A1
A.402	SECTIONS - PROPOSED	F	1:100@A1
A.403	SECTIONS - PROPOSED	F	1:100@A1
A.404	DETAILS - SERVICES RISER + METER CUPBOARDS	D	1:100
A.405	DETAILS - TYPICAL WINDOW DETAILS	D	1:100
A.406	DETAILS - TYPICAL BALCONY + ROOF DETAILS	D	1:100
A.407	DETAILS - AWNINGS (LEVEL GR + 3)	D	AS SHOWN
A.408	DETAILS - LEVEL 05 SHADE STRUCTURE + ROOF	D	AS SHOWN
A.409	DETAILS - GLASS BLOCK WALL	D	AS SHOWN
A.410	DETAILS - STAIRWELL	D	AS SHOWN
A.501	WINDOWS, DOORS & PARTITIONS SCHEDULE	D	1:100@A1
A.502	WINDOWS, DOORS & PARTITIONS SCHEDULE	D	1:100@A1
A.503	WINDOWS, DOORS & PARTITIONS SCHEDULE	D	1:100@A1
A.600	JOINERY SCHEDULE & TYPICAL DETAILS	D	1:100
A.601	JOINERY PLANS & ELEVATIONS - LEVEL GR	D	AS SHOWN
A.602	JOINERY PLANS & ELEVATIONS - FOYER LVL 01-05	D	1:50 @ A1
A.603	JOINERY PLANS & ELEVATIONS - LEVEL 01	D	1:100
A.604	JOINERY PLANS & ELEVATIONS - LEVEL 01 + LEVEL 02	D	1:100
A.605	JOINERY PLANS & ELEVATIONS - LEVEL 02 + LEVEL 03	D	1:100
A.606	JOINERY PLANS & ELEVATIONS - LEVEL 03 + LEVEL 04	D	1:100
A.607	JOINERY PLANS & ELEVATIONS - LEVEL 04	D	1:100
A.608	JOINERY PLANS & ELEVATIONS - LEVEL 05	D	1:50 @ A1
A.609	JOINERY PLANS & ELEVATIONS-TYPICAL WET AREAS	A	1:100
A.610	JOINERY PLANS & ELEVATIONS-TYPICAL WET AREAS	D	1:100
A.701	FIRE RATED PLASTERBOARD (ALL LEVELS)	A	1:100@A1

GENERAL LEGEND:

(A.01) W WINDOW NUMBER
(A.01) D DOOR NUMBER
(E) EXISTING
U.O.N. UNLESS OTHERWISE NOTED
DOOR
WINDOW
SD SLIDING DOOR
CSD CAVITY SLIDING DOOR
SLIDING DOOR + WINDOW

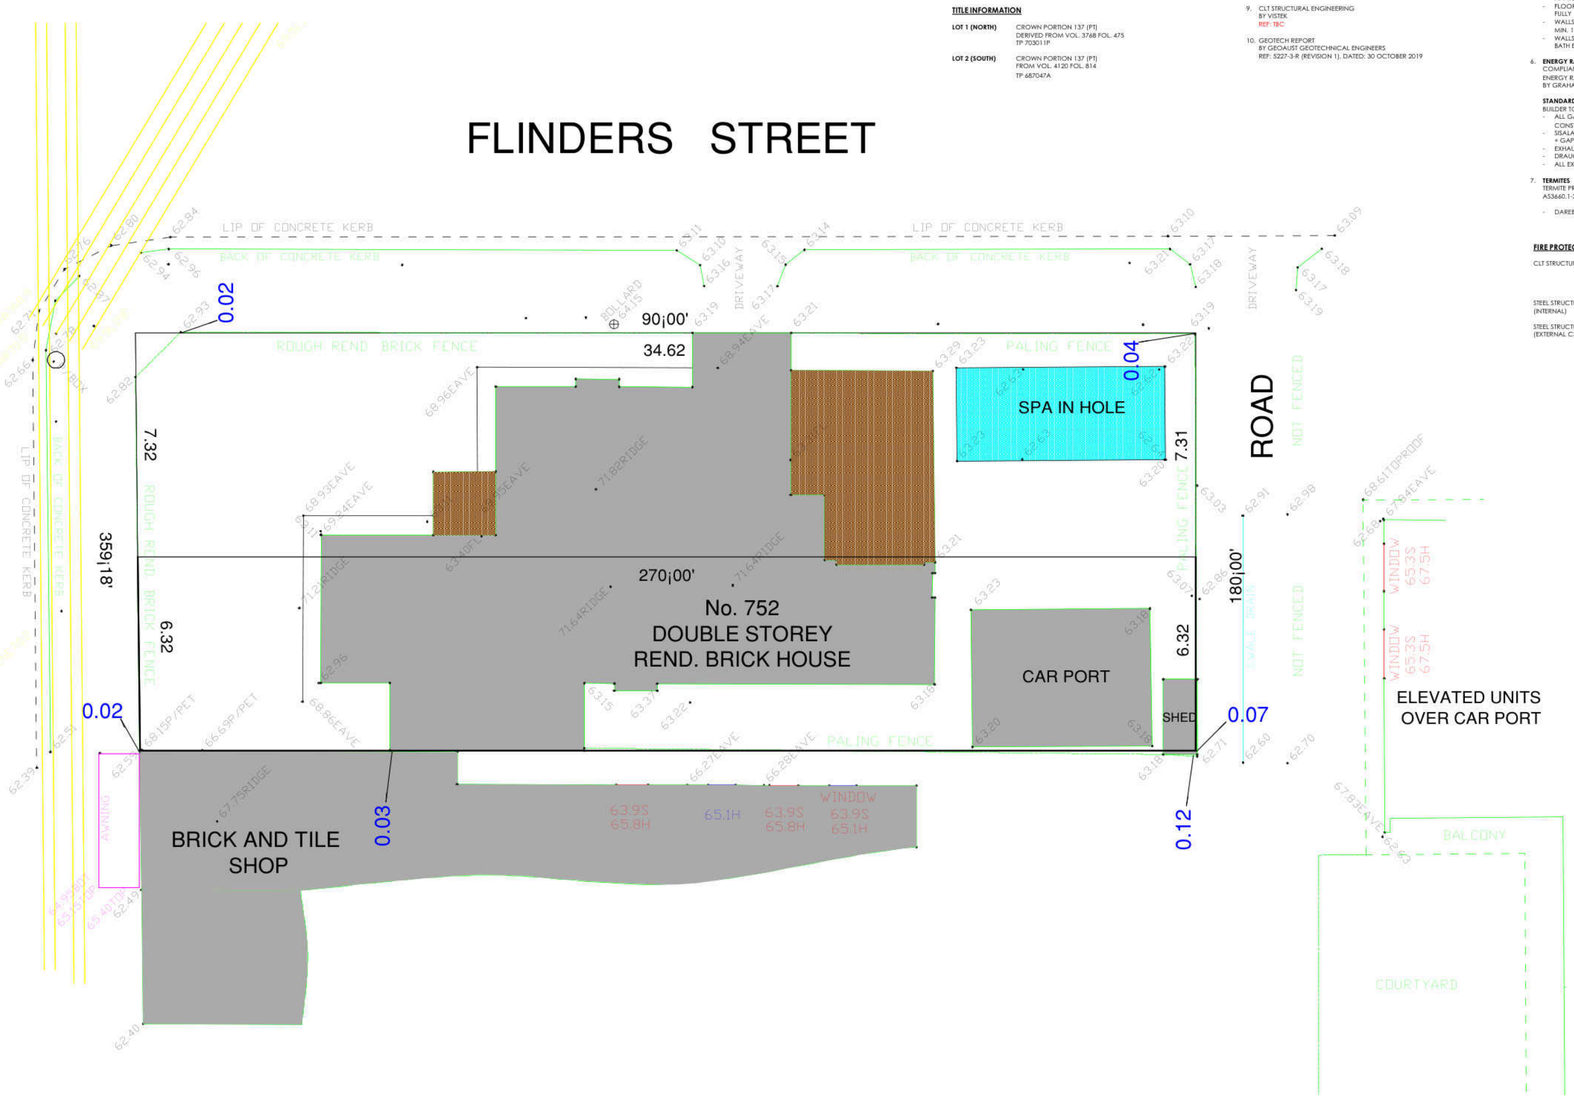

1 SITE SURVEY
Scale: 1:100

2 LOCATION PLAN
N.T.S

FOR CONSTRUCTION - 17/12/19

ISSUE	DATE	REVISION
F	17/12/19	FOR CONSTRUCTION
E	13/11/19	UPDATED DRAWING REFERENCE LIST
D	31/10/19	UPDATED DRAWING REFERENCE LIST
C	31/5/19	CONTRACT SET

CLIENT H.CHARALAMBOUS
Gardiner Architects
7/252 St Georges Rd, Fitzroy North, VIC, 3068
Ph: (03) 9486 4592 E: info@paulgardiner.com.au

DWG COVER SHEET + SITE CONTEXT
PROJECT RETAIL/RESIDENTIAL DEVELOPMENT
752 HIGH STREET, THORNBURY
DRAWN BY AM
SCALE AS SHOWN
JOB NO 141211
A.001
DWG #
REV# F

PHOTO A

PHOTO B

PHOTO C

PHOTO D

DEMOLITION LEGEND:

- EXISTING WALLS
- DEMOLISHED WALLS
- SHADED AREA REMOVED TOTALLY
- EXISTING DOORWAY REMOVED
- EXISTING WINDOW REMOVED

DEMOLITION NOTES:

1. READ IN CONJUNCTION WITH SPECIFICATION
2. DEMOLISH AS NECESSARY TO ACHIEVE THE PROPOSED WORKS CONTRACTOR TO MAKE GOOD AS NECESSARY TO ACHIEVE THE PROPOSED WORKS.
3. EXISTING + ADJOINING STRUCTURE TO BE SECURELY BRACED THROUGHOUT AND AFTER DEMOLITION.
4. DUST IS TO BE KEPT TO A MINIMUM.
5. AREAS WHERE DEMOLITION WORK HAS BEEN UNDERTAKEN ARE TO BE LEFT CLEAN AND CLEAR OF ALL DEBRIS.
6. INSPECTION & REPORT ITEMS:
   BUILDER TO INSPECT & REPORT TO ARCHITECT REGARDING FOLLOWING ITEMS:
   - ANY HIDDEN ARTEFACTS
   - UNDERGROUND ROCK
   - TERMITES
   - ASBESTOS
   - CONTAMINATED SOIL
7. BUILDER TO ALLOW FOR HAZARDOUS MATERIALS AUDIT PRIOR TO DEMOLITION OF ANY WORKS RE: ASBESTOS REMOVAL WORK SEE PROVISIONAL SUMS ALLOWANCES FOR REMOVAL AND CERTIFICATION ALLOWANCE
8. CUT + SEAL ALL SERVICES INCLUDING REMOVAL OF U/GROUND PIPES AS REQUIRED
9. MAKE GOOD ALL FOOTPATHS, LANEWAY ETC. FOLLOWING BUILDING WORKS
10. DEMOLITION ORGANISED BY & CONTRACTED BY OWNER

CONTAMINATED SOIL:

1. THE SITE IS IN A CITY OF DAREBIN SPECIAL BUILDING OVERLAY.
2. SOME SOIL CONTAMINATION IS PRESENT.
3. REFER ESP REPORT + AUDITOR STATEMENT 22984 L1 Compliance Letter 221216
4. ESP TO BE ENGAGED TO INSPECT SUITE DURING EXCAVATIO TO DETERMINE CONTAMINATED SOIL TO BE REMOVED.
5. USE A LICENSED CONTAMINATED SOIL REMOVAL CONTRACTOR (ORGANISED BY & CONTRACTED BY OWNER)

DILAPIDATION REPORT:

1. ARRANGE AND DOCUMENT DILAPIDATION SURVEY TO ADJACENT PROPERTY AT 750 HIGH STREET, THORNBURY, PUBLISH PRIOR TO DEMOLITION.

RETAINED FITTINGS & MATERIALS

THE OWNER SHALL REMOVE ALL REQUIRED ITEMS PRIOR TO DEMOLITION. ALL REMAINING MATERIALS ARE THE RESPONSIBILITY OF THE DEMOLITION CONTRACTOR

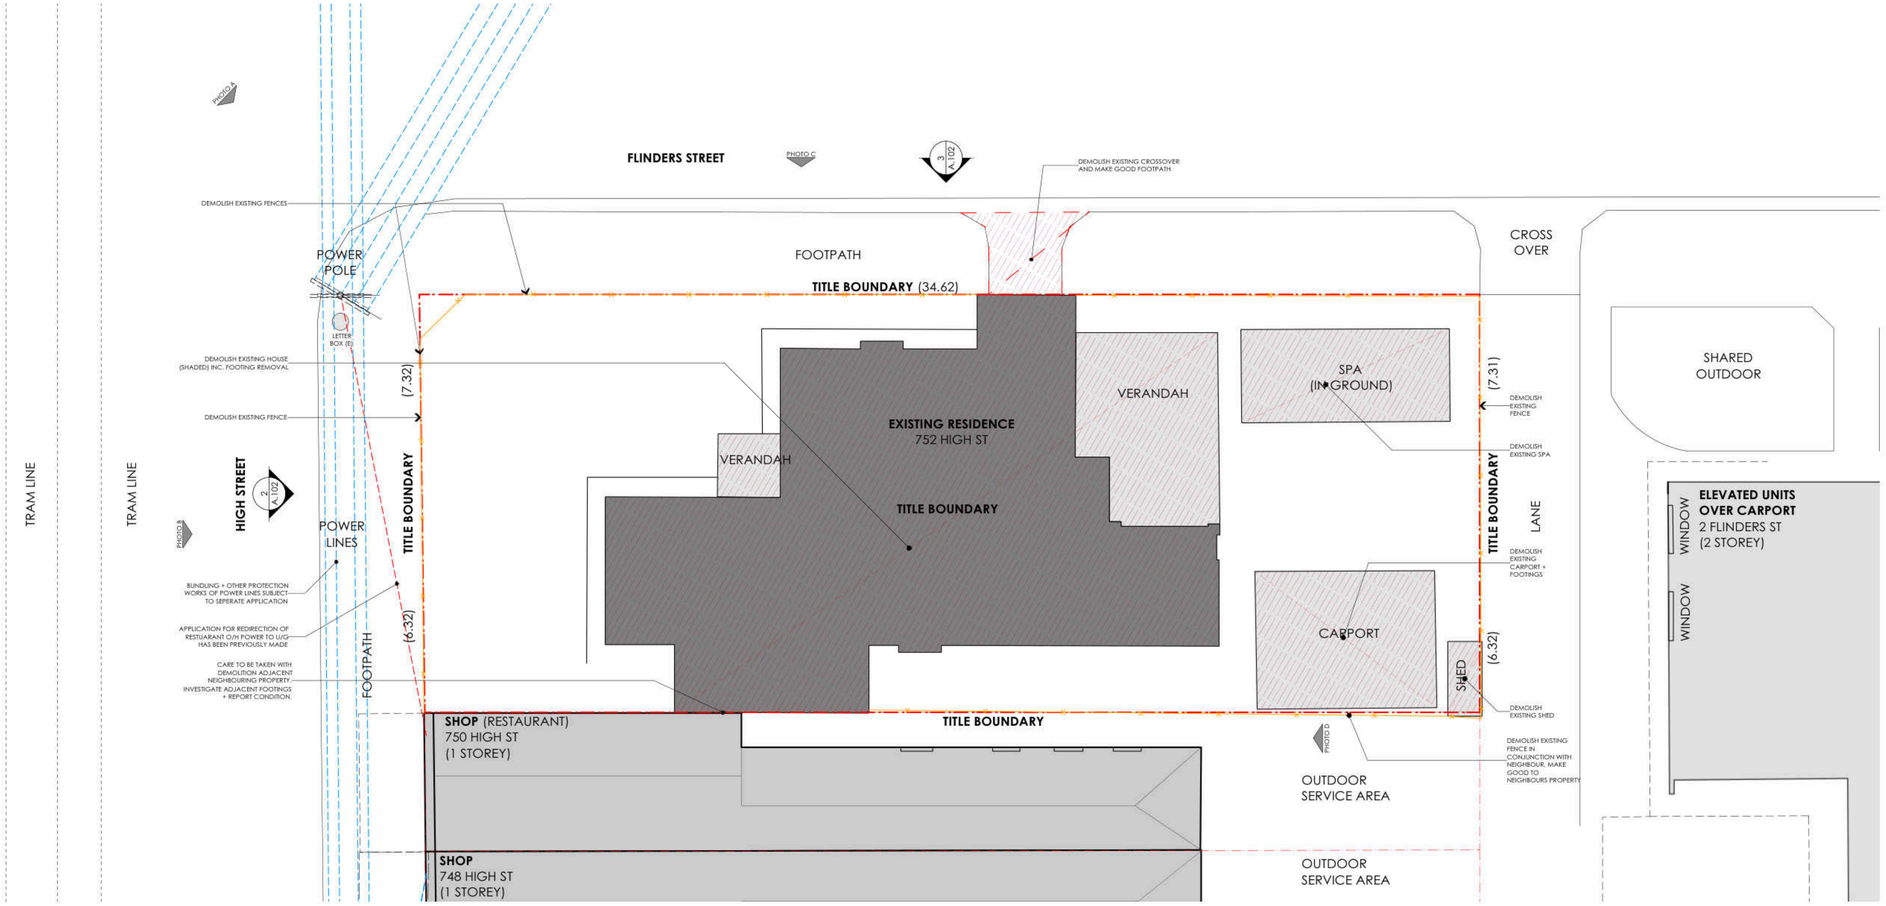

1 DEMOLITION PLAN
Scale: 1:100

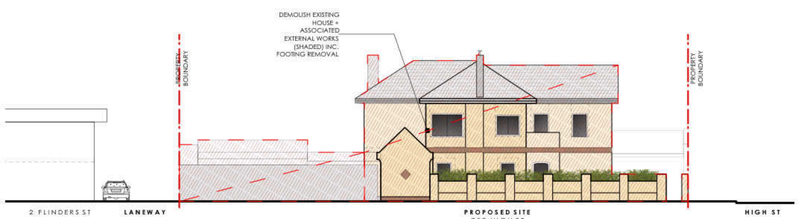

2 NORTH ELEVATION
Scale: 1:200

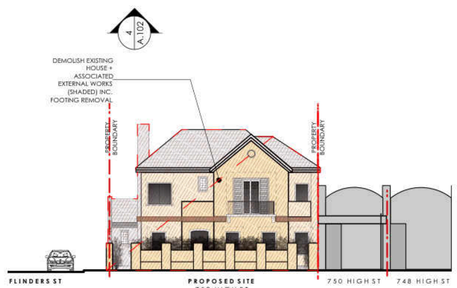

3 WEST ELEVATION
Scale: 1:200

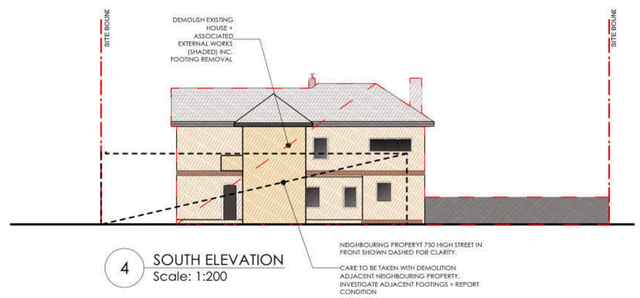

4 SOUTH ELEVATION
Scale: 1:200

FOR CONSTRUCTION - 17/12/19

ISSUE	DATE	REVISION
D	17/12/19	FOR CONSTRUCTION
C	31/5/19	CONTRACT SET

This drawing is to be read in conjuction with the other architectural documents including the specification and all relevant consultant's drawings. Contractors must verify all dimensions on site before commencing any shop drawings or fabrication. Do not scale any dimensions from drawings. Report any discrepancies or omissions to the Architect prior to proceeding.

CLIENT H.CHARALAMBOUS
Gardiner Architects
7/252 St Georges Rd, Fitzroy North, VIC, 3068
Ph: (03) 9486 4592 E: info@paulgardiner.com.au

DWG SITE PLAN - EXISTING & DEMOLITION
PROJECT RETAIL/RESIDENTIAL DEVELOPMENT
752 HIGH STREET, THORNBURY

JOB NO 141211
DRAWN BY AM
SCALE 1:200 @ A1
A.101
DWG #
REV# D

FLINDERS STREET

HIGH STREET

PROPERTY BOUNDARY

RETAIL
Area:137.2 sq m
(LV GR - LOWER)
FFL -0.13
RL 63.07

SHOP
750 HIGH ST

SHOP
748 HIGH ST

ENTRY
(TERR 1)

FOYER
(LV GR - UPPER)
FFL 0.00
RL 63.20

ACCESSIBLE WC

MALE WC (AMBULANT)

FEMALE WC (AMBULANT)

CL STORE

STORAGE CAGES

RESIDENT STORAGE

LIFT
(REFER SERVICES SPEC., FOR PRODUCT)

SHAFT SIZE
2040x2355

SUSTAINABLE TRANSPORT DISPLAY + RESIDENT NOTICE BOARD

BIKE STORE (9 SPACES TOTAL)

BIKE STORE (10 SPACES TOTAL)

NED KELLY BICYCLE PARKING RAILS, FIXED TO WALL IN STAGGERED ARRANGEMENT

RETAIL RUBBISH/RECYCLING

RESIDENCES RUBBISH/RECYCLING

90mm CONCRETE BLOCK WALL

FFL 0.00
RL 63.20

GREASE TRAP UNDER BINS

TRANSFER BAY
FFL -0.34
RL 62.86

MAX. RAMP DOWN 3% = 1.72m

TOTAL:
13 CAR SPACES

3 CAR STACKER

2 CAR STACKER

CARSTACKER, 3 LEVELS AT REAR + 2 LEVELS AT FRONT KLAUS MULTIPARKING COMBINATION OF 4300-200 (REAR) + 4000-210 (FRONT) (REFER TO SCHEDULE OF EQUIPMENT)

STRIP DRAIN AT END OF RAMP

WATER TANKS DOTTED UNDER

MAX. RAMP UP 5% = 2.86m

LINE OF FACE OF SHOTCRETE WALL BELOW

MULTIPLE RESIDENCES
2 FLINDERS ST

LANEWAY

COURTYARD

POS

EXISTING CROSSOVER

REMOVE EXISTING CROSSOVER + MAKE GOOD KERB + CHANNEL/FOOTPATH

AWNING RETURNS DOWN

AWNING OVER

CURVE CORNER

SERVICES CBRD (REFER A.404 FOR DETAIL)

FIRE SERVICE | WATER | GAS

SCV | METER/MSB | PILLAR

SERVICE METERS

SERVICES

SIGNAGE ON WALL

TILE CLADDING

EXISTING TEL. PILLAR

INTERCOM

POWER POLE

LETTER BOX

LETTERBOXES

SEAT (REFER A.407 DETAILS)

SLAB RECESS FOR ENTRY MAT (BY OTHERS)

TIMBER CLADDING TO 3 RECESSED ENTRY WALLS

KERB + CHANNEL

ASSUMED KITCHEN EXHAUST (BY OTHERS LATER) REFER TO ELEVATIONS

ASSUMED POSITION OF FUTURE COMMERCIAL KITCHEN

KITCHENETTE

OUTLINE OF BUILDING ABOVE

OVERALL

BUILDING/EXTERNAL WORKS

BUILDING

WINDOWS

SETBACK

BOUNDARY SETBACK

1 - A.301

2 - A.301

3 - A.302

4 - A.302

2 FLOOR PLAN - LEVEL GROUND
SCALE: 1:100

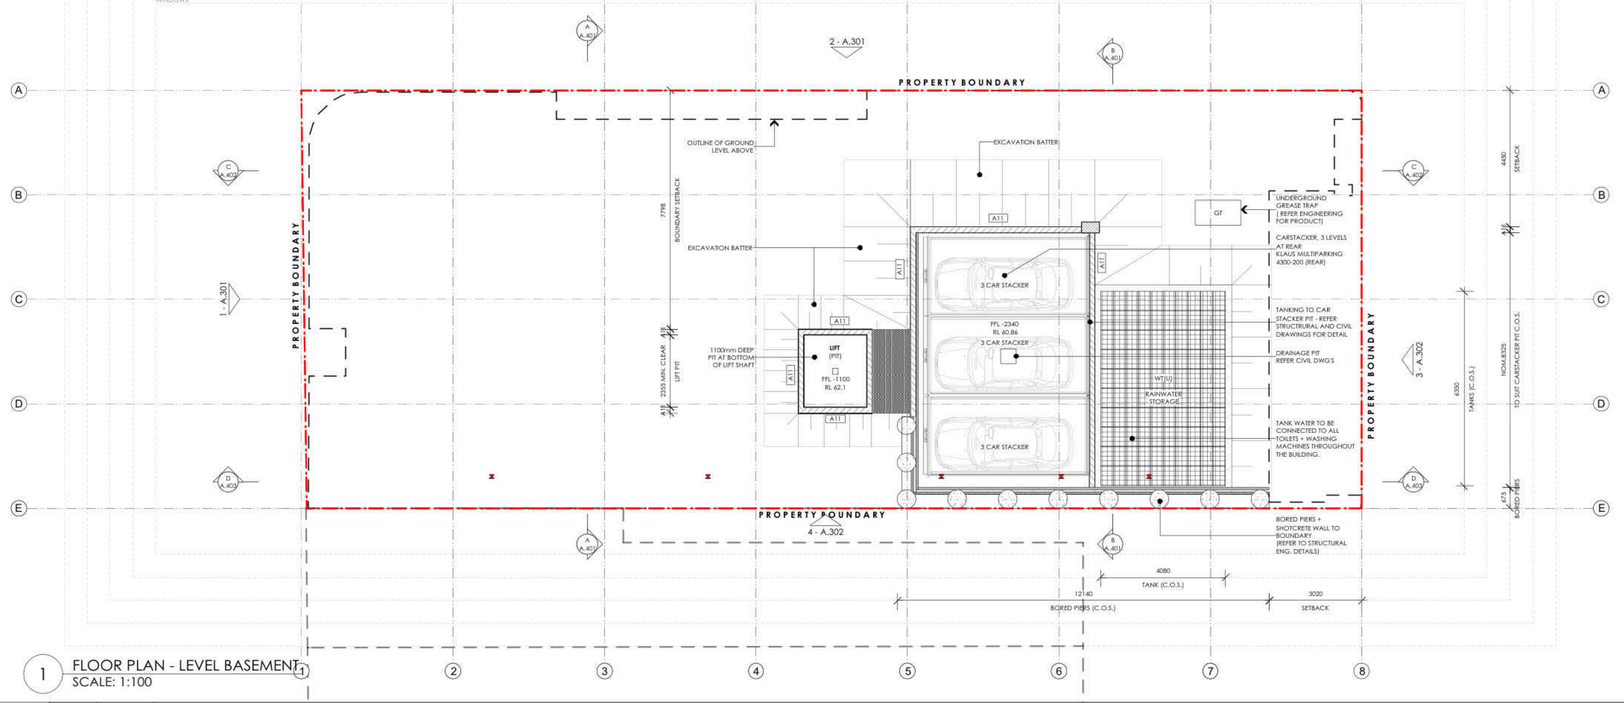

1 FLOOR PLAN - LEVEL BASEMENT
SCALE: 1:100

FLOOR PLAN NOTES
1. FIGURED DIMENSIONS TO BE TAKEN IN PREFERENCE TO SCALING
2. ALL DIMENSIONS ARE CLEAR UNLESS NOTED OTHERWISE
3. ARCHITECT TO CONFIRM SETOUT ON SITE
4. FOR ARCHITRAVES & SKIRTINGS REFER FINISHES PLAN A.205-A.207
5. FOR WALL FINISHES REFER FINISHES PLAN A.205-A.207
6. READ IN CONJUNCTION WITH SPECIFICATION FOR CONSTRUCTION & WORKMANSHIP STANDARDS

STRUCTURAL ENGINEERING
- PLANS TO BE READ IN CONJUCTION WITH SPECIFICATION + STRUCTURAL ENG'S DOCUMENTATION
- STUD FRAMING IN WALLS HIGHER THAN 2.7M TO BE ALTERED AS PER THE REQUIREMENTS OUTLINED IN THE TIMBER FRAMING CODE + STRUCTURAL ENGINEERS DOCUMENTATION
- REFER STRUCTURAL ENGINEERING DRAWINGS BY 4 SITE/VISTEK

FLOOR PLAN SYMBOLS LEGEND

WALL TYPES
- A1 EXTERNAL (REFER TO A.106 +A.107)
- B1 INTERNAL (REFER TO A.106 +A.107)

STRUCTURAL MEMBER
- C3 (REFER STRUCTURAL ENGINEERING)
- CC2 CONCRETE COLUMNS (REFER CONCRETE ENGINEERING)

FLOOR FINISHES
- CONC - REFER A.205, A.206 + A.207

WINDOWS
- G.01 W - REFER A.501-A.507

DOORS
- 1.01 D - REFER TO DOOR SCHEDULE

EXTERNAL BLIND
- BK - EXTERNAL MOTORISED ALUMINIUM VENETIAN BLIND (REFER A.405 FOR DETAIL + SCHEDULES FOR PRODUCT)

BALLUSTRADES
- BL1 - DELETED-
- BL2 BALUSTRADE TYPE 2 - REFER TO A.408 BALUSTRADE DETAIL
- BL3/PS BALUSTRADE TYPE 3 (INC. PRIVACY SCREEN) - REFER TO A.408 BALUSTRADE DETAIL
- BL4 BALUSTRADE TYPE 4 - REFER TO A.408 BALUSTRADE DETAIL
- BL5 BALUSTRADE TYPE 5 - REFER TO A.408 BALUSTRADE DETAIL
- PS PRIVACY SCREEN (FIXED METAL PRIVACY SCREEN) - REFER TO A.408 FOR DETAIL
- G1 GATE 1 - REFER TO GATE DETAIL

JOINERY + FURNITURE
- J JOINERY UNIT - REFER TO JOINERY DRAWINGS FOR DETAILS
- J (U) JOINERY UNIT UNDER - REFER TO JOINERY DRAWINGS FOR DETAILS
- LF LOOSE FURNITURE (BY OTHERS)

DRAINAGE
- DP DOWNPIPE
- BW BALCONY WASTE REFER DETAIL A AND DETAIL C ON A.406

GENERAL LEGEND
- 1.0 A.404 DETAIL REFERENCE CODE

CSD CAVITY SLIDING DOOR
SD SLIDING DOOR
DW DISH WASHER
FR FRIDGE
CBRD CUPBOARD
WM WASHING MACHINE
DR TUMBLE DRYER
BA HAND BASIN
TRH TOILET ROLL HOLDER
TR TOWEL RAIL
TRG TROUGH
CT COOK TOP
MC MIRROR CABINET
WB WASH BASIN
V VANITY
HTR HEATED TOWEL RAIL
HT HAND TOWEL HOLDER
R WARDROBE
FH FIRE HYDRANT
D DESK
BW BALCONY WASTE
CL CLEAR
S/O SET OUT
O/S OFFSET
C.O.S CHECK ON SITE
SCV SPRINKLER CONTROL VALVE

FRAME OUT WALL RECESS

ACCESSIBLE TURNING AREA

FIRE SERVICES

FC FIRE CURTAIN PRODUCT TBC

ISSUE	DATE	REVISION
D	17/12/19	FOR CONSTRUCTION
C	31/5/19	CONTRACT SET

This drawing to be read in conjunction with the other contract documents including the specification. Any discrepancies found in these documents during the course of the contract, Contractor must notify all dimensions must be checked on site before work. Do not scale any dimensions from drawings. Refer to Project Specification for all exceptions.

CLIENT H.CHARALAMBOUS

Gardiner Architects
7/252 St Georges Rd, Fitzroy North, VIC, 3068
Ph: (03) 9486 4092 E: info@paulgardiner.com.au

DWG FLOOR PLAN - BASEMENT/GROUND

PROJECT RETAIL/RESIDENTIAL DEVELOPMENT
752 HIGH STREET, THORNBURY

DRAWN BY AM
SCALE 1:100 @A1
JOB NO 141211
A.102
DWG #
REV# D

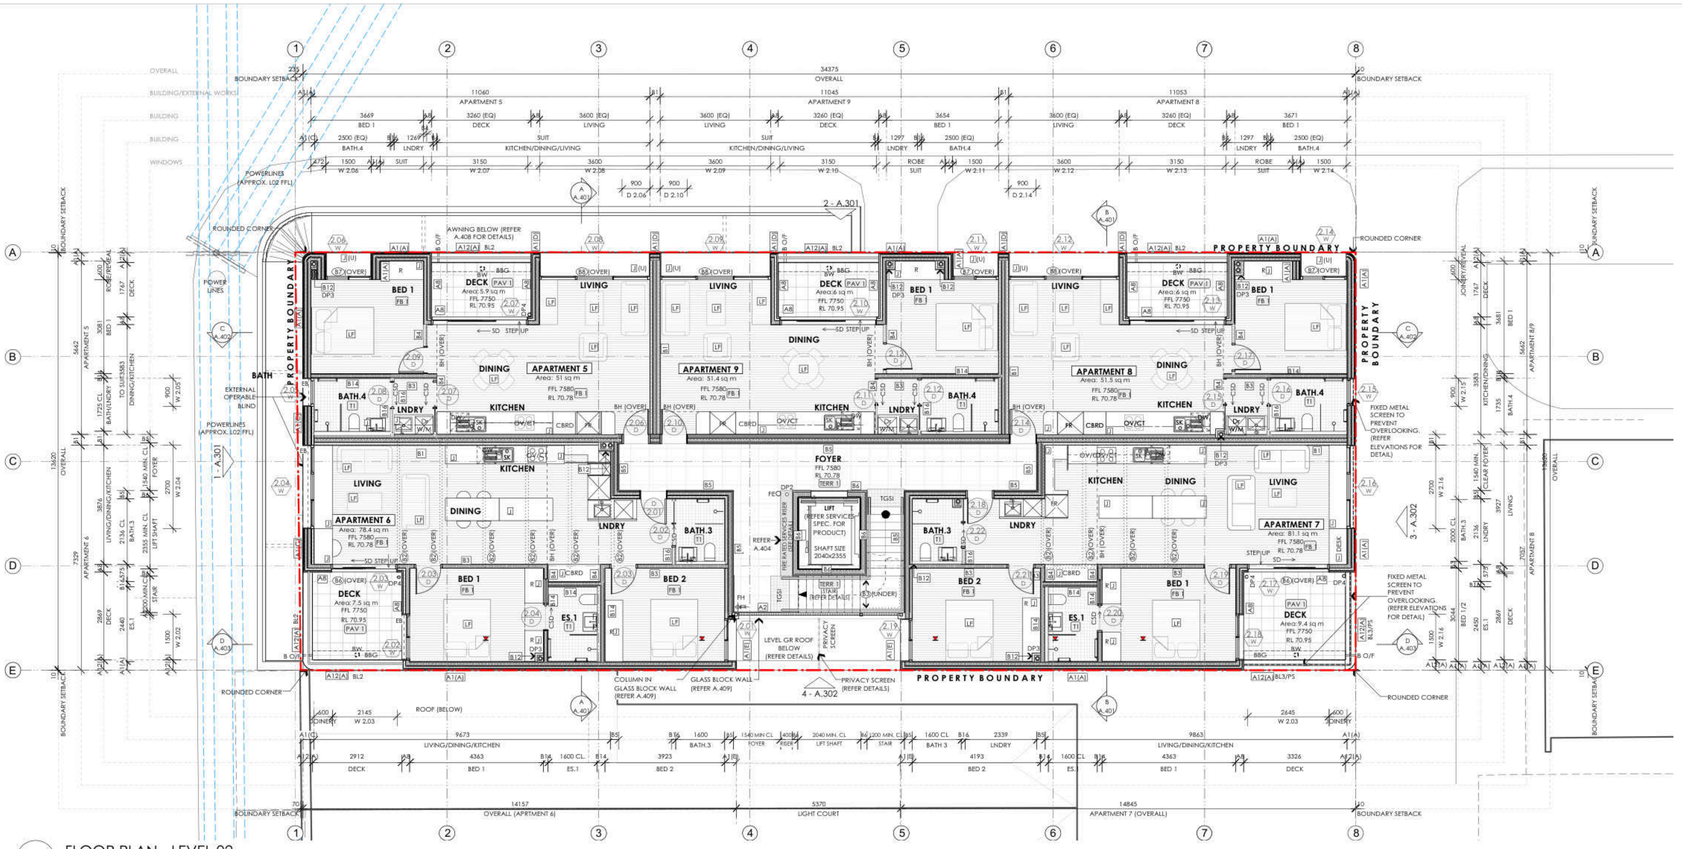

2 FLOOR PLAN - LEVEL 02
SCALE: 1:100

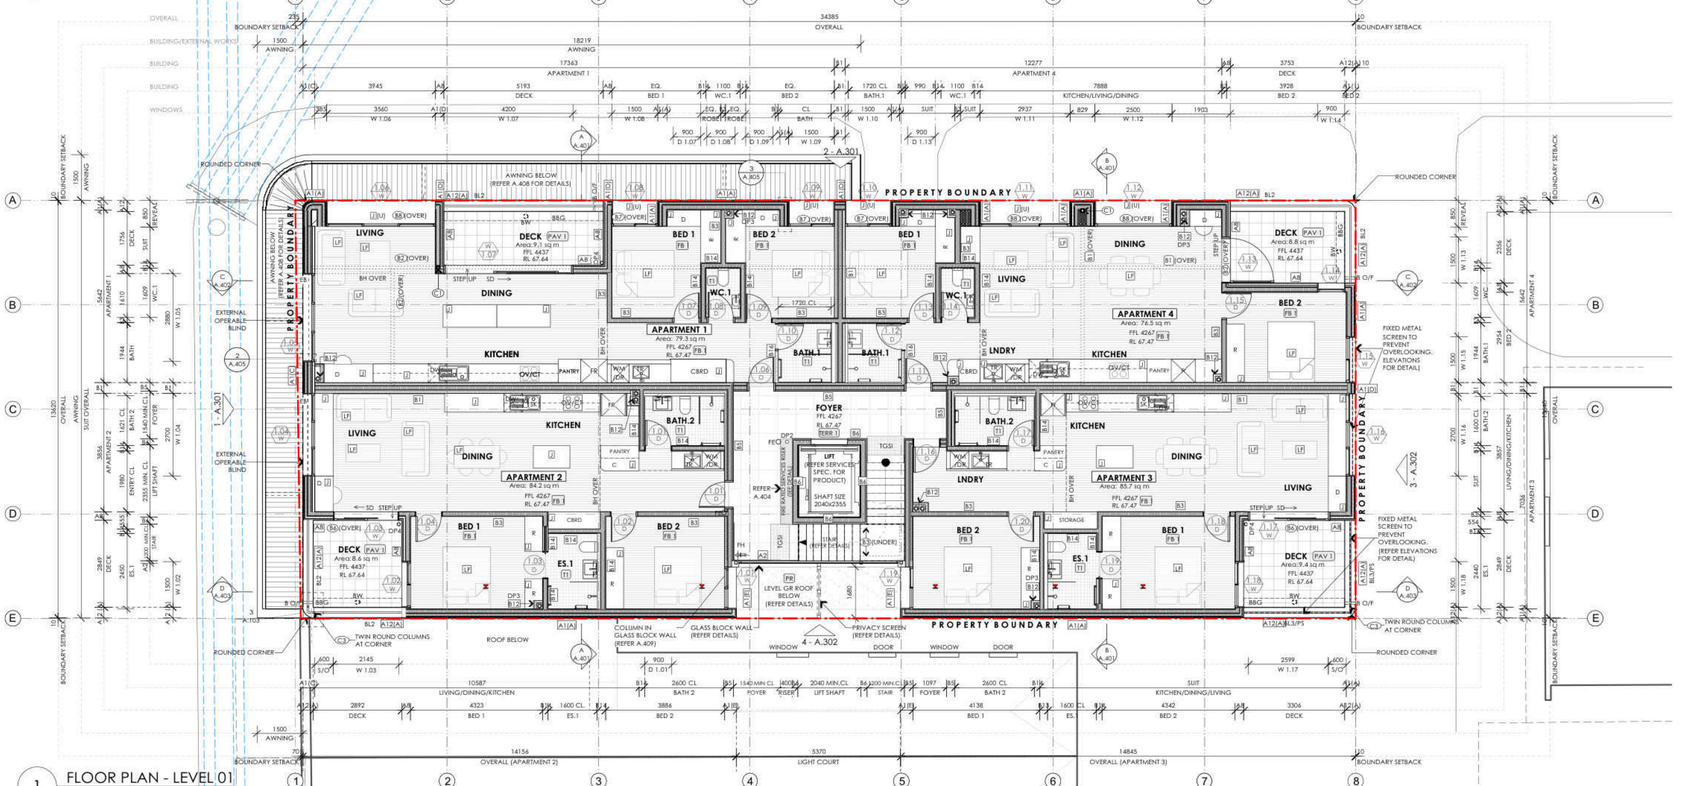

1 FLOOR PLAN - LEVEL 01
SCALE: 1:100

ROOF NOTES

GENERAL

1. READ IN CONJUNCTION WITH SPECIFICATION
2. **SARKING**
   ALL METAL ROOFING TO BE FITTED WITH ALUMINIUM FOIL SARKING & 25MM MINERAL WOOL BLANKET BETWEEN SARKING & U/S ROOFING
3. **FLASHINGS & CAPPINGS**
   ALLOW TO FLASH ALL JUNCTIONS TO WALLS & CAPPING TO ROOF EDGES
4. **PENETRATIONS**
   ALLOW FOR FLASHING TO ALL ROOF PENETRATIONS OVER & ABOVE INDICATED ON DRAWINGS TO PLUMBING VENTS ETC.
5. **WET DOWNPIPE SYSTEM**
   SYPHONIC ROOF DRAINAGE SYSTEM TO DRAIN ENTIRE LEVEL OS ROOF DECK OR ALTERNATIVE DRAINAGE TO APPROVAL

SUPPLY + INSTALL: SYFON SYSTEMS
CONTACT: (03) 9542 6000

ROOF LEGEND

ROOFING

MD1	METAL DECK ROOFING 1	PRODUCT: MATERIAL: COLOUR:	LYSAGHT TRIMDECK COLORBOND NIGHT SKY
WM	WETSUIT MEMBRANE ROOF APPLIED TO SUBSTRATE	[REFER A.107 FOR DETAILS]	
PB	PEBBLE ROOF	[REFER A.107 FOR DETAILS]	
TD	SELECTED TIMBER DECK		
MG	SELECTED METAL GRATE		

ACCESSORIES

R	RIDGE CAPPING	PRODUCT: MATERIAL: COLOUR:	PROPRIETARY COLORBOND FOLDED RIDGE FLASHING COLORBOND TO MATCH ROOFING (SEE EXT. FIN. SCHEDULE)
V	VALLEY GUTTER	PRODUCT: MATERIAL:	MEMBRANCE APPLIED TO SUBSTRATE TO FORM CUSTOM VALLEY GUTTER [REFER DETAIL.....] WETSUIT MEMBRANE
BC	BARGE CAPPING	PRODUCT: MATERIAL: COLOUR:	FOLDED METAL FLASHING (50mm DOWNTURN) - AS DETAILED COLORBOND TO MATCH ROOFING (SEE EXT. FIN. SCHEDULE)
DP1	DOWNPIPE 1	PRODUCT: MATERIAL: COLOUR:	76mm DIAM. DOWNPIPE COLORBOND TO MATCH ROOFING (SEE EXT. FIN. SCHEDULE)
DP2	DOWNPIPE 2	PRODUCT: MATERIAL: SUPPLIER:	50mm CHARGED SYPHONIC DOWNPIPE TBC SUPPLIED + INSTALLED BY SYFON SYSTEMS
DP3	DOWNPIPE 3	PRODUCT: MATERIAL: COLOUR:	100mm DIAM. PVC DOWNPIPE CONCEALED IN WALLS/ROOFS AS REQUIRED PER SITUATION PVC TBC (SEE DETAIL: A_____)
DP4	DOWNPIPE 4	PRODUCT: MATERIAL: COLOUR:	100mm DIAM. NOM. DOWNPIPE COLORBOND TO MATCH ROOFING (SEE EXT. FIN. SCHEDULE)
DP5	DOWNPIPE SPREADER	PRODUCT: MATERIAL: COLOUR:	100x50mm NOM. RECTANGULAR DPS COLORBOND TO MATCH ROOFING (SEE EXT. FIN. SCHEDULE)
EG	EAVES GUTTER	PRODUCT: MATERIAL: COLOUR:	NOM 115x90 METAL EAVES GUTTER (EG.: 'LYSAGHT QUAD GUTTER') WITH CONCEALED CLIPS COLORBOND TO MATCH ROOFING (SEE EXT. FIN. SCHEDULE)
EBG	EAVES BOX GUTTER	PRODUCT: MATERIAL:	CUSTOM FOLDED METAL TO MATCH ROOF MATERIAL + COLOUR REFER DETAILS AS CALLED OUT ON PLAN NOTES
BG	BOX GUTTER	PRODUCT: MATERIAL: COLOUR:	HEAVY GAUGE FABRICATED BOX GUTTER. STAINLESS STEEL TO MATCH ROOFING (SEE EXT. FIN. SCHEDULE)
BBG	BALCONY BOX GUTTER - SUB DECK DRAINAGE BOX GUTTER [REFER A.406 FOR DETAIL]		
RWH	RAINWATER HEAD	PRODUCT: MATERIAL: COLOUR:	CUSTOM FABRICATED RAINWATER HEAD. DOUBLE FOLDED JOINTS. POP OVERFLOW COLORBOND TO MATCH ROOFING (SEE EXT. FIN. SCHEDULE)
C	ROOF COWL	PRODUCT:	PROPRIETARY ROOF COWL AS REQUIRED BY INTERNAL EXHAUST FAN UNIT. SEE RCP. A.211 FOR UNIT SPECIFICATION BUILDER TO PROVIDE WATERPROOF CONNECTION WITH ROOFING
O/F	OVERFLOW	TAKEN FROM TANK TO LEGAL POINT POINT OF DISCHARGE. LOCATED AT STREET IN CURB/REAR LANE/LOCATION SHOWN	
B O/F	BALCONY OVERFLOW	SEE A.406 FOR DETAIL	
PC	PARAPET CAPPING	MATERIAL: COLOUR: REFER A.406 FOR DETAIL	5MM STEEL FLAT PLAT POWDERCOAT, BLACK

FLOOR PLAN NOTES

1. FIGURED DIMENSIONS TO BE TAKEN IN PREFERENCE TO SCALING
2. ALL DIMENSIONS ARE CLEAR UNLESS NOTED OTHERWISE
3. ARCHITECT TO CONFIRM SETOUT ON SITE
4. FOR ARCHITRAVES, & SKIRTINGS REFER FINISHES PLAN A.205-A.207
5. FOR WALL FINISHES REFER FINISHES PLAN A.205-A.207
6. READ IN CONJUNCTION WITH SPECIFICATION FOR CONSTRUCTION & WORKMANSHIP STANDARDS

STRUCTURAL ENGINEERING
- PLANS TO BE READ IN CONJUCTION WITH SPECIFICATION + STRUCTURAL ENG'S DOCUMENTATION
- STUD FRAMING IN WALLS HIGHER THAN 2.7M TO BE ALTERED AS PER THE REQUIREMENTS OUTLINED IN THE TIMBER FRAMING CODE + STRUCTURAL ENGINEERS DOCUMENTATION
- REFER STRUCTURAL ENGINEERING DRAWINGS BY 4 SITE/VISTEK

FLOOR PLAN SYMBOLS LEGEND

WALL TYPES
- A1 EXTERNAL [REFER TO A.106 +A.107]
- B1 INTERNAL [REFER TO A.106 +A.107]

STRUCTURAL MEMBER
- CS (REFER STRUCTURAL ENGINEERING)
- CC2 CONCRETE COLUMNS (REFER CONCRETE ENGINEERING)

FLOOR FINISHES
- CONC - REFER A.205, A.206 + A.207

WINDOWS
- 1.01 W - REFER A.501-A.507

DOORS
- 1.01 D - REFER TO DOOR SCHEDULE

EXTERNAL BLIND
- BK - EXTERNAL MOTORISED ALUMINIUM VENETIAN BLIND (REFER A.405 FOR DETAIL + SCHEDULES FOR PRODUCT)

BALUSTRADES
- BL1 - DELETED-
- BL2 BALUSTRADE TYPE 2 - REFER TO A.408 BALUSTRADE DETAIL
- BL3/PS BALUSTRADE TYPE 3 (INC. PRIVACY SCREEN) - REFER TO A.408 BALUSTRADE DETAIL
- BL4 BALUSTRADE TYPE 4 - REFER TO A.408 BALUSTRADE DETAIL
- BL5 BALUSTRADE TYPE 5 - REFER TO A.408 BALUSTRADE DETAIL
- PS PRIVACY SCREEN (FIXED METAL PRIVACY SCREEN) - REFER TO A.408 FOR DETAIL
- G1 GATE 1 - REFER TO GATE DETAIL

JOINERY + FURNITURE
- J JOINERY UNIT - REFER TO JOINERY DRAWINGS FOR DETAILS
- JJJ JOINERY UNIT UNDER - REFER TO JOINERY DRAWINGS FOR DETAILS
- LF LOOSE FURNITURE [BY OTHERS]

DRAINAGE
- DP DOWNPIPE
- BW BALCONY WASTE REFER DETAIL A AND DETAIL C ON A.406

GENERAL LEGEND
- 1.0 A.404 DETAIL REFERENCE CODE

CSD	CAVITY SLIDING DOOR
SD	SLIDING DOOR
DW	DISH WASHER
FR	FRIDGE
CBRD	CUPBOARD
WM	WASHING MACHINE
DR	TUMBLE DRYER
BA	HAND BASIN
TRH	TOILET ROLL HOLDER
TR	TOWEL RAIL
TRG	TROUGH
CT	COOK TOP
MC	MIRROR CABINET
WB	WASH BASIN
V	VANITY
HTR	HEATED TOWEL RAIL
HT	HAND TOWEL HOLDER
R	WARDROBE
FH	FIRE HYDRANT
D	DESK
BW	BALCONY WASTE
CL	CLEAR
S/O	SET OUT
O/S	OFFSET
C.O.S	CHECK ON SITE
SCV	SPRINKLER CONTROL VALVE

- FRAME OUT WALL RECESS
- ACCESSIBLE TURNING AREA

FIRE SERVICES
- FC FIRE CURTAIN PRODUCT TBC

STORMWATER & WATER HARVESTING LEGEND

NOTE: REFER SERVICES PLAN DRAWINGS FOR SPECIFIC WATER HARNESSING + RETICULATION FUNCTIONAL INFORMATION

WG(U) BELOW GROUND WATER TANK	PRODUCT: MATERIAL: SIZE: LITRE:	ARTLANTIS FLO-TANK, 40 X TRIPLE STACKED MODULE POLYCARBONATE/STAINLESS STEEL TBC TRIPLE MODULE 1310H X 408W X 685L TOTAL FOOTPRINT 1.632 X 6350 40 X 347.8 TRIPLE MODULES 13,912 LITRES TOTAL CAPACITY

PUMPS & VALVES

- PROVIDE APPROVED PROPRIETARY PUMP WITH MAINS TOP UP FACILITY
- PROVIDE 'RAINBIRD' OR SIMILAR ALARM AND GAUGE, GENERALLY ALLOWING CONTROL OF FUNCTIONS.
- PROVIDE ENCLOSURE TO MANUFACTURERS RECOMMENDATIONS

FLAT COLOURBOND STEEL SHEET ON SUBSTRATE
COLOUR: BLACK

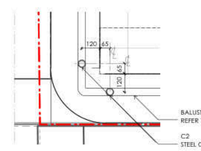

3 FLOOR PLAN DETAIL 1
SCALE: 1:20

FOR CONSTRUCTION - 17/12/19

ISSUE	DATE	REVISION
F	17/12/19	FOR CONSTRUCTION
E	23/10/19	FOR CLT SHOP DRAWING
D	6/6/19	EARLY WORKS PERMIT (CONSTRUCTION ISSUE)
C	31/5/19	CONTRACT SET

This drawing is issued in conjunction with the other architectural documents including the project specification. Do not scale this drawing. Check all dimensions on site. The Contractor is to notify all dimensional discrepancies to the Architect before proceeding with the work. Any deviations are to be approved by the Architect or Consultants prior to proceeding.

CLIENT H.CHARALAMBOUS

Gardiner Architects
7/252 St Georges Rd, Fitzroy North, VIC, 3068
Ph: (03) 9486 4092 E: info@paulgardiner.com.au

DWG: **FLOOR PLAN - LEVEL 01 + 02**
PROJECT: RETAIL/RESIDENTIAL DEVELOPMENT
752 HIGH STREET, THORNBURY
DRAWN BY: AM
SCALE: 1:100 @ A1
JOB NO: 141211
DWG #: A.103
REV: F

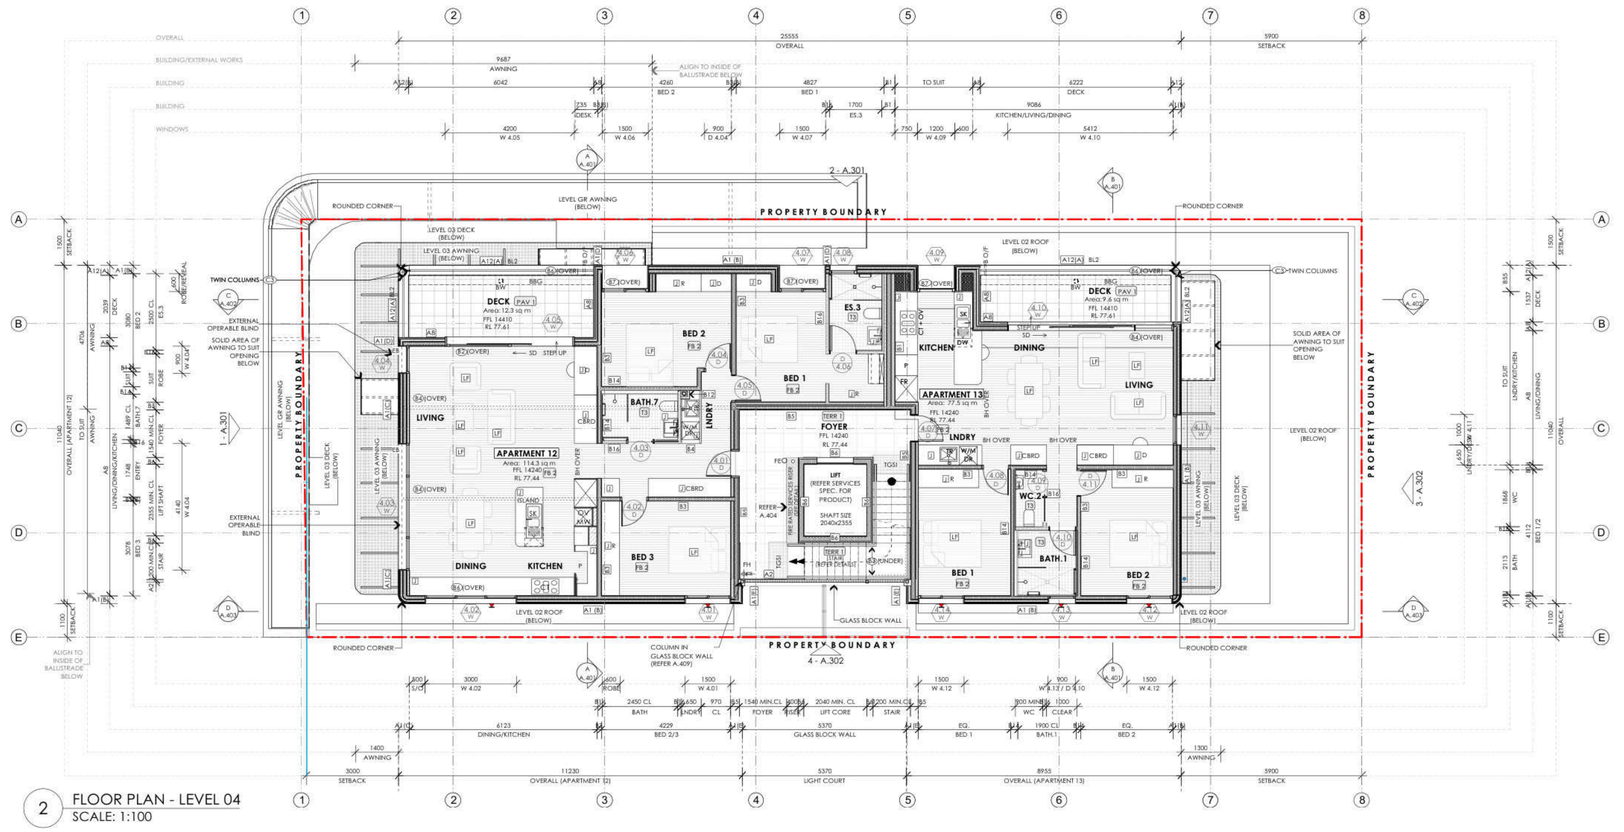

2 FLOOR PLAN - LEVEL 04
SCALE: 1:100

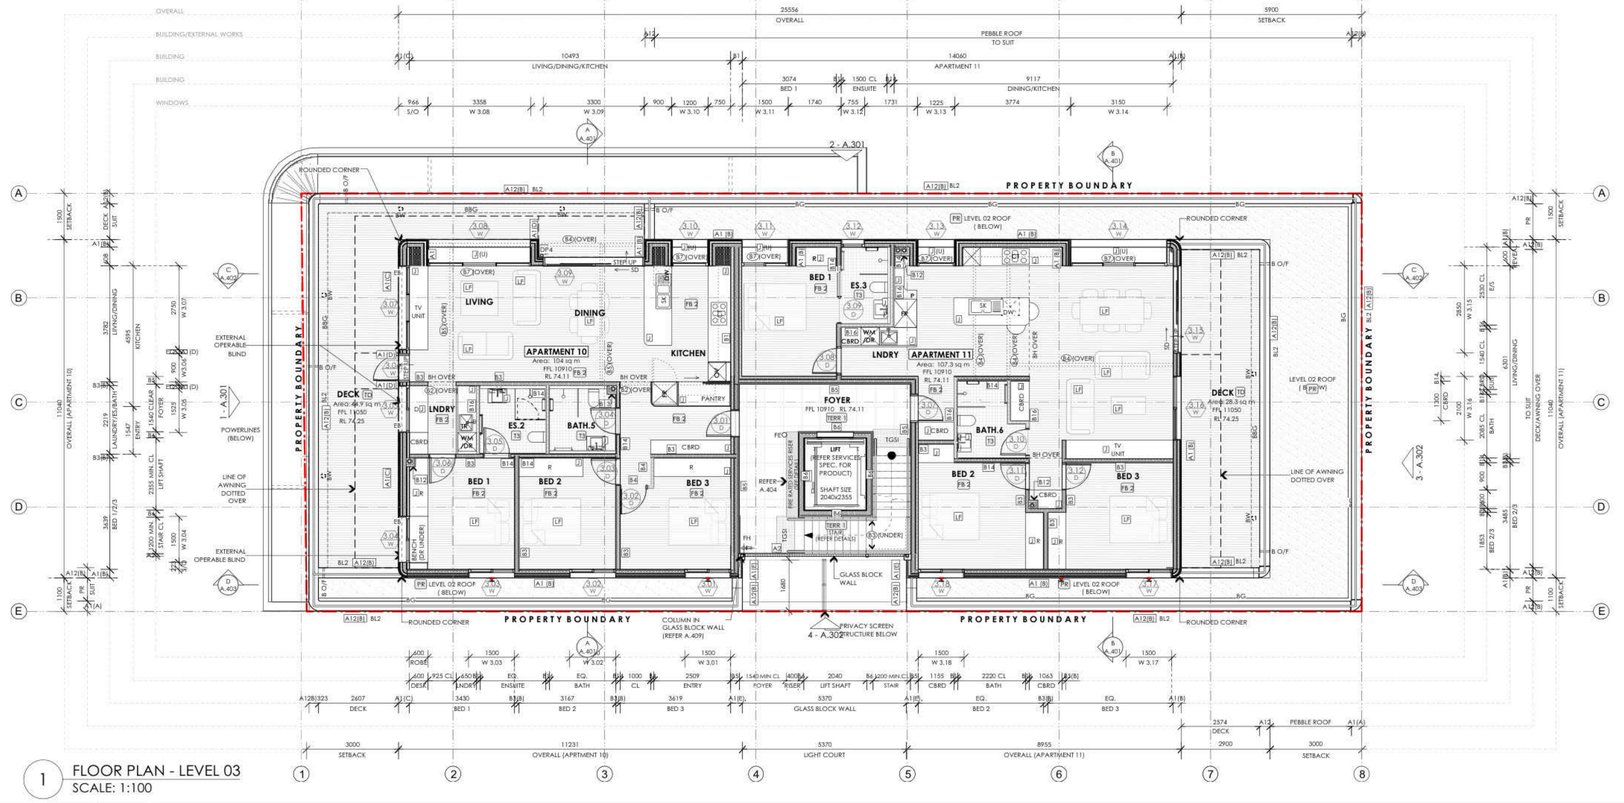

1 FLOOR PLAN - LEVEL 03
SCALE: 1:100

ROOF NOTES

GENERAL

1. READ IN CONJUNCTION WITH SPECIFICATION
2. **SARKING**
   ALL METAL ROOFING TO BE FITTED WITH ALUMINIUM FOIL SARKING & 25MM MINERAL WOOL BLANKET BETWEEN SARKING & U/S ROOFING
3. **FLASHINGS & CAPPINGS**
   ALLOW TO FLASH ALL JUNCTIONS TO WALLS & CAPPING TO ROOF EDGES
4. **PENETRATIONS**
   ALLOW FOR FLASHING TO ALL ROOF PENETRATIONS OVER & ABOVE INDICATED ON DRAWINGS TO PLUMBING VENTS ETC.
5. **WET DOWNPIPE SYSTEM**
   SYPHONIC ROOF DRAINAGE SYSTEM TO DRAIN ENTIRE LEVEL 05 ROOF DECK OR ALTERNATIVE DRAINAGE TO APPROVAL

SUPPLY + INSTALL: SYFON SYSTEMS
CONTACT: (03) 9542 6000

ROOF LEGEND

ROOFING

MD1	METAL DECK ROOFING 1	PRODUCT: LYSAGHT TRIMDECK MATERIAL: COLORBOND COLOUR: NIGHT SKY	
WM	WETSUIT MEMBRANE ROOF APPLIED TO SUBSTRATE	[REFER A.107 FOR DETAILS]	
PB	PEBBLE ROOF	[REFER A.107 FOR DETAILS]	
TD	SELECTED TIMBER DECK		
MG	SELECTED METAL GRATE		

ACCESSORIES

R	RIDGE CAPPING	PRODUCT: PROPRIETARY COLORBOND FOLDED RIDGE FLASHING MATERIAL: COLORBOND COLOUR: TO MATCH ROOFING (SEE EXT. FIN. SCHEDULE)	
V	VALLEY GUTTER	PRODUCT: MEMBRANCE APPLIED TO SUBSTRATE TO FORM CUSTOM VALLEY GUTTER [REFER DETAIL....] MATERIAL: WETSUIT MEMBRANE	
BC	BARGE CAPPING	PRODUCT: FOLDED METAL FLASHING (50mm DOWNTURN) - AS DETAILED MATERIAL: COLORBOND COLOUR: TO MATCH ROOFING (SEE EXT. FIN. SCHEDULE)	
DP1	DOWNPIPE 1	PRODUCT: 75mm DIAM. DOWNPIPE MATERIAL: COLORBOND COLOUR: TO MATCH ROOFING (SEE EXT. FIN. SCHEDULE)	
DP2	DOWNPIPE 2	PRODUCT: 50mm CHARGED SYPHONIC DOWNPIPE MATERIAL: TBC SUPPLIER: SUPPLIED + INSTALLED BY SYFON SYSTEMS	
DP3	DOWNPIPE 3	PRODUCT: 100mm DIAM. PVC DOWNPIPE CONCEALED IN WALLS/ROOFS AS REQUIRED PER SITUATION MATERIAL: PVC COLOUR: TBC (SEE DETAIL A_____)	
DP4	DOWNPIPE 4	PRODUCT: 100mm DIAM. NOM. DOWNPIPE MATERIAL: COLORBOND COLOUR: TO MATCH ROOFING (SEE EXT. FIN. SCHEDULE)	
DPS	DOWNPIPE SPREADER	PRODUCT: 100x50mm NOM. RECTANGULAR DPS MATERIAL: COLORBOND COLOUR: TO MATCH ROOFING (SEE EXT. FIN. SCHEDULE)	
EG	EAVES GUTTER	PRODUCT: NOM 115x90 METAL EAVES GUTTER (EG. 'LYSAGHT QUAD GUTTER') WITH CONCEALED CLIPS MATERIAL: COLORBOND COLOUR: TO MATCH ROOFING (SEE EXT. FIN. SCHEDULE)	
EBG	EAVES BOX GUTTER	PRODUCT: CUSTOM FOLDED METAL TO MATCH ROOF MATERIAL + COLOUR REFER DETAILS AS CALLED OUT ON PLAN NOTES	
BG	BOX GUTTER	PRODUCT: HEAVY GAUGE FABRICATED BOX GUTTER. MATERIAL: STAINLESS STEEL COLOUR: TO MATCH ROOFING (SEE EXT. FIN. SCHEDULE)	
BBG	BALCONY BOX GUTTER - SUB DECK DRAINAGE BOX GUTTER [REFER A.406 FOR DETAIL]		
RWH	RAINWATER HEAD	PRODUCT: CUSTOM FABRICATED RAINWATER HEAD. DOUBLE FOLDED JOINTS. POP OVERFLOW MATERIAL: COLORBOND	
C	ROOF COWL	PRODUCT: PROPRIETARY ROOF COWL AS REQUIRED BY INTERNAL EXHAUST FAN UNIT. SEE RCP A.211 FOR UNIT SPECIFICATION BUILDER TO PROVIDE WATERPROOF CONNECTION WITH ROOFING	
O/F	OVERFLOW	TAKEN FROM TANK TO LEGIAL POINT POINT OF DISCHARGE; LOCATED AT STREET IN CURB/REAR LANE/LOCATION SHOWN	
B O/F	BALCONY OVERFLOW- SEE A.406 FOR DETAIL		
PC	PARAPET CAPPING	MATERIAL: 5MM STEEL FLAT PLAT COLOUR: POWDERCOAT, BLACK REFER A.406 FOR DETAIL	

FLOOR PLAN NOTES

1. FIGURED DIMENSIONS TO BE TAKEN IN PREFERENCE TO SCALING
2. ALL DIMENSIONS ARE CLEAR UNLESS NOTED OTHERWISE
3. ARCHITECT TO CONFIRM SETOUT ON SITE
4. FOR ARCHITRAVES, & SKIRTINGS REFER FINISHES PLAN A.205-A.207
5. FOR WALL FINISHES REFER FINISHES PLAN A.205-A.207
6. READ IN CONJUNCTION WITH SPECIFICATION FOR CONSTRUCTION & WORKMANSHIP STANDARDS

STRUCTURAL ENGINEERING
- PLANS TO BE READ IN CONJUCTION WITH SPECIFICATION + STRUCTURAL ENG'S DOCUMENTATION
- STUD FRAMING IN WALLS HIGHER THAN 2.7M TO BE ALTERED AS PER THE REQUIREMENTS OUTLINED IN THE TIMBER FRAMING CODE + STRUCTURAL ENGINEERS DOCUMENTATION
- REFER STRUCTURAL ENGINEERING DRAWINGS BY 4 SITE/VISTEK

FLOOR PLAN SYMBOLS LEGEND

WALL TYPES
- A1 EXTERNAL [REFER TO A.106 +A.107]
- B1 INTERNAL [REFER TO A.106 +A.107]

STRUCTURAL MEMBER
- C3 (REFER STRUCTURAL ENGINEERING)
- CC2 CONCRETE COLUMNS [REFER CONCRETE ENGINEERING]

FLOOR FINISHES
- CONC - REFER A.205, A.206 + A.207

WINDOWS
- 1.01 W - REFER A.501-A.507

DOORS
- 1.01 D - REFER TO DOOR SCHEDULE

EXTERNAL BLIND
- BK - EXTERNAL MOTORISED ALUMINIUM VENETIAN BLIND (REFER A.405 FOR DETAIL + SCHEDULES FOR PRODUCT)

BALUSTRADES
- BL1 - DELETED-
- BL2 BALUSTRADE TYPE 2 - REFER TO A.408 BALUSTRADE DETAIL
- BL3/PS BALUSTRADE TYPE 3 (INC. PRIVACY SCREEN) - REFER TO A.408 BALUSTRADE DETAIL
- BL4 BALUSTRADE TYPE 4 - REFER TO A.408 BALUSTRADE DETAIL
- BL5 BALUSTRADE TYPE 5 - REFER TO A.408 BALUSTRADE DETAIL
- PS PRIVACY SCREEN (FIXED METAL PRIVACY SCREEN) - REFER TO A.408 FOR DETAIL
- G1 GATE 1 - REFER TO GATE DETAIL

JOINERY + FURNITURE
- J JOINERY UNIT - REFER TO JOINERY DRAWINGS FOR DETAILS
- J (U) JOINERY UNIT UNDER - REFER TO JOINERY DRAWINGS FOR DETAILS
- LF LOOSE FURNITURE (BY OTHERS)

DRAINAGE
- DP DOWNPIPE
- BW BALCONY WASTE REFER DETAIL A AND DETAIL C ON A.406

GENERAL LEGEND
- 1.0 A.404 DETAIL REFERENCE CODE

CSD	CAVITY SLIDING DOOR
SD	SLIDING DOOR
DW	DISH WASHER
FR	FRIDGE
CBRD	CUPBOARD
WM	WASHING MACHINE
DR	TUMBLE DRYER
BA	HAND BASIN
TRH	TOILET ROLL HOLDER
TR	TOWEL RAIL
TRG	TROUGH
CT	COOK TOP
MC	MIRROR CABINET
WB	WASH BASIN
V	VANITY
HTR	HEATED TOWEL RAIL
HT	HAND TOWEL HOLDER
R	WARDROBE
FH	FIRE HYDRANT
D	DESK
BW	BALCONY WASTE
CL	CLEAR
S/O	SET OUT
O/S	OFFSET
C.O.S	CHECK ON SITE
SCV	SPRINKLER CONTROL VALVE
	FRAME OUT WALL RECESS
	ACCESSIBLE TURNING AREA

FIRE SERVICES
- FC FIRE CURTAIN PRODUCT TBC

STORMWATER & WATER HARVESTING LEGEND

NOTE: REFER SERVICES PLAN DRAWINGS FOR SPECIFIC WATER HARNESSING + RETICULATION FUNCTIONAL INFORMATION

DIMENSIONS ARE FOR SCOPING PURPOSES AND SHOW DESIGN INTENT

WSE(I) BELOW GROUND WATER TANK — PRODUCT: ARTLANTIS FLO-TANK, 40 X TRIPLE STACKED MODULES

ISSUE	DATE	REVISION
E	17/12/19	FOR CONSTRUCTION
D	25/10/19	FOR CLT SHOP DRAWING
C	31/5/19	CONTRACT SET

This drawing to be read in conjunction with the other contract documents including the specification. Any discrepancies found during the course of the contract, Contractor to notify all dimensions on site prior to commencement of work. Do not scale any dimensions from drawings. Allow for thickness of construction and equipment.

FOR CONSTRUCTION - 17/12/19

Gardiner Architects
7/252 St Georges Rd, Fitzroy North, VIC, 3068
Ph: (03) 9486 4092 E: info@paulgardiner.com.au

CLIENT H.CHARALAMBOUS
DWG FLOOR PLAN - LEVEL 03 + 04
PROJECT RETAIL/RESIDENTIAL DEVELOPMENT 752 HIGH STREET, THORNBURY
DRAWN BY AM
SCALE 1:100 @ A1
JOB NO 141211
A.104
DWG #
REV# E

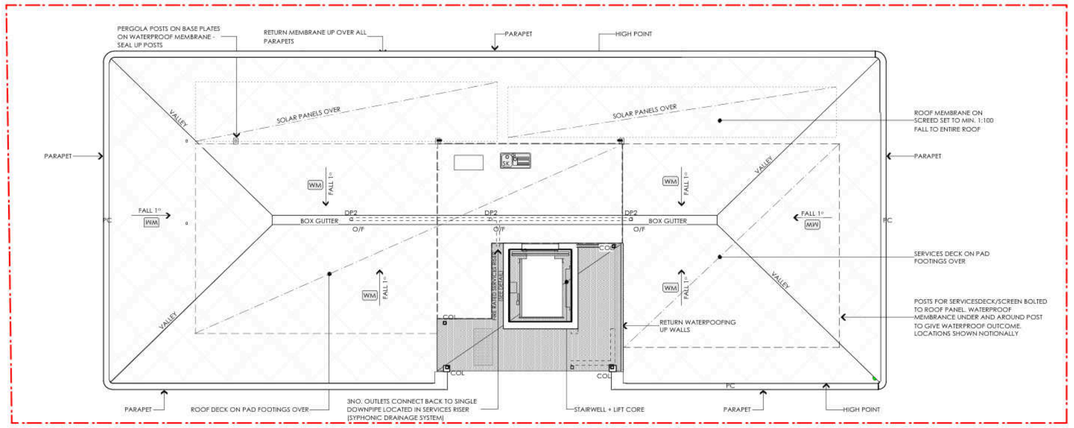

2 ROOF DECK - DRAINAGE PLAN
SCALE: 1:100

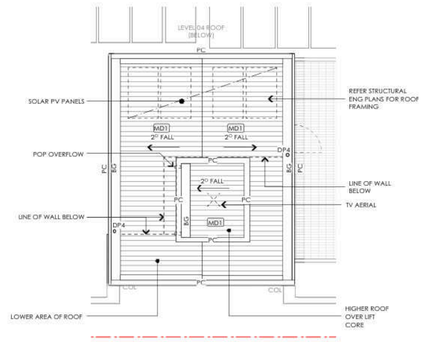

3 ROOF PLAN - LEVEL 05
SCALE: 1:100

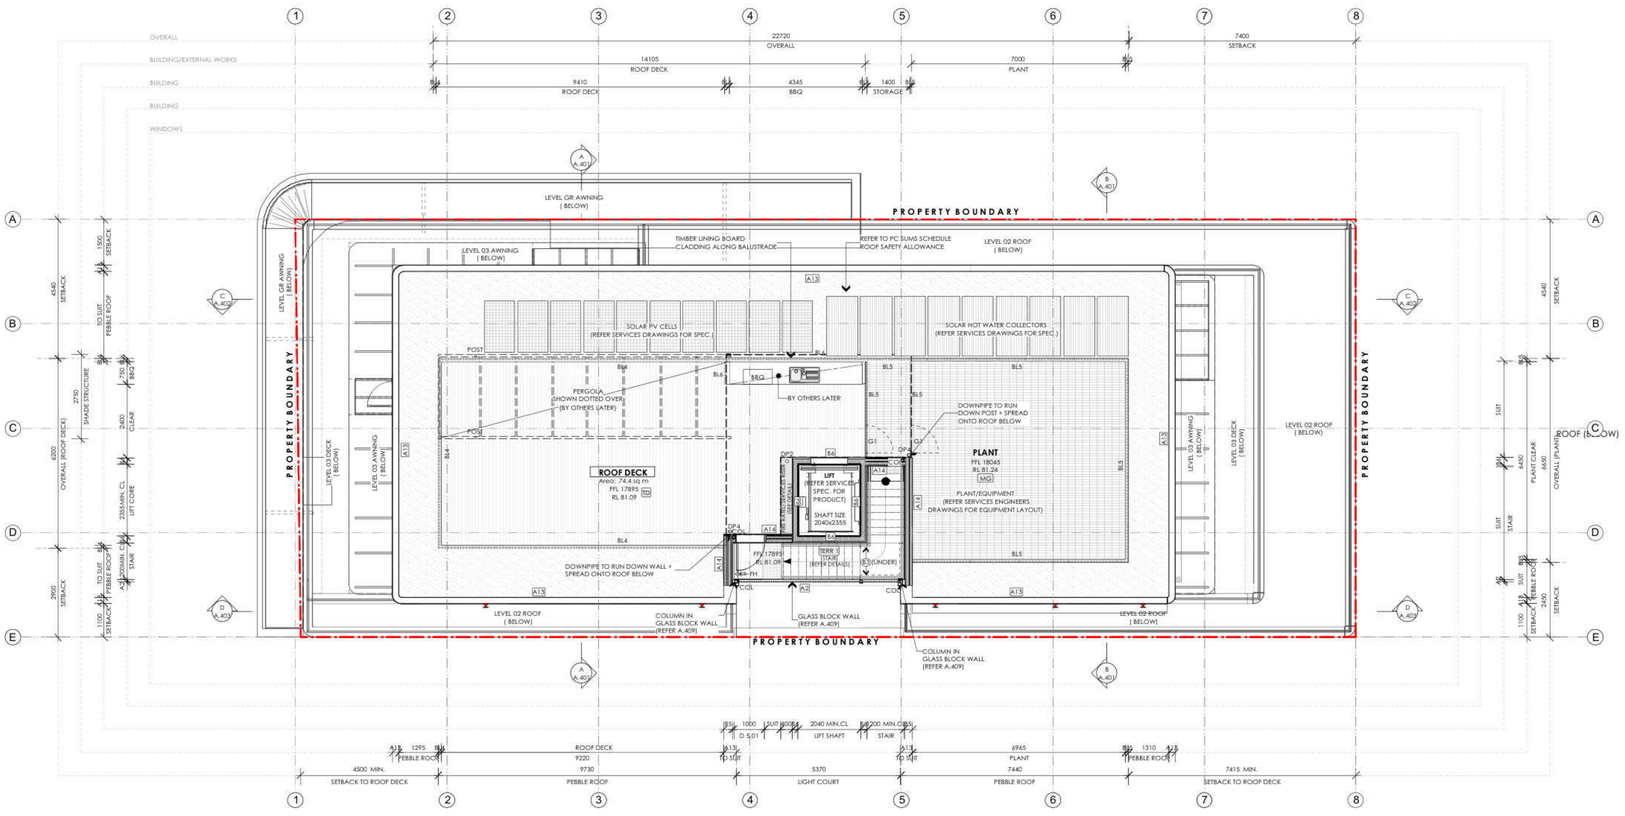

1 FLOOR PLAN - LEVEL 05
SCALE: 1:100

ROOF NOTES

GENERAL

1. READ IN CONJUNCTION WITH SPECIFICATION
2. **SARKING**
   ALL METAL ROOFING TO BE FITTED WITH ALUMINIUM FOIL SARKING & 25MM MINERAL WOOL BLANKET BETWEEN SARKING & U/S ROOFING
3. **FLASHINGS & CAPPINGS**
   ALLOW TO FLASH ALL JUNCTIONS TO WALLS & CAPPING TO ROOF EDGES
4. **PENETRATIONS**
   ALLOW FOR FLASHING TO ALL ROOF PENETRATIONS OVER & ABOVE INDICATED ON DRAWINGS TO PLUMBING VENTS ETC.
5. **WET DOWNPIPE SYSTEM**
   SYPHINIC ROOF DRAINAGE SYSTEM TO DRAIN ENTIRE LEVEL 05 ROOF DECK OR ALTERNATIVE DRAINAGE TO APPROVAL

SUPPLY + HSTALL: SYFON SYSTEMS
CONTACT: (03) 9542 6000

ROOF LEGEND

ROOFING

MD1	METAL DECK ROOFING 1	PRODUCT: LYSAGHT TRIMDECK MATERIAL: COLORBOND COLOUR: NIGHT SKY
WM	WETSUIT MEMBRANE ROOF APPLIED TO SUBSTRATE	[REFER A.107 FOR DETAILS]
PR	PEBBLE ROOF	[REFER A.107 FOR DETAILS]
TD	SELECTED TIMBER DECK	
MG	SELECTED METAL GRATE	

ACCESSORIES

R	RIDGE CAPPING	PRODUCT: PROPRIETARY COLORBOND FOLDED RIDGE FLASHING MATERIAL: COLORBOND COLOUR: TO MATCH ROOFING (SEE EXT. FIN. SCHEDULE)
V	VALLEY GUTTER	PRODUCT: MEMBRANCE APPLIED TO SUBSTRATE TO FORM CUSTOM VALLEY GUTTER [REFER DETAIL....] MATERIAL: WETSUIT MEMBRANE
BC	BARGE CAPPING	PRODUCT: FOLDED METAL FLASHING (50mm DOWNTURN) - AS DETAILED MATERIAL: COLORBOND COLOUR: TO MATCH ROOFING (SEE EXT. FIN. SCHEDULE)
DP1	DOWNPIPE 1	PRODUCT: 76mm DIAM. DOWNPIPE MATERIAL: COLORBOND COLOUR: TO MATCH ROOFING (SEE EXT. FIN. SCHEDULE)
DP2	DOWNPIPE 2	PRODUCT: 50mm CHARGED SYPHONIC DOWNPIPE MATERIAL: TBC SUPPLIER: SUPPLIED + INSTALLED BY SYFON SYSTEMS
DP3	DOWNPIPE 3	PRODUCT: 100mm DIAM. PVC DOWNPIPE CONCEALED IN WALLS/ROOFS AS REQUIRED PER SITUATION MATERIAL: PVC COLOUR: TBC (SEE DETAIL A_____)
DP4	DOWNPIPE 4	PRODUCT: 100mm DIAM. NOM. DOWNPIPE MATERIAL: COLORBOND COLOUR: TO MATCH ROOFING (SEE EXT. FIN. SCHEDULE)
DP5	DOWNPIPE SPREADER	PRODUCT: 100x50mm NOM. RECTANGULAR DPS MATERIAL: COLORBOND COLOUR: TO MATCH ROOFING (SEE EXT. FIN. SCHEDULE)
EG	EAVES GUTTER	PRODUCT: NOM 115x90 METAL EAVES GUTTER (EG. 'LYSAGHT QUAD GUTTER') WITH CONCEALED CLIPS MATERIAL: COLORBOND COLOUR: TO MATCH ROOFING (SEE EXT. FIN. SCHEDULE)
EBG	EAVES BOX GUTTER	PRODUCT: CUSTOM FOLDED METAL TO MATCH ROOF MATERIAL + COLOUR REFER DETAILS AS CALLED OUT ON PLAN NOTES
BG	BOX GUTTER	PRODUCT: HEAVY GAUGE FABRICATED BOX GUTTER. MATERIAL: STAINLESS STEEL COLOUR: TO MATCH ROOFING (SEE EXT. FIN. SCHEDULE)
BBG	BALCONY BOX GUTTER - SUB DECK DRAINAGE BOX GUTTER [REFER A.406 FOR DETAIL]	
RWH	RAINWATER HEAD	PRODUCT: CUSTOM FABRICATED RAINWATER HEAD. MATERIAL: COLORBOND COLOUR: TO MATCH ROOFING (SEE EXT. FIN. SCHEDULE) DOUBLE FOLDED JOINTS. POP OVERFLOW
C	ROOF COWL	PRODUCT: PROPRIETARY ROOF COWL AS REQUIRED BY INTERNAL EXHAUST FAN UNIT. SEE RCP A.211 FOR UNIT SPECIFICATION BUILDER TO PROVIDE WATERPROOF CONNECTION WITH ROOFING
O/F	OVERFLOW	TAKEN FROM TANK TO LEGAL POINT POINT OF DISCHARGE. LOCATED AT STREET IN CURB/REAR LANE/LOCATION SHOWN
B.O/F	BALCONY OVERFLOW	SEE A.406 FOR DETAIL
PC	PARAPET CAPPING	MATERIAL: 5MM STEEL FLAT PLAT COLOUR: POWDERCOAT, BLACK REFER A.406 FOR DETAIL

STORMWATER & WATER HARVESTING LEGEND

NOTE: REFER SERVICES PLAN DRAWINGS FOR SPECIFIC WATER HARNESSING + RETICULATION FUNCTIONAL INFORMATION

WSU	BELOW GROUND WATER TANK	PRODUCT: ARTLANTIS FLO-TANK, 40 X TRIPLE STACKED MODULES MATERIAL: POLYCARBONATE/STAINLESS STEEL TBC SIZE: TRIPLE MODULE 1310H X 408W X 685L TOTAL FOOTPRINT 1632 X 6350 40 X 347.8 TRIPLE MODULES LITRE: 13,912 LITRES TOTAL CAPACITY

FLOOR PLAN NOTES

1. FIGURED DIMENSIONS TO BE TAKEN IN PREFERENCE TO SCALING
2. ALL DIMENSIONS ARE CLEAR UNLESS NOTED OTHERWISE
3. ARCHITECT TO CONFIRM SETOUT ON SITE
4. FOR ARCHITRAVES & SKIRTINGS REFER FINISHES PLAN A.205-A.207
5. FOR WALL FINISHES REFER FINISHES PLAN A.205-A.207
6. READ IN CONJUNCTION WITH SPECIFICATION FOR CONSTRUCTION & WORKMANSHIP STANDARDS

STRUCTURAL ENGINEERING
- PLANS TO BE READ IN CONJUCTION WITH SPECIFICATION + STRUCTURAL ENG'S DOCUMENTATION
- STUD FRAMING IN WALLS HIGHER THAN 2.7M TO BE ALTERED AS PER THE REQUIREMENTS OUTLINED IN THE TIMBER FRAMING CODE + STRUCTURAL ENGINEERS DOCUMENTATION
- REFER STRUCTURAL ENGINEERING DRAWINGS BY 4 SITE/VISTEK

FLOOR PLAN SYMBOLS LEGEND

WALL TYPES
- A1 EXTERNAL [REFER TO A.106 +A.107]
- B1 INTERNAL [REFER TO A.106 +A.107]

STRUCTURAL MEMBER
- C3 (REFER STRUCTURAL ENGINEERING)
- CC2 CONCRETE COLUMNS (REFER CONCRETE ENGINEERING)

FLOOR FINISHES
- CONC - REFER A.205, A.206 + A.207

WINDOWS
- A01 W - REFER A.501-A.507

DOORS
- 1.01 D - REFER TO DOOR SCHEDULE

EXTERNAL BLIND
- BK - EXTERNAL MOTORISED ALUMINIUM VENETIAN BLIND (REFER A.405 FOR DETAIL + SCHEDULES FOR PRODUCT)

BALLISTRADES
- BL1 - DELETED-
- BL2 BALUSTRADE TYPE 2 - REFER TO A.408 BALUSTRADE DETAIL
- BL3/PS BALUSTRADE TYPE 3 (INC. PRIVACY SCREEN) - REFER TO A.408 BALUSTRADE DETAIL
- BL4 BALUSTRADE TYPE 4 - REFER TO A.408 BALUSTRADE DETAIL
- BL5 BALUSTRADE TYPE 5 - REFER TO A.408 BALUSTRADE DETAIL
- PS PRIVACY SCREEN (FIXED METAL PRIVACY SCREEN) - REFER TO A.408 FOR DETAIL
- G1 GATE 1 - REFER TO GATE DETAIL

JOINERY + FURNITURE
- J JOINERY UNIT - REFER TO JOINERY DRAWINGS FOR DETAILS
- J.(U) JOINERY UNIT UNDER - REFER TO JOINERY DRAWINGS FOR DETAILS
- LF LOOSE FURNITURE (BY OTHERS)

DRAINAGE
- DP DOWNPIPE
- DW BALCONY WASTE REFER DETAIL A AND DETAIL C ON A.406

GENERAL LEGEND
- 1.0 A.404 DETAIL REFERENCE CODE

CSD	CAVITY SLIDING DOOR
SD	SLIDING DOOR
DW	DISH WASHER
FR	FRIDGE
CBRD	CUPBOARD
WM	WASHING MACHINE
DR	TUMBLE DRYER
BA	HAND BASIN
TRH	TOILET ROLL HOLDER
TR	TOWEL RAIL
TRG	TROUGH
CT	COOK TOP
MC	MIRROR CABINET
WB	WASH BASIN
V	VANITY
HTR	HEATED TOWEL RAIL
HT	HAND TOWEL HOLDER
R	WARDROBE
FH	FIRE HYDRANT
D	DESK
BW	BALCONY WASTE
CL	CLEAR
S/O	SET OUT
O/S	OFFSET
C.O.S	CHECK ON SITE
SCV	SPRINKLER CONTROL VALVE

- FRAME OUT WALL RECESS
- ACCESSIBLE TURNING AREA

FIRE SERVICES
- FC FIRE CURTAIN PRODUCT TBC

DIMENSIONS ARE FOR SCOPING PURPOSES AND SHOW DESIGN INTENT

ISSUE	DATE	REVISION
E	17/12/19	FOR CONSTRUCTION
D	23/10/19	FOR CLT SHOP DRAWING
C	31/5/19	CONTRACT SET

This drawing is to be read in conjunction with the other contract documents including the Preliminaries. All work and materials are to be in accordance with the requirements of the current building regulations and all relevant statutory authorities. Contractor must verify all dimensions on site before commencing any shop drawings. Do not scale any dimensions from this drawing. Refer to Architect if any discrepancies or omissions are found.

FOR CONSTRUCTION - 17/12/19

CLIENT: H.CHARALAMBOUS

Gardiner Architects
7/252 St Georges Rd, Fitzroy North, VIC, 3068
Ph: (03) 9486 4092 E: info@paulgardiner.com.au

DWG: ROOF PLAN - LEVEL 05
PROJECT: RETAIL/RESIDENTIAL DEVELOPMENT
752 HIGH STREET, THORNBURY
DRAWN BY: AM
SCALE: 1:100 @ A1
JOB NO: 141211
A.105
DWG #
REV# E

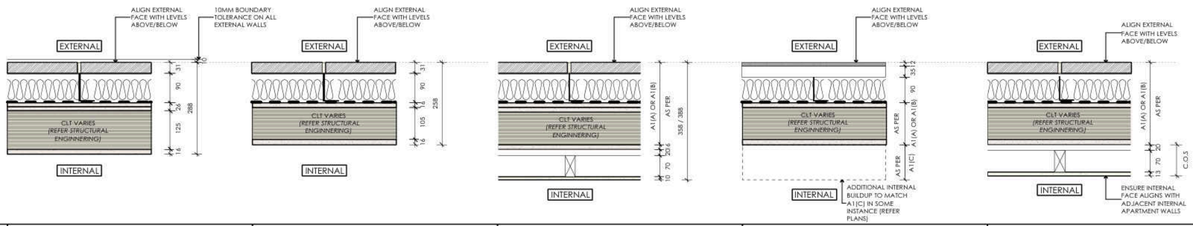

WALL TYPE CODE	A1 (A) [EXTERNAL]		A1 (B) - [EXTERNAL]		A1 (C) - [EXTERNAL]		A1 (D) - [EXTERNAL]		A1 (E) - [EXTERNAL]		A2 - [EXTERNAL]		A3 - [EXTERNAL]		A4 - [EXTERNAL]		A5 - [EXTERNAL]	
DESCRIPTION	CLT WALL LOAD BEARING (LEVEL 01+02)		CLT WALL LOAD BEARING (LEVEL 03+04)		CLT WALL LOAD BEARING (WITH CONCEALED BLIND) - WESTERN WALLS ALL LEVELS		CLT WALL LOAD BEARING (WITH VITRAPANEL CLADDING) - ALL LEVELS		CLT WALL LOAD BEARING (ADJACENT GLASS BLOCK WALL) ALL LEVELS		STAIR WELL NON-LOAD BEARING		RETAIL TO SOUTH NEIGHBOUR LOAD BEARING		GROUND FLOOR LOAD BEARING		(SERVICES CBRDS., CARSTACKER ETC. LEVEL GR) LOAD BEARING	
SYSTEM	N/A		N/A		N/A		N/A		N/A		N/A		N/A		N/A		N/A	
MIN. FIRE RATING	90/90/90		90/90/90		90/90/90		90/90/90		90/90/90		-/60/-		120/120/120		120/120/120		120/120/120	
MIN. ACOUSTIC RATING	AS PER ACOUTSIC ENG SPEC..		AS PER ACOUTSIC ENG SPEC..		AS PER ACOUTSIC ENG SPEC..		AS PER ACOUTSIC ENG SPEC..		AS PER ACOUTSIC ENG SPEC..		NA		NA		NA		NA	
OVERALL THICKNESS	288MM		258MM		358MM / 388MM		VARIES		VARIES		80mm		290mm		225mm		190mm	
WALL BUILDUP (OUTSIDE TO INSIDE)	- BRICK TILE ON METAL RAIL SYSTEM **[1]** - 20MM CAVITY - HELPING HAND ADJUSTABLE BRACKET **[31]** - ROCKWOOL INSULATION **[8]** - VAPOUR PERMEABLE SARKING **[4]** - FIRE RATED PLASTERBOARD (2x13mm) **[6]** - CLT ENGINEERED TIMBER PANEL (125mm) **[5]** - FIRE RATED PLASTERBOARD (16mm) **[6]**	SUPPLIED BY BUILDER BUILDER BUILDER BUILDER BUILDER BUILDER BUILDER CLT BUILDER	- BRICK TILE ON METAL RAIL SYSTEM **[1]** - 20MM CAVITY - HELPING HAND ADJUSTABLE BRACKET **[31]** - ROCKWOOL INSULATION **[8]** - VAPOUR PERMEABLE SARKING **[4]** - FIRE RATED PLASTERBOARD (2X16mm) **[6]** - CLT ENGINEERED TIMBER PANEL (105mm) **[5]** - FIRE RATED PLASTERBOARD (1X16mm) **[6]**	SUPPLIED BY BUILDER BUILDER BUILDER BUILDER BUILDER BUILDER BUILDER CLT BUILDER	**LEVEL 01 & 02 (AS PER A1(A))** + - CAVITY (20mm) - TIMBER STUD (70x35mm) **[7]** - PLASTERBOARD (10mm) **[9]** OR **LEVEL 03 & 04 (AS PER A1(B))** + - CAVITY (20mm) - TIMBER STUD (70x35mm) **[7]** - PLASTERBOARD (10mm) **[9]**	SUPPLIED BY BUILDER BUILDER BUILDER BUILDER BUILDER BUILDER	- VITRAPANEL **[12]** - TOPHAT (NOM. 35MM) - HELPING HAND ADJUSTABLE BRACKET **[31]** - ROCKWOOL INSULATION **[8]** - VAPOUR PERMEABLE SARKING **[4]** **LEVEL 01 & 02 (AS PER A1(A))** - FIRE RATED PLASTERBOARD (2X13mm) **[6]** - CLT ENGINEERED TIMBER PANEL (125mm) **[5]** - FIRE RATED PLASTERBOARD (16mm) **[6]** OR **LEVEL 03 & 04 (AS PER A1(B))** - FIRE RATED PLASTERBOARD (1X16mm) **[6]** - CLT ENGINEERED TIMBER PANEL (125mm) **[5]** - FIRE RATED PLASTERBOARD (16mm) **[6]** + **IN SOME INSTANCES (AS PER A1(C))** - CAVITY (20mm) - TIMBER STUD (70x35mm) **[7]** - PLASTERBOARD (10mm) **[9]**	SUPPLIED BY BUILDER BUILDER BUILDER BUILDER BUILDER BUILDER CLT BUILDER	**LEVEL 01 & 02 (AS PER A1(A))** + - CAVITY (20mm) - TIMBER STUD (TO SUIT) **[7]** - PLASTERBOARD (10mm) ALIGNED WITH ABUTTING INTERNAL WALL FACE (REFER PLANS) **[9]** OR **LEVEL 03 & 04 (AS PER A1(B))** + - CAVITY (20mm) - TIMBER STUD (TO SUIT) **[7]** - PLASTERBOARD (10mm) ALIGNED WITH ABUTTING INTERNAL WALL FACE (REFER PLANS) **[9]**	SUPPLIED BY BUILDER BUILDER BUILDER BUILDER BUILDER BUILDER	- GLASS BLOCKS (80mm) **[10]** - MORTAR GENERALLY 10mm (U.O.N) REINFORCING AS REQUIRED	SUPPLIED BY BUILDER BUILDER	- FIRE RATED PLASTERBOARD (1x13mm) **[6]** - TIMBER STUD (1 x 70mm) **[7]** - FILL STUD WALL WITH INSULATION (70mm THICK) **[40]** - AIR GAP (20 mm) - BREATHABLE SARKING - REINFORCED CONCRETE BLOCKWORK (1 x 190mm) **[11]** - RENDER + PAINT (5mm) - WHERE FINISH IS EXPOSED	SUPPLIED BY BUILDER BUILDER BUILDER BUILDER BUILDER BUILDER BUILDER	- BRICK TILE ON METAL RAIL SYSTEM **[1]** - TOP HAT (28mm) **[3]** - NON-COMUBSTIBLE BREATHABLE SARKING **[4]** - REINFORCED CONCRETE BLOCKWORK (190mm) **[11]**	SUPPLIED BY BUILDER BUILDER BUILDER BUILDER	- PAINT FINISH - REINFORCED CORE-FILLED CONCRETE BLOCKWORK **[11]** - PAINT FINISH	SUPPLIED BY BUILDER BUILDER BUILDER
NOTES	REFER WALL + FLOOR PRODUCT NOTES		REFER WALL + FLOOR PRODUCT NOTES		REFER WALL + FLOOR PRODUCT NOTES		REFER WALL + FLOOR PRODUCT NOTES		REFER WALL + FLOOR PRODUCT NOTES		REFER WALL + FLOOR PRODUCT NOTES		REFER WALL + FLOOR PRODUCT NOTES		REFER WALL + FLOOR PRODUCT NOTES		REFER WALL + FLOOR PRODUCT NOTES	

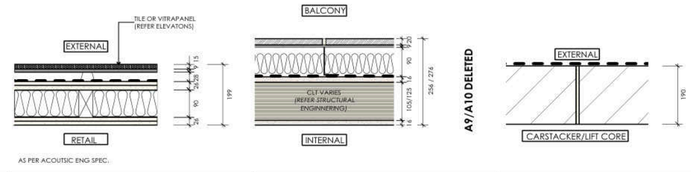

WALL TYPE CODE	A7 - [EXTERNAL]		A8 - [EXTERNAL]		A11- [EXTERNAL]		A12 (A) - [EXTERNAL]		A12 (B) - [EXTERNAL]		A13 - [EXTERNAL]		A14 - [EXTERNAL]	
DESCRIPTION	RETAIL NON-LOAD BEARING		APARTMENT BALCONIES LOAD BEARING (ALL LEVELS)		BASEMENT CARSTACKER + LIFT PIT LOAD BEARING		BALUSTRADE (LEVEL 1/2/4) LOAD BEARING		BALUSTRADE (LEVEL 3) + PARAPET (LEVEL 3) LOAD BEARING		ROOF DECK PARAPET		ROOF DECK STAIRWELL LOAD BEARING	
SYSTEM	CSR 375		N/A		N/A		N/A		N/A		N/A		N/A	
MIN. FIRE RATING	90/90/90		90/90/90		120/120/120		90/90/90		90/90/90		90/90/90		90/90/90	
MIN. ACOUSTIC RATING	AS PER ACOUTSIC ENG SPEC..		AS PER ACOUTSIC ENG SPEC..		N/A		N/A		N/A		N/A		N/A	
OVERALL THICKNESS	199mm		256MM / 276MM		190mm		VARIES		NOM. 358MM		NOM. 312MM		321MM	
WALL BUILDUP (OUTSIDE TO INSIDE)	- TILE CLADDING (NOM. 15mm) **[35]** OR - VITRAPANEL (12MM) **[12]** - FIBRE CEMENT SHEET (9mm) **[2]** - TOPHAT (28mm)**[3]** - BREATHABLE SARKING - FIRE PLASTERBOARD (2 x13mm) **[9]** - TIMBER STUD (90x45mm) **[7]** - FILL STUD WALL WITH INSULATION (90mm THICK) **[40]** - FIRE PLASTERBOARD (2 x13mm) **[9]** *** NOTE:** VITRAPANEL IN BETWEEN WINDOWS (REFER ELEVATIONS)	SUPPLIED BY BUILDER BUILDER BUILDER BUILDER BUILDER BUILDER BUILDER	- TERRACOTTA TILE DIRECT FIX TO FC SHEET **[13]** - CEMENT SHEET **[2]** - CAVITY TO SUIT - HELPING HAND ADJUSTABLE BRACKET **[31]** - ROCKWOOL INSULATION **[8]** - NON-COMUBSTIBLE BREATHABLE SARKING **[4]** - FIRE RATED PLASTERBOARD (16mm) **[6]** - CLT ENGINEERED TIMBER PANEL (125 OR 105mm) **[5]** - FIRE RATED PLASTERBOARD (16mm) **[6]**	SUPPLIED BY BUILDER BUILDER BUILDER BUILDER BUILDER BUILDER BUILDER BUILDER CLT BUILDER	- TANKING TO OUTSIDE OF WALL - REINFORCED CONCRETE BLOCKWORK (1 x 190mm) **[11]** *REFER TO STRUCTURAL ENGINEERS DRAWINGS FOR DETAILS	SUPPLIED BY BUILDER BUILDER	- BRICK TILE ON METAL RAIL SYSTEM **[1]** - 20MM CAVITY - HELPING HAND ADJUSTABLE BRACKET **[31]** - ROCKWOOL INSULATION **[8]** - FIRE RATED PLASTERBOARD (2x13mm) (LEVEL 01 + 02) **[6]** **OR** - FIRE RATED PLASTERBOARD (1x16mm) (LEVEL 03 + 04) **[6]** - CLT ENGINEERED TIMBER PANEL (125 OR 105mm) **[5]** *(REPLACED WITH LIGHT TIMBER FRAMING IN SOME INSTANCES - REFER STRUCTURAL ENGINEERING)* - FIRE RATED PLASTERBOARD (1x16mm) **[6]** - NON-COMUBSTIBLE BREATHABLE SARKING **[4]** - CEMENT SHEET **[2]** - TERRACOTTA TILE DIRECT FIX TO FC SHEET **[13]**	SUPPLIED BY BUILDER BUILDER BUILDER BUILDER BUILDER BUILDER BUILDER CLT BUILDER BUILDER BUILDER BUILDER BUILDER BUILDER	- BRICK TILE ON METAL RAIL SYSTEM **[1]** - 20MM CAVITY - HELPING HAND ADJUSTABLE BRACKET **[31]** - NON-COMUBSTIBLE BREATHABLE SARKING **[4]** - FIRE RATED PLASTERBOARD (2x13mm) **[6]** - CLT ENGINEERED TIMBER PANEL (125 OR 105mm) **[5]** - STRUCTURAL STEEL POSTS (REFER STRUCTURAL ENGINEERING FOR DETAIL) - FIRE RATED PLASTERBOARD (1x14mm) **[6]** - BATTENING TO SUIT - NON-COMUBSTIBLE BREATHABLE SARKING **[4]** - CEMENT SHEET **[2]** - BRICK TILE DIRECT FIX TO FC SHEET **[1]**	SUPPLIED BY BUILDER BUILDER BUILDER BUILDER BUILDER BUILDER BUILDER CLT BUILDER BUILDER BUILDER BUILDER BUILDER BUILDER	- BRICK TILE ON METAL RAIL SYSTEM **[1]** - 20MM CAVITY - HELPING HAND ADJUSTABLE BRACKET **[31]** - ROCKWOOL INSULATION **[8]** - NON-COMUBSTIBLE BREATHABLE SARKING **[4]** - FIRE RATED PLASTERBOARD (1x16mm) **[6]** - CLT ENGINEERED TIMBER PANEL (125 OR 105mm) **[5]** - FIRE RATED PLASTERBOARD (1x16mm) **[6]** - NON-COMUBSTIBLE BREATHABLE SARKING **[4]** - FIBRE CEMENT SHEET (9mm) **[2]**	SUPPLIED BY BUILDER BUILDER BUILDER BUILDER BUILDER BUILDER BUILDER CLT BUILDER BUILDER BUILDER BUILDER BUILDER BUILDER	- TIMBER LINING BOARDS **[42]** - CEMENT SHEET **[2]** - FRAMED OUT (NOM. METAL STUDS) TO SUIT INSULATION - ROCKWOOL INSULATION **[8]** - NON-COMUBSTIBLE BREATHABLE SARKING **[4]** - FIRE RATED PLASTERBOARD (1x16mm) **[6]** - CLT ENGINEERED TIMBER PANEL (125 OR 105mm) **[5]** - FIRE RATED PLASTERBOARD (1x16mm) **[6]** - PLYWOOD FINISH (REFER SCHEDULES)	SUPPLIED BY BUILDER BUILDER BUILDER BUILDER BUILDER BUILDER BUILDER CLT BUILDER BUILDER BUILDER
NOTES	REFER WALL + FLOOR PRODUCT NOTES		REFER WALL + FLOOR PRODUCT NOTES		REFER WALL + FLOOR PRODUCT NOTES		REFER WALL + FLOOR PRODUCT NOTES		REFER WALL + FLOOR PRODUCT NOTES		REFER WALL + FLOOR PRODUCT NOTES		REFER WALL + FLOOR PRODUCT NOTES	

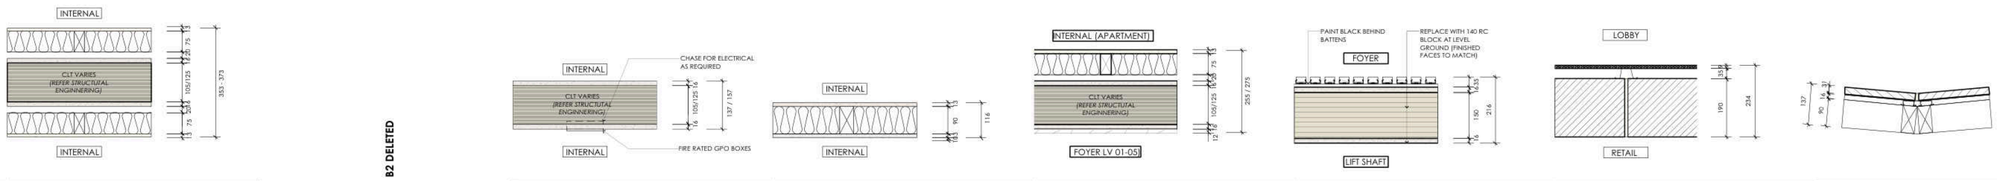

WALL TYPE CODE	B1 - [INTERNAL]		B3 - [INTERNAL]		B4 - [INTERNAL]		B5 - [INTERNAL]		B6 - [INTERNAL]		B7 - [INTERNAL]		B8 - [INTERNAL]	
DESCRIPTION	CLT PARTY WALL - INTERTENANCY LOAD BEARING		CLT GENERAL APARTMENT WALL LOAD BEARING		INTERNAL APARTMENT WALL (FRAMING) NON-LOAD BEARING		CLT CORRIDOR WALL LOAD BEARING		LIFT SHAFT WALL (CONCRETE UP TO LV 01, CLT ABOVE) LOAD BEARING		RETAIL AND FOYER DIVIDING WALL LOAD-BEARING		CURVED WALL TO STAIR (LEVEL GR) NON-LOAD BEARING	
SYSTEM	W07-03		N/A		N/A		N/A		N/A		N/A		N/A	
MIN. FIRE RATING	90/90/90		90/90/90		-/60/60		90/90/90		90/90/90		120/120/120		NIL	
MIN. ACOUSTIC RATING	Rw + Ctr > 50		N/A		N/A		Rw > 50		N/A		N/A		N/A	
OVERALL THICKNESS	353mm OR 373mm		137mm OR 157mm		110mm		255mm OR 275mm		216mm		234mm		137mm	
WALL BUILDUP (INSIDE TO OUT)	- PLASTERBOARD (13mm) **[9]** - TIMBER STUD (70x35mm) **[7]** - FILL STUD WALL WITH GLASSWOOL INSULATION(75mm)**[40]** - AIR GAP (20 mm) - FIRE RATED PLASTERBOARD (16mm) **[6]** - CLT ENGINEERED TIMBER PANEL (105 OR 125mm) **[5]** - FIRE RATED PLASTERBOARD (16mm) **[6]** - AIR GAP (20 mm) - TIMBER STUD (70x35mm) **[7]** - FILL STUD WALL WITH GLASSWOOL INSULATION(75mm)**[40]** - PLASTERBOARD (10mm) **[9]**	SUPPLIED BY BUILDER BUILDER BUILDER BUILDER CLT BUILDER BUILDER BUILDER BUILDER	- FIRE RATED PLASTERBOARD (16mm) **[6]** - CLT ENGINEERED TIMBER PANEL (105mm or 125mm) **[5]** - FIRE RATED PLASTERBOARD (16mm) **[6]**	SUPPLIED BY BUILDER CLT BUILDER	- FIRE RATED PLASTERBOARD (13mm) **[6]** - TIMBER STUD (90x45mm) **[7]** - FILL STUD WALL WITH GLASSWOOL INSULATION (90mm) **[40]** - FIRE RATED PLASTERBOARD (13mm) **[6]**	SUPPLIED BY BUILDER CLT BUILDER BUILDER	- PLASTERBOARD (10mm) **[9]** - TIMBER STUD (90x45mm) **[7]** - FILL STUD WALL WITH GLASSWOOL NSULATION (75mm) **[40]** - AIR GAP (20 mm) - FIRE RATED PLASTERBOARD (16mm) **[6]** - CLT ENGINEERED TIMBER PANEL (105mm OR 125mm) **[5]** - FIRE RATED PLASTERBOARD (16mm) **[6]** - PLYWOOD FINISH (REFER SCHEDULES)	SUPPLIED BY BUILDER BUILDER BUILDER BUILDER CLT BUILDER BUILDER	- "CONCEPT CLICK" TIMBER BATTEN (19mm x 32mm) ON PROPRIETARY TRACK, SPECIES AND SPACING TBC - FIRE RATED PLASTERBOARD (1 x 16mm) **[6]** - CLT ENGINEERED TIMBER PANEL (150mm) **[5]** - FIRE RATED PLASTERBOARD (1 x 16mm) **[6]** *SUBSTITUTE CLT WITH REINFORCED CONCRETE BLOCKWORK (140mm)**[11]** UP TO LEVEL 01 FLOOR LEVEL. FINISHED FACE TO MATCH.	SUPPLIED BY BUILDER: BUILDER: CLT BUILDER	- VITRAPANEL (9MM) **[12]** - TOPHAT (35MM) - REINFORCED CONCRETE BLOCKWORK (1 x 190mm) **[11]**	SUPPLIED BY BUILDER BUILDER BUILDER	- BRICK TILE ON METAL RAIL SYSTEM **[1]** - TOPHAT (28mm)**[3]** - TIMBER STUD (90x45mm) **[7]**	SUPPLIED BY BUILDER BUILDER BUILDER
NOTES	REFER WALL + FLOOR PRODUCT NOTES		REFER WALL + FLOOR PRODUCT NOTES		SUBSTITUTE INTERNAL SIDE OF FIRE RATED PLASTERBOARD FOR VILLABOARD AND TILES IN GROUND FLOOR BATHROOMS REFER WALL + FLOOR PRODUCT NOTES		REFER WALL + FLOOR PRODUCT NOTES		REFER WALL + FLOOR PRODUCT NOTES		REFER WALL + FLOOR PRODUCT NOTES		REFER WALL + FLOOR PRODUCT NOTES	

WALL + FLOOR PRODUCT NOTES

1. **BRICK CLADDING (BUILDING FACADE)**
   PRODUCT: PGH AVANTE RAIL SYSTEM
   BRICK: MORADA, OR SIMILAR TBC
   SIZE: TBC
   COLOUR: TBC
   CONTACT: ANDREW WALLACE 0401 897 190
2. **CEMENT SHEET**
   NOTES: SUBSTRATE FOR VARIOUS FINISHES
   PRODUCT: EXTERIOR GRADE SUITABLE AS WATERPROOF EXTERNAL TILE UNDERLAY
3. **TOPHAT**
   PRODUCT: PROPRIETARY 28mm FOLDED METAL EQUIVALENT TO (RONDO OR SIMILAR APPROVED)
4. **SARKING**
   PRODUCT: ENVIROSEAL PROCTORWRAP COMMERCIAL WALL (CW)
   SUPPLIER: PROCTOR GROUP
   CONTACT: (03) 9369 4043
5. **ENGINEERED TIMBER PANEL**
   PRODUCT: CROSS LAMINATED TIMBER (CLT) FLOOR + WALL PANELS
   CONTACT: XLAM (0458 333 886)
6. **FIRE RATED PLASTERBOARD**
   PRODUCT: BORAL FIRESTOP
   SIZE: 13 OR 16mm THICK
7. **TIMBER STUD WALLS**
   PRODUCT: - 70x35mm + 90x45mm PINE STUDS @ 450MM CTRS
   - 70x35mm + 90x45mm TOP + BOTTOM PLATES + NOGGINGS
   CONTACT: XLAM (0458 333 886)
8. **INSULATION (EXTERNAL RAINSCREEN WALL + BALCONIES)**
   PRODUCT: DCTECH ROCKWOOL 80mm THICK, R2.1 INSULATION, SLIT INSULATION TO ALLOW THE NVELOPE BRACKET PIERCE THROUGH IN RAINSCREEN INSTALLATION
   SUPPLIER: DCTECH
   CONTACT: 0413 624 345
9. **PLASTERBOARD LINING**
   STANDARD 10 + 13mm PLASTERBOARD
10. **GLASS BLOCKS**
    PRODUCT: LA ROCHERE RANGE 'JAVA' + 'TRANSPARENT' 190x190x80mm (REFER A.409 FOR BREAKUP)
    SUPPLY + INSTALL: GLASS BLOCK SHOP
    CONTACT: (03) 9720 4099
11. **REINFORCED CONCRETE BLOCK WORK**
    - REFER STRUCTURAL ENGINEERS DOCUMENTS FOR DETAILS
12. **PRE-FINISHED CEMENT SHEET**
    PRODUCT: VITRAPANEL (OR SIMILAR APPROVED) PREFINISHED CEMENT SHEET
    COLOUR: BLACK (COLOUR TBC)
13. **TERRACOTTA TILE**
    - REFER SCHEDULE FOR PRODUCT
    THICKNESS: 15MM SOFFITS AND WALLS / 50MM BALCONIES
    INSTALLATION: DIRECT FIX TO SOFFITS + WALLS / ON PROPRIETARY DECK STRUCTURE FOR BALCONIES
14. **ACOUSTIC RUBBER UNDERLAY**
    PRODUCT: EMBLETON IMPACTAMAT
    THICKNESS: 10MM
15. **TIMBER DECKING**
    - REFER SCHEDULE FOR PRODUCT
16. **PROPRIETARY DECK SUBSTRUCTURE**
    PRODUCT: OUTDURE 'QWICKBUILD' PROPRIETARY DECK FRAME + SUPPORT SYSTEM
    CONTACT: ph (02) 9098 8250
17. **WATERPROOF MEMBRANE**
    PRODUCT: NEPTUNE COATINGS WETSUIT FLUID APPLIED MEMBRANE SUPPLY + INSTALL
18. **CERAMIC WALL TILE (INTERNAL WET AREAS)**
    - REFER TO SCHEDULE OF TILES FOR PRODUCT
19. **TILE UNDERLAY(INTERNAL WET AREAS)**
    PRODUCT: 6mm VILLABOARD FROM JAMES HARDIE
20. **CERAMIC WALL TILE (INTERNAL)**
    - REFER SCHEDULE FOR PRODUCT
21. **CERAMIC FLOOR TILE (INTERNAL)**
    - REFER SCHEDULE FOR PRODUCT
22. **CONCRETE SLAB**
    - REFER STRUCTURAL ENGINEERS DOCUMENTS FOR DETAILS
23. **PEBBLE ROOF**
    PRODUCT: RECYCLED BRICK
24. **GEOTEXTILE MEMBRANE**
    PRODUCT: REFER PEBBLE ROOF SUBCONTRACTOR'S SPEC.
25. **DRAINAGE CELL**
    PRODUCT: REFER PEBBLE ROOF SUBCONTRACTOR'S SPEC. (ATLANTIS FLO-CELL 20 OR SIMILAR)
26. **PROTECTION LAYER**
    PRODUCT: REFER PEBBLE ROOF SUBCONTRACTOR'S SPEC.
27. **SCREED (EXTERNAL TO ACHIEVE FALL)**
    PRODUCT: TBC (ARDEX OR SIMILAR APPROVED)
28. **FLOORING SUBSTRATE**
    PRODUCT: KNAUF BRIO 23 (23MM THICK)
29. **INSULATION (CEILING)**
    PRODUCT: GLASSWOOL BATT INSULATION (MIN.14kg/m3) MIN. 75MM THICK
30. **VIBRATION ISOLATORS**
    PRODUCT: EMBELTON UB CEILING BRACKET WITH RHDE RUBBER ELEMENT
    SUPPLIER: EMBELTON
31. **BRICK TILE CLADDING SUPPORTS**
    PRODUCT: HELPING HAND BRACKET NH2 SYSTEM
    SUPPLIER: NVELOPE
32. **ACOUSTIC FLOOR INSULATION**
    PRODUCT: GLASSWOOL QUIETEL 130KG/M³ (13MM THICK)
    SUPPLIER: BRADFORD
33. **APARTMENT CEILING**
    PRODUCT: MDF WITH HOOP PINE VENEER ROTARY CUT BACKING DBG (26MM THICK)
    SUPPLIER: TIMBERWOOD PANELS
    CONTACT: 0436 654 968
34. **SCREED (INTERNAL TO ACHIEVE FALL)**
    PRODUCT: TBC (ARDEX OR SIMILAR APPROVED)
35. **TILE CLADDING (EXTERIOR)**
    - REFER SCHEDULE OF EXTERNAL FINISHES
36. **CLT FLOOR SLAB MEMBRANE**
    PRODUCT: PROCTOR WRAPTITE SA SELF ADHESIVE FACTORY APPLIED TO CLT
    SUPPLIER: PROCTOR GROUP
    CONTACT: (03) 9369 4043
37. **METAL GRATE**
    PRODUCT: STANDARD SURFACE PROFILE
    SUPPLIER: WEDLOK
    NOTE: CONFIRM LOADS OF SERVICES PLANT
38. **STEEL SUB FRAME ON PAD FOOTINGS**
    - 1 x 150mm
    PRODUCT: TBC
39. **ENGINEERED TIMBER FLOORBOARDS**
    - REFER SCHEDULE FOR PRODUCT
40. **INSULATION (INTERNAL WALLS)**
    FILL WALL CAVITY WITH GLASSWOOL BATT INSULATION
    PRODUCT : GLASSWOOL BATT INSULATION (MIN. 14kg/m3)
41. **ROOF DECK SCREED SUBSTRATE**
    18MM MARINE PLY
42. **EXTERNAL TIMBER LINING**
    TIMBER LINING BOARDS (REFER SCHEDULES FOR PRODUCT)
43. **DIMPLED RUBBER UNDERLAY**
    FOR ROOF DECK
    PRODUCT: REGUPOL 6010 8/4MM DIMPLED

FOR CONSTRUCTION - 17/12/19

ISSUE	DATE	REVISION
E	17/12/19	FOR CONSTRUCTION
D	23/10/19	FOR CLT SHOP DRAWING

This drawing is to be read in conjunction with the other architectural documents including the project specification and all relevant consultant's drawings. Do not scale this drawing. Contractor is to check all dimensions on site. Do not scale off drawing. Any discrepancies are to be brought to the attention of the Architect/Superintendent Architect for clarification/decision in writing.

CLIENT: H.CHARALAMBOUS

Gardiner Architects
7/252 St Georges Rd, Fitzroy North, VIC, 3068
Ph: (03) 9486 4092 E: info@paulgardiner.com.au

DWG: WALL/FLOOR/ROOF TYPE SCHEDULE
PROJECT: RETAIL/RESIDENTIAL DEVELOPMENT
752 HIGH STREET, THORNBURY
DRAWN BY: AM
SCALE: 1:10 @ A1
JOB NO: 141211
DWG #: A.106
REV#: E

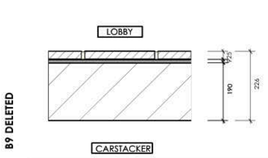

B9 DELETED

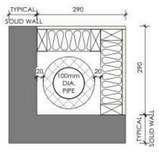

B11 DELETED

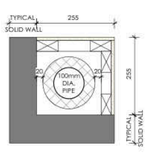

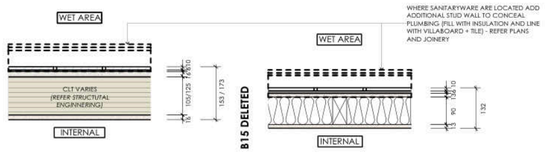

B15 DELETED

WALL TYPE CODE	B10 - [INTERNAL]		B12 - [INTERNAL]		B13 - [INTERNAL]		B14 - [INTERNAL]		B16 - [INTERNAL]	
DESCRIPTION	LOBBY TO CARSTACKER LOAD BEARING		RISER IN HABITABLE ROOM		RISER IN NON-HABITABLE ROOM		CLT (HABITABLE ROOM - WET AREA) LOAD-BEARING		FRAMING (HABITABLE ROOM - WET AREA) NON-LOAD-BEARING	
SYSTEM	N/A		TBC		TBC		TBC		N/A	
FIRE RATING	120/120/120		-/60/60		-/60/60		90/60/60		-/60/60	
ACOUSTIC RATING	N/A		Rw + Ctr > 40		Rw + Ctr > 25		N/A		N/A	
OVERALL THICKNESS	226mm		TBC		TBC		153mm OR 173mm		132mm	
WALL BUILDUP (INSIDE TO OUT)	- BRICK TILE (25mm) DIRECT FIX (NO METAL RAIL) **[1]** - CEMENT SHEET (9mm) **[2]** - REINFORCED CONCRETE BLOCKWORK (1 x 190mm) **[11]** - PAINT FINISH TO CARSTACKER FACE	SUPPLIED BY BUILDER BUILDER BUILDER	- PLASTERBOARD (10mm) **[9]** - TIMBER STUD (70x35mm) **[7]** - FILL STUD WALL WITH GLASSWOOL INSULATION (75mm) **[40]** - 20mm AIR GAP - ACOUSTIC LAGGING AROUND PIPE AS REQUIRED	SUPPLIED BY BUILDER BUILDER BUILDER BUILDER BUILDER	- PLASTERBOARD (10mm) **[9]** - TIMBER STUD ON SIDE (70x35mm) **[7]** - 20mm AIR GAP - ACOUSTIC LAGGING AROUND PIPE AS REQUIRED	SUPPLIED BY BUILDER BUILDER BUILDER:	- TILE LINING (NOM.10MM) **[19]** - VILLABOARD LINING (6mm) **[20]** - FIRE RATED PLASTERBOARD (16mm) **[6]** - CLT ENGINEERED TIMBER PANEL (105mm OR 125mm) **[5]** - FIRE RATED PLASTERBOARD (16mm) **[6]**	SUPPLIED BY BUILDER BUILDER BUILDER CLT BUILDER	- TILE LINING (NOM.10MM) **[19]** - VILLABOARD LINING (6mm) **[20]** - FIRE RATED PLASTERBOARD (13mm) **[6]** - TIMBER STUD (90x45mm) **[7]** - FILL STUD WALL WITH INSULATION (70mm THICK) **[40]** - FIRE RATED PLASTERBOARD (13mm) **[6]**	SUPPLIED BY BUILDER BUILDER LVL BUILDER BUILDER
NOTES	REFER WALL + FLOOR PRODUCT NOTES		REFER WALL + FLOOR PRODUCT NOTES FIRE COLLARS REQUIRED AT FLOORS BELOW + ABOVE		REFER WALL + FLOOR PRODUCT NOTES FIRE COLLARS REQUIRED AT FLOORS BELOW + ABOVE		REFER WALL + FLOOR PRODUCT NOTES		- STUD WALLS TO CONTINUE UP TO UNDERSIDE OF CLT FLOOR SLAB ABOVE - BATHROOM SIDE LAYER OF VILLABOARD LINING CAULKED AGAINST CLT FLOOR SLAB REFER WALL + FLOOR PRODUCT NOTES	

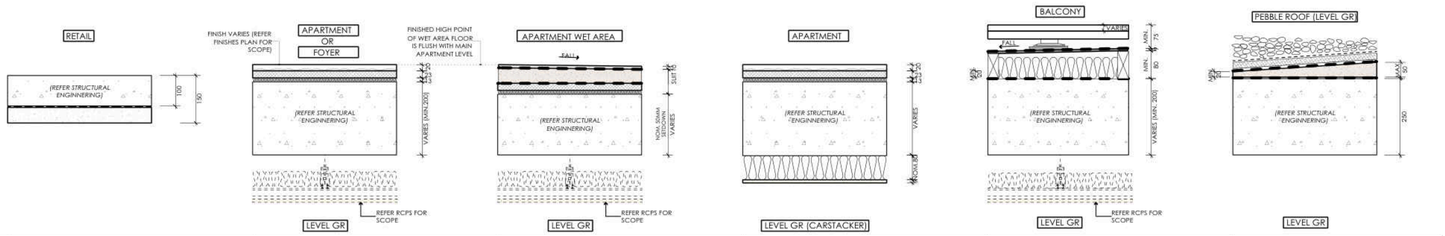

FLOOR/ROOF TYPE CODE	C1	C2 (A)	C2 (B)	C3	C4	C5
DESCRIPTION	CONCRETE - LEVEL GR (SLAB ON GROUND)	CONCRETE - LEVEL 01 (TYPICAL FLOOR)	CONCRETE - LEVEL 01 WET AREA (TYPICAL FLOOR)	CONCRETE - LEVEL 01 (FLOOR ABOVE CARSTACKER)	CONCRETE - LEVEL 01 (TYPICAL BALCONY)	CONCRETE - LEVEL GR (PEBBLE ROOF OVER STORE)
SYSTEM	N/A	N/A	N/A	N/A	N/A	N/A
FIRE RATING	N/A	120/120/120	120/120/120	120/120/120	120/120/120	120/120/120
ACOUSTIC RATING	N/A	Rw +Ctr > 50 (AIRBORNE) Ln,w <62 (IMPACT)	Rw +Ctr > 50 (AIRBORNE) Ln,w <62 (IMPACT)	Rw +Ctr > 50 (AIRBORNE) Ln,w <62 (IMPACT)	Rw +Ctr > 50 (AIRBORNE) Ln,w <62 (IMPACT)	N/A
OVERALL THICKNESS	150mm	VARIES	VARIES	VARIES	VARIES	VARIES
FLOOR BUILDUP (TOP TO BOTTOM)	- CONCRETE RAFT SLAB (REFER ENGINEERING FOR SPECIFICATION) - MEMBRANE TO ENGINEERS DETAIL - COMPACTED SAND BED (1 x 50mm) *ALL TO ENGINEERS DETAIL SUPPLIED BY BUILDER BUILDER BUILDER BUILDER	- ENGINEERED TIMBER FLOOR BOARD **[39]** (REPLACE WITH TILES IN WC'S+UNDER LAUNDRY WASHING MACHINES) - POST TENSIONED CONCRETE SLAB (REFER ENGINEERING FOR SPECIFICATION) - SUSPENDED CEILING WITH INSULATION AS REQUIRED (REFER RCP'S FOR SCOPE OF FINISH) SUPPLIED BY BUILDER BUILDER BUILDER BUILDER	- TILE FINISH **[21]** - WATERPROOFING MEMBRANE - SCREED TO FALL **[34]** - WATERPROOFING MEMBRANE - POST TENSIONED CONCRETE SLAB (WITH SETDOWN) (REFER ENGINEERING FOR SPECIFICATION) - SUSPENDED CEILING WITH INSULATION AS REQUIRED (REFER RCP'S FOR SCOPE OF FINISH) SUPPLIED BY BUILDER BUILDER BUILDER BUILDER BUILDER BUILDER BUILDER	- ENGINEERED TIMBER FLOOR BOARD **[39]** (REPLACE WITH TILES + WATERPROOF MEMBRANE TO FALL UNDER LAUNDRY WASHING MACHINES) - KNAUF BRIO 23 BONDED TO FLOOR BOARD **[28]** - HIGH DENSITY GLASSWOOL **[32]** - POST TENSIONED CONCRETE SLAB (REFER ENGINEERING FOR SPECIFICATION) - HIGH DENSITY GLASSWOOL **[8]** - VILLABOARD SHEET (FLUSH JOINTED + PAINTED) SUPPLIED BY BUILDER BUILDER BUILDER BUILDER BUILDER BUILDER	- TERRACOTTA TILE - DECK SUBSTRUCTURE ON PADS (VARIES) **[16]** - ACOUSTIC RUBBER UNDERLAY BENEATH DECKING PADS **[34]** - WATERPROOF MEMBRANE **[17]** - SCREED TO FALL (VARIES) **[27]** - WATERPROOF MEMBRANE **[17]** - POST TENSIONED CONCRETE SLAB (REFER ENGINEERING FOR SPECIFICATION) - SUSPENDED CEILING WITH INSULATION AS REQUIRED (REFER RCP'S FOR SCOPE OF FINISH) SUPPLIED BY BUILDER BUILDER BUILDER BUILDER BUILDER BUILDER BUILDER	- PEBBLES (NOM.50mm) **[23]** - GEOTEXTILE MEMBRANE **[24]** - DRAIN CELL (20mm) **[25]** - WATERPROOF MEMBRANE **[17]** - CONCRETE SCREED TO FALL (VARIES)**[27]** - WATERPROOF MEMBRANE **[17]** - POST TENSIONED CONCRETE SLAB (REFER ENGINEERING FOR SPECIFICATION) SUPPLIED BY BUILDER BUILDER BUILDER BUILDER BUILDER BUILDER BUILDER
NOTES		FINISH VARIES IN FOYER (REFER FINISHES PLAN A.206 + A.207 FOR SCOPE				

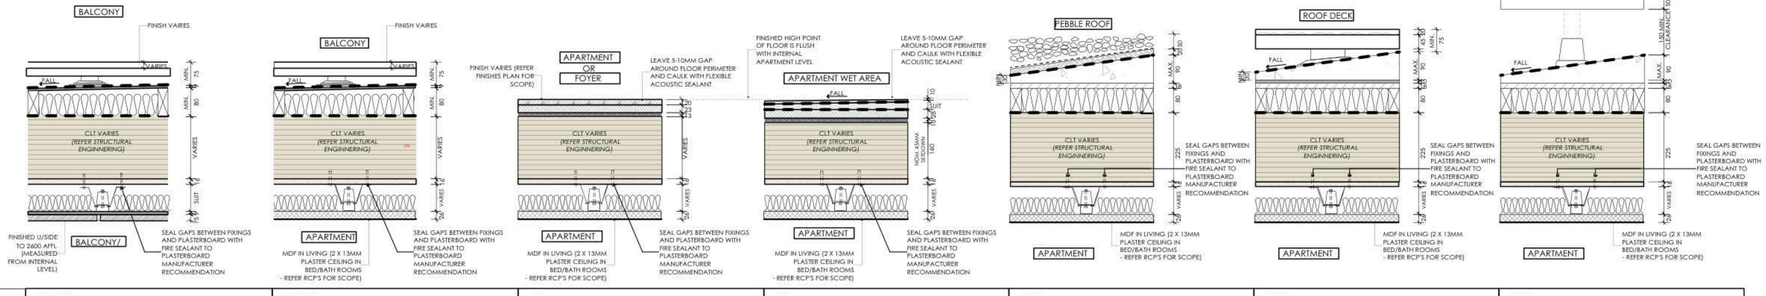

FLOOR/ROOF TYPE CODE	C6 (A)	C6 (B)	C7	C8	C10	C12	C13
DESCRIPTION	CLT- LEVEL 02/03/04 (TYPICAL BALCONY OVER BALCONY)	CLT - LEVEL 02/03/04 (TYPICAL BALCONY OVER APARTMENT)	CLT - LEVEL 02/03/04 (TYPICAL APARTMENT FLOOR)	CLT - LEVEL 02/03/04 (TYPICAL WET AREA)	CLT - LEVEL 2/LEVEL 4 (ROOF)	CLT - LEVEL 5 (ROOF DECK)	CLT - LEVEL 05 (SERVICES DECK FLOOR)
SYSTEM	N/A	N/A	N/A	N/A	N/A	N/A	N/A
FIRE RATING	90/90/90	90/90/90	90/90/90	90/90/90	90/90/90	90/90/90	90/90/90
ACOUSTIC RATING	Rw +Ctr > 50 (AIRBORNE) Ln,w <62 (IMPACT)	Rw +Ctr > 50 (AIRBORNE) Ln,w <62 (IMPACT)	Rw +Ctr > 50 (AIRBORNE) Ln,w <62 (IMPACT)	Rw +Ctr > 50 (AIRBORNE) Ln,w <62 (IMPACT)	N/A	Rw +Ctr > 50 (AIRBORNE) Ln,w <62 (IMPACT)	N/A
OVERALL THICKNESS	VARIES	VARIES	VARIES	VARIES	VARIES	VARIES	VARIES
FLOOR BUILDUP (TOP TO BOTTOM)	- TIMBER DECKING **[15]** OR - TILE **[13]** - DECK SUBSTRUCTURE ON PADS (VARIES) **[16]** - ACOUSTIC RUBBER UNDERLAY BENEATH DECK PADS 10MM **[14]** - WATERPROOF MEMBRANE **[17]** - CEMENT SHEET ON BATTENS TO FALL **[2]** - ROCKWOOL INSULATION **[8]** - CLT MEMBRANE **[36]** - CLT ENGINEERED TIMBER PANEL (NOM. 205mm) **[5]** - FIRE RATED PLASTERBOARD (1x16mm) **[9]** - CAVITY TO SUIT FILLED WITH min. 75mm INSULATION **[29]** - VIBRATION ISOLATORS **[30]** - CEILING CHANNEL (RONDO OR SIMILAR) - CEMENT SHEET **[2]** - TERRACOTTA TILE DIRECT FIX TO FC SHEET **[13]** SUPPLIED BY BUILDER BUILDER BUILDER BUILDER BUILDER BUILDER BUILDER

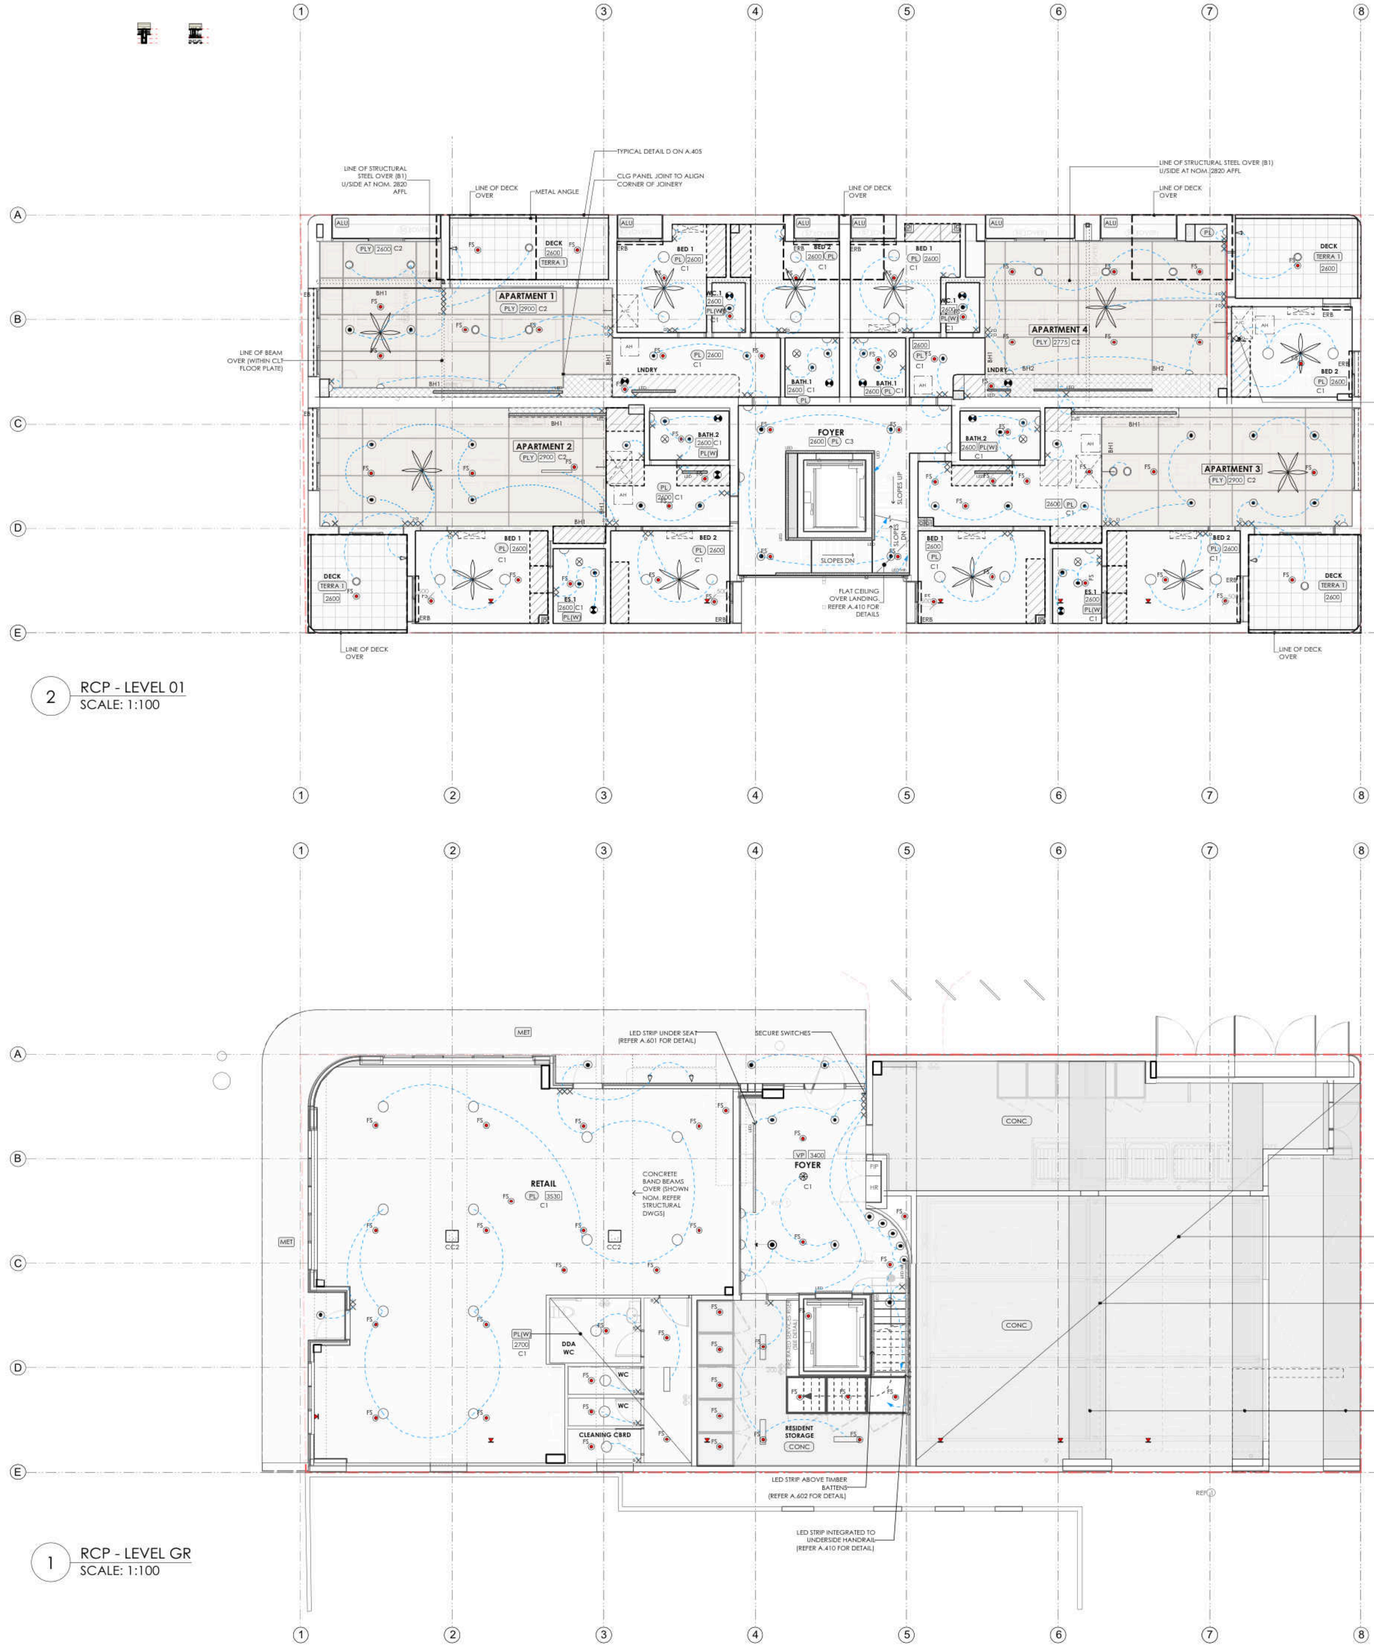

2 RCP - LEVEL 01
SCALE: 1:100

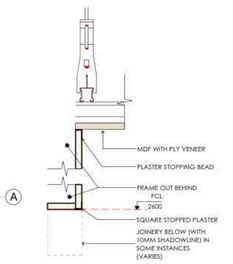

A BH1 - TYPICAL DETAIL
Scale: 1:5

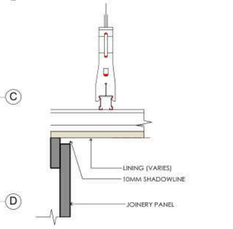

B JOINERY/CLG SHADOW LINE - TYPICAL DETAIL
Scale: 1:5

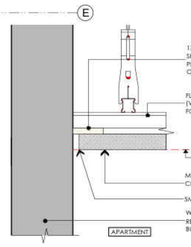

C TYPICAL CORNICE C2 DETAIL (APARTMENT)
Scale: 1:5

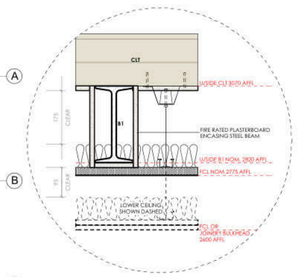

E CLG DETAIL - BEAM B1
SCALE: 1:10

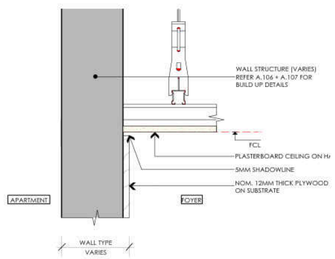

D TYPICAL CORNICE C3 DETAIL (FOYER)
Scale: 1:5

1 RCP - LEVEL GR
SCALE: 1:100

CEILING NOTES

1. READ IN CONJUNCTION WITH SPECIFICATION FOR QUALITY AND WORKMANSHIP
2. **BATTENING**
   ALL PLASTER CEILINGS TO BE BATTENED WITH ADJUSTABLE RONDO FURRING CHANNELS TO ALLOW FLAT + STRAIGHT PLASTER
3. **PREPARATION**
   ALL WALL FRAMING TO BE TRIMMED PACKED & GENERALLY READY FOR PLASTER AND/OR PLYWOOD
4. **PLASTERWORK**

LEVEL OF FINISH
- LEVEL 4 FINISH TO AS 2589:2007 (GENERALLY THROUGHOUT U.O.N.) STANDARD LEVEL OF FINISH FOR STOPPED PLASTERBOARD
- LEVEL 5 FINISH TO AS 2589:2007 HIGH LEVEL OF FINISH FOR GLANCING LIGHT & SEMI GLOSS PAINTS

PRODUCT:
USE BORAL "ENVIRO" RANGE OR SIMILAR APPROVED

GENERAL
- 2600 FINISHED HEIGHT ABOVE FINISHED FLOOR LEVEL (FFL)
- PRODUCTS TO BE ORDERED AS SPECIFIED UNLESS OTHERWISE APPROVED.
- JOINERY BELOW, FULL HEIGHT
- JOINERY BELOW, UP TO BULKHEAD

CEILING LEGEND

LININGS
- PL — PLASTERBOARD 13MM THICK FLUSH JOINTED FOR PAINT FINISH
- PLW — WATERPROOF PLASTERBOARD 13MM FLUSH JOINTED SOFFIT LINING, PAINTED FINISH - BORAL WET AREA BOARD OR SIMILAR APPROVED
- PLY — 26mm THICK PRODUCT: MDF WITH HOOP PINE VENEER (REFER WALL+FLOOR BUILDUP A.107, DETAIL 33 FOR DETAILS)
- CONC — EXPOSED CONCRETE SLAB OVER BONDEK TRAY (NO FINISH)
- MET — FLAT COLORBOND SHEET MATERIAL: COLOURBOND STEEL ADHERED TO 18MM MARINE PLY SUBSTRATE COLOUR: BLACK (TBC)
- TERRA 1 — TERRACOTTA SOFFIT TILE ADHESIVE FIX REFER SCHEDULES FOR PRODUCT AND A.106/A.107 FOR DETAIL
- PM — PERFORATED METAL TO UNDERSIDE OF AWNING REFER A.407 FOR DETAIL
- ALU — FABRICATED PRE-FINISHED ALUMINIUM REVEAL COLOUR: DARK GREY (TBC)

CORNICES
- TYPE 1 CORNICE - SQUARE SET
- C1 TYPE 2 CORNICE - 10MM SHADOWLINE (REFER TYPICAL DETAIL C/A.201)
- C2 TYPE 2 CORNICE - 5MM SHADOWLINE (REFER TYPICAL DETAIL D/A.201)

MISC.
- AH — ACCESS HATCH - FLUSH CONCEALED HATCH PAINTED FINISH. U.O.N. SIZE: NOM. 600 x 600

MECHANICAL
- AIR CONDITIONING DIFUSER FLUSH TO CEILING. FINISH: SELECTED POWDERCOAT COLOUR
- ABOVE CEILING CONCEALED SPLIT A/C UNIT WITH ACCESS HATCH. ARROW INDICATES GRILLE DIRECTION SIZE: NOM. 1050 x 850
- WALL MOUNTED A/C UNIT

SERVICES
- FIRE SPRINKLER BRANCH
- FIRE SPRINKLER NEW
- FS — FIRE SPRINKLER SIDEWALL

STRUCTURAL STEEL
- STRUCTURAL STEEL - CONCEALED IN CEILING (REFER STRUCTURAL PLANS FOR DETAIL)

INTERNAL WINDOW FURNISHING SCHEDULE
NOTES:
- REFER PROVISIONAL SUMM
- READ IN CONJUNCTION WITH WINDOW SCHEDULE

- EB — EXTERNAL MOTORIZED RECESSED DROP DOWN ALUMINIUM VENETIAN BLIND (REFER SCHEDULES FOR PRODUCT) REFER DETAIL B/A.405
- ERB — EXPOSED ROLLER BLIND ON SASH REFER DETAIL A/A.405
- CRB — CONCEALED ROLLER BLIND REFER DETAIL A/A.405

LIGHTING NOTES

1. READ IN CONJUNCTION WITH SPECIFICATION.
2. ARTIFICIAL LIGHT TO COMPLY WITH AS1680
3. LIGHTING LAYOUT TBC BY ARCHITECT ON SITE
4. PLY CEILING LAYOUT TBC BY ARCHITECT ON SITE
5. EUROPEAN LAUNDRIES WITH FOLDING DOORS TO HAVE SWITCHES INSIDE CAVITY END PANELS AT NOM. 1500MM AFFL - REFER JOINERY DWGS FOR DETAIL
6. **LIGHT FITTINGS**
   INSTALLATION: BY BUILDER
   SELECTIONS: REFER SCHEDULE OF LIGHT FITTINGS IN "SCHEDULES" + PC SUMS FOR SUPPLY ONLY ALLOWANCE
   SHROUDS: ALL RECESSED DOWNLIGHTS ARE REQUIRED TO HAVE SHROUDS INSTALLED TO MANUFACTURERS SPECIFICATIONS PRODUCT: EXFOLIATORS AUSTRALIA FIRE RATED DOWN LIGHT COVERS SIZED AS APPROPRIATE AND INSTALLED AS PER MANUFACTURER'S SPEC
7. **WIRING**
   - ALL EXISTING LIGHTING WIRING TO BE RETAINED/REPLACED WITH NEW TO LOCATIONS AS SHOWN ON PLANS
8. **ENERGY RATING**
   - LED LIGHT FITTINGS TO BE INSTALLED GENERALLY
   - LIGHT FITTINGS TO COMPLY WITH BCA 6 STAR ENERGY RATING REQUIREMENT
   - TOTAL MAXIMUM ILLUMINATION POWER SHOULD NOT EXCEED:
     - 5 WATTS/SQM FOR INTERNAL AREAS
     - 4 WATTS/SQM FOR EXTERNAL AREAS
     - 3 WATTS/SQM FOR GARAGES
9. **SWITCHES & PRODUCTS**
   - PRODUCT: HPM 'LINEA' RANGE
   - COLOURS - WHITE (WHITE WALLS + WHITE JOINERY)
     - BLACK (IN JOINERY END PANEL AS SHOWN)
10. **DIMMERS**
    - DIGINET LED SMART, XPERT DIMMER SWITCH (PUSH BUTTON)
    - INTEGRATED DIMMER + SWITCH

LIGHTING + SWITCHING LEGEND
- SUSPENDED CEILING LIGHT & ROSE
- WIDE BEAM RECESSED DL: CIRCULAR LED
- RECESSED DOWNLIGHT: CIRCULAR LED
- RECESSED DOWNLIGHT: LED WITH DIRECTIONAL FITTING
- WALL/BULKHEAD MOUNTED LIGHT (READ IN CONJUNCTION WITH JOINERY ELEVATIONS)
- LED — LED STRIP LIGHT ADHESIVE STRIP
- SURFACE MOUNTED DL: SQUARE LED
- LIGHT SWITCH
- LIGHT SWITCH - 2 WAY SWITCHING
- LIGHT SWITCH - DIMMER SWITCHING
- AUTOMATIC LIGHT SENSOR & OVERRIDE SWITCH
- LED STRIP LIGHT (SURFACE MOUNTED/RECESSED) REFER DRAWINGS FOR INSTALLATION DEFINITION
- FLUORESCENT LIGHT 1x36W
- FLUORESCENT LIGHT 2x36W
- EXHAUST FAN (REFER SERVICES ENG FOR PRODUCT + SPEC)
- TRICKLE VENT EXAUST FAN (FULLY AUTOMATIC PROVIDING CONTINOUS AIR EXCHANGE) (REFER SERVICES ENG FOR PRODUCT + SPEC)
- EXTERNAL WALL LIGHT
- SWEEP FAN AND LIGHT
- METAL PIPE TO HOUSE ELECTRICAL CONDUIT FIXED TO UNDER OF CLT
- HARDWIRED SMOKE DETECTOR (REFER SERVICES DWGS)
- EXTERNAL SPOT LIGHT

FOR CONSTRUCTION - 17/12/19

SCALE	DATE	REVISION
D	17/12/19	FOR CONSTRUCTION
C	31/5/19	CONTRACT SET

This drawing to require conjuction with the documents and all relevant consultants' project specification and any instructions issued during the course of the contract. Contractor must verify all dimensions on site before commencing any work. Do not scale from this drawing. Any discrepancies must be brought to the superintendent's attention.

CLIENT H.CHARALAMBOUS

Gardiner Architects
7/252 St Georges Rd, Fitzroy North, VIC, 3068
Ph: (03) 9486 4092 E: info@paulgardiner.com.au

DWG RCP - GROUND FLOOR + LEVEL 01
PROJECT RETAIL/RESIDENTIAL DEVELOPMENT
752 HIGH STREET, THORNBURY
DRAWN BY AM
SCALE 1:100 @ A1
JOB NO 141211
DWG # A.201
REV# D

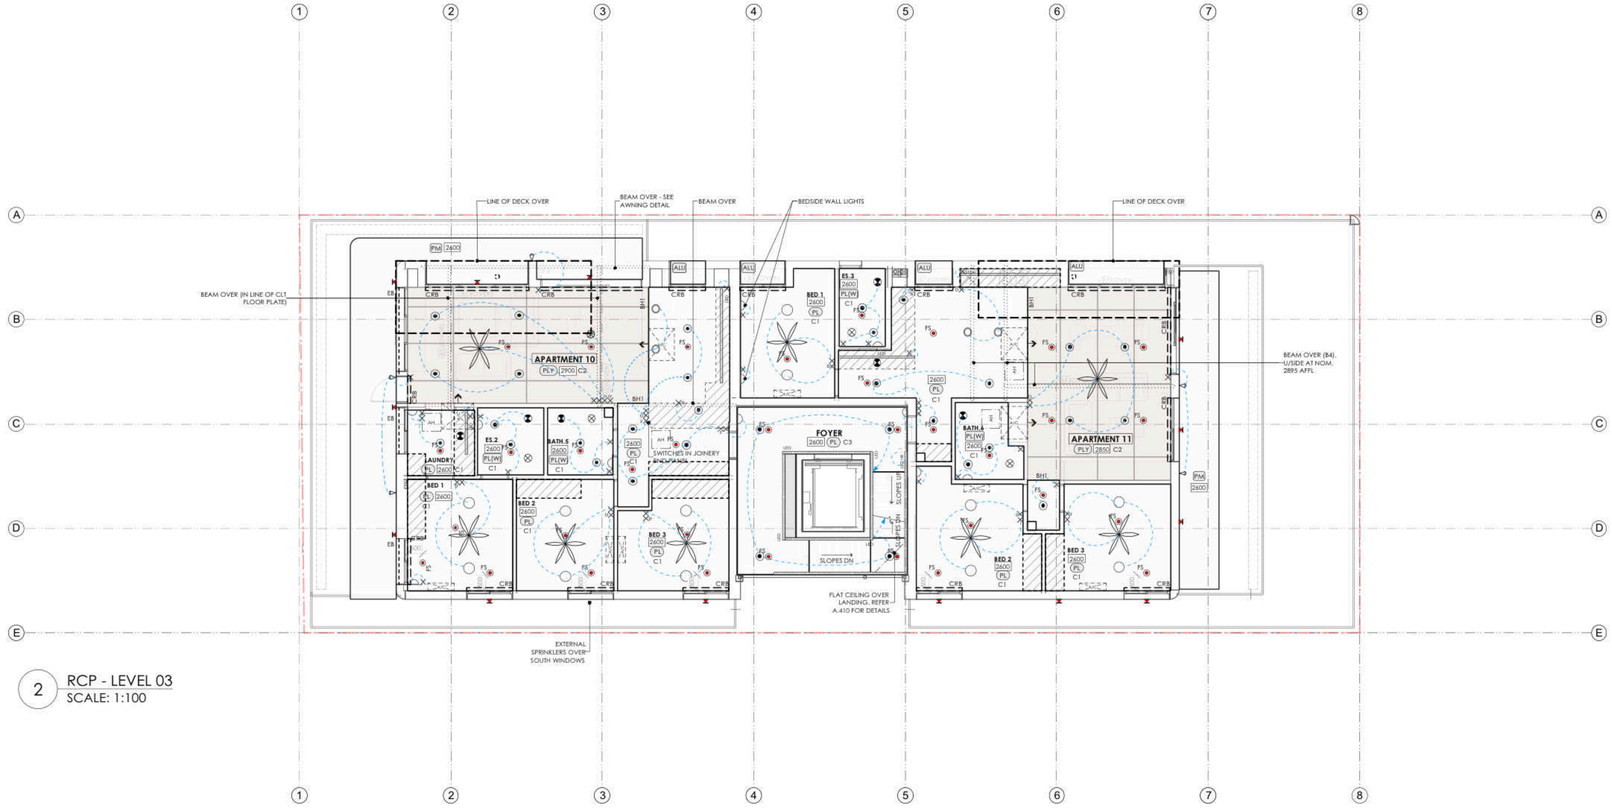

2 RCP - LEVEL 03
SCALE: 1:100

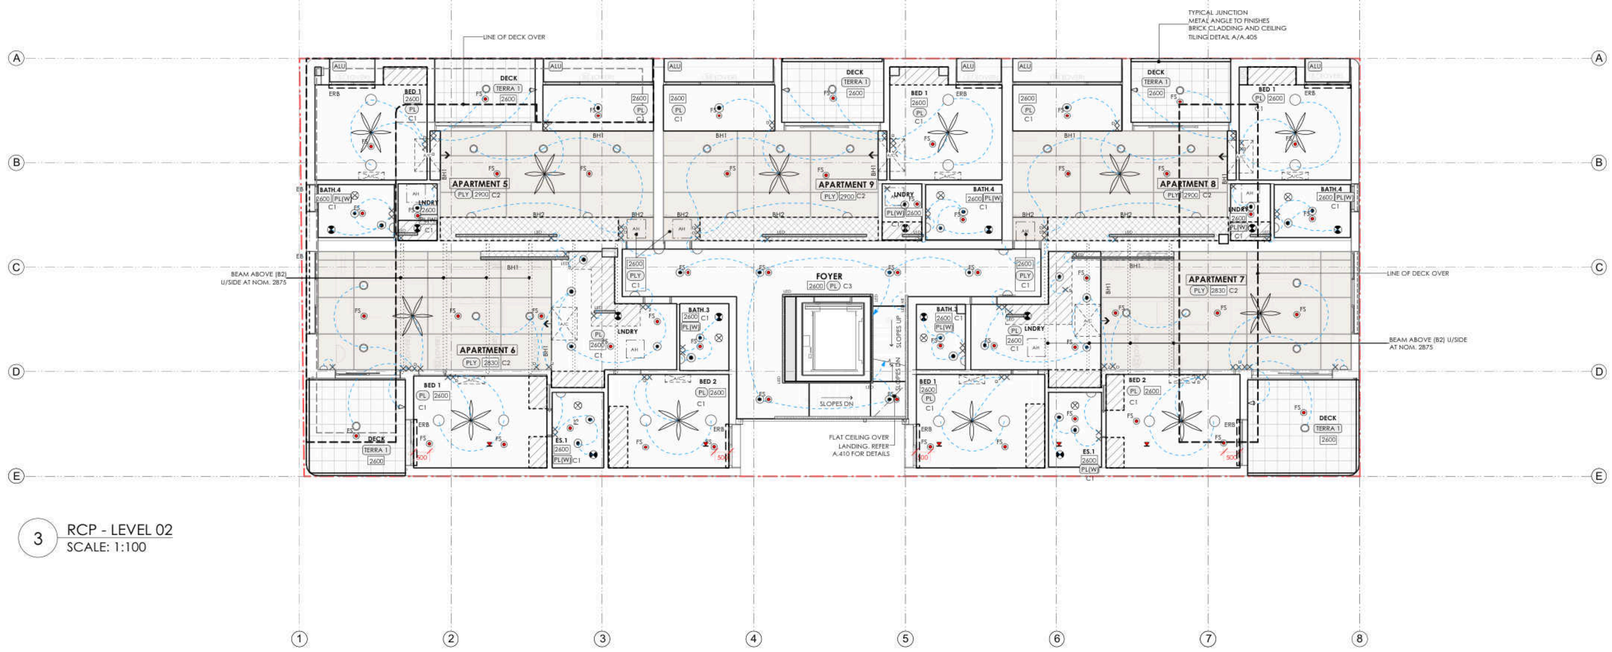

3 RCP - LEVEL 02
SCALE: 1:100

CEILING NOTES

1. READ IN CONJUNCTION WITH SPECIFICATION FOR QUALITY AND WORKMANSHIP
2. **BATTENING**
   ALL PLASTER CEILINGS TO BE BATTENED WITH ADJUSTABLE RONDO FURRING CHANNELS TO ALLOW FLAT + STRAIGHT PLASTER
3. **PREPARATION**
   ALL WALL FRAMING TO BE TRIMMED PACKED & GENERALLY READY FOR PLASTER AND/OR PLYWOOD
4. **PLASTERWORK**

LEVEL OF FINISH
- LEVEL 4 FINISH TO AS 2589:2007 (GENERALLY THROUGHOUT U.O.N.) STANDARD LEVEL OF FINISH FOR STOPPED PLASTERBOARD
- LEVEL 5 FINISH TO AS 2589:2007 HIGH LEVEL OF FINISH FOR GLANCING LIGHT & SEMI GLOSS PAINTS

PRODUCT:
USE BORAL "ENVIRO" RANGE OR SIMILAR APPROVED

GENERAL
- 2600 FINISHED HEIGHT ABOVE FINISHED FLOOR LEVEL (FFL)
- PRODUCTS TO BE ORDERED AS SPECIFIED UNLESS OTHERWISE APPROVED.
- JOINERY BELOW, FULL HEIGHT
- JOINERY BELOW, UP TO BULKHEAD

CEILING LEGEND

LININGS

PL — PLASTERBOARD 13MM THICK FLUSH JOINTED FOR PAINT FINISH

PLW — WATERPROOF PLASTERBOARD 13MM FLUSH JOINTED SOFFIT LINING, PAINTED FINISH - BORAL WET AREA BOARD OR SIMILAR APPROVED

PLY — 26mm THICK
PRODUCT: MDF WITH HOOP PINE VENEER
(REFER WALL+FLOOR BUILDUP A.107, DETAIL 33 FOR DETAILS)

CONC — EXPOSED CONCRETE SLAB OVER BONDEK TRAY (NO FINISH)

MET — FLAT COLORBOND SHEET
MATERIAL: COLOURBOND STEEL ADHERED TO 18MM MARINE PLY SUBSTRATE
COLOUR: BLACK (TBC)

TERRA 1 — TERRACOTTA SOFFIT TILE
ADHESIVE FIX
REFER SCHEDULES FOR PRODUCT AND A.106/A.107 FOR DETAIL

PM — PERFORATED METAL TO UNDERSIDE OF AWNING
REFER A.407 FOR DETAIL

ALU — FABRICATED PRE-FINISHED ALUMINIUM REVEAL
COLOUR: DARK GREY (TBC)

CORNICES

TYPE 1 CORNICE - SQUARE SET

C1 TYPE 2 CORNICE - 10MM SHADOWLINE (REFER TYPICAL DETAIL C/A.201)

C2 TYPE 2 CORNICE - 5MM SHADOWLINE (REFER TYPICAL DETAIL D/A.201)

MISC.

AH — ACCESS HATCH - FLUSH CONCEALED HATCH PAINTED FINISH, U.O.N. SIZE: NOM. 600 x 600

MECHANICAL

AIR CONDITIONING DIFUSER FLUSH TO CEILING. FINISH: SELECTED POWDERCOAT COLOUR

ABOVE CEILING CONCEALED SPLIT A/C UNIT WITH ACCESS HATCH ARROW INDICATES GRILLE DIRECTION SIZE: NOM. 1050 x 850

WALL MOUNTED A/C UNIT

SERVICES

FIRE SPRINKLER BRANCH

FIRE SPRINKLER NEW

FS — FIRE SPRINKLER SIDEWALL

STRUCTURAL STEEL

STRUCTURAL STEEL - CONCEALED IN CEILING (REFER STRUCTURAL PLANS FOR DETAIL)

INTERNAL WINDOW FURNISHING SCHEDULE
NOTES:
- REFER PROVISIONAL SUMM
- READ IN CONJUNCTION WITH WINDOW SCHEDULE

EB — EXTERNAL MOTORIZED RECESSED DROP DOWN ALUMINIUM VENETIAN BLIND (REFER SCHEDULES FOR PRODUCT) REFER DETAIL B/A.405

ERB — EXPOSED ROLLER BLIND ON SASH REFER DETAIL A/A.405

CRB — CONCEALED ROLLER BLIND REFER DETAIL A/A.405

LIGHTING NOTES

1. READ IN CONJUNCTION WITH SPECIFICATION.
2. ARTIFICIAL LIGHT TO COMPLY WITH AS1680
3. LIGHTING LAYOUT TBC BY ARCHITECT ON SITE
4. PLY CEILING LAYOUT TBC BY ARCHITECT ON SITE
5. EUROPEAN LAUNDRIES WITH FOLDING DOORS TO HAVE SWITCHES INSIDE CAVITY END PANELS AT NOM. 1500MM AFFL - REFER JOINERY DWGS FOR DETAIL
6. **LIGHT FITTINGS**
   INSTALLATION: BY BUILDER
   SELECTIONS: REFER SCHEDULE OF LIGHT FITTINGS IN "SCHEDULES" + PC SUMS FOR SUPPLY ONLY ALLOWANCE
   SHROUDS: ALL RECESSED DOWNLIGHTS ARE REQUIRED TO HAVE SHROUDS INSTALLED TO MANUFACTURERS SPECIFICATIONS
   PRODUCT: EXFOLIATORS AUSTRALIA FIRE RATED DOWN LIGHT COVERS SIZED AS APPROPRIATE AND INSTALLED AS PER MANUFACTURER'S SPEC
7. **WIRING**
   - ALL EXISTING LIGHTING WIRING TO BE RETAINED/REPLACED WITH NEW TO LOCATIONS AS SHOWN ON PLANS
8. **ENERGY RATING**
   - LED LIGHT FITTINGS TO BE INSTALLED GENERALLY
   - LIGHT FITTINGS TO COMPLY WITH BCA 6 STAR ENERGY RATING REQUIREMENT
   - TOTAL MAXIMUM ILLUMINATION POWER SHOULD NOT EXCEED:
     - 5 WATTS/SQM FOR INTERNAL AREAS
     - 4 WATTS/SQM FOR EXTERNAL AREAS
     - 3 WATTS/SQM FOR GARAGES
9. **SWITCHES & PRODUCTS**
   - PRODUCT: HPM 'LINEA' RANGE
   - COLOURS - WHITE (WHITE WALLS + WHITE JOINERY)
     - BLACK (IN JOINERY END PANEL AS SHOWN)
10. **DIMMERS**
    - DIGINET LED SMART, XPERT DIMMER SWITCH (PUSH BUTTON)
    - INTEGRATED DIMMER + SWITCH

LIGHTING + SWITCHING LEGEND

- SUSPENDED CEILING LIGHT & ROSE
- WIDE BEAM RECESSED DL: CIRCULAR LED
- RECESSED DOWNLIGHT: CIRCULAR LED
- RECESSED DOWNLIGHT: LED WITH DIRECTIONAL FITTING
- WALL/BULKHEAD MOUNTED LIGHT (READ IN CONJUNCTION WITH JOINERY ELEVATIONS)
- LED STRIP LIGHT ADHESIVE STRIP
- SURFACE MOUNTED DL: SQUARE LED
- LIGHT SWITCH
- LIGHT SWITCH - 2 WAY SWITCHING
- LIGHT SWITCH - DIMMER SWITCHING
- AUTOMATIC LIGHT SENSOR & OVERRIDE SWITCH
- LED STRIP LIGHT (SURFACE MOUNTED/RECESSED) REFER DRAWINGS FOR INSTALLATION DEFINITION
- FLUORESCENT LIGHT 1x36W
- FLUORESCENT LIGHT 2x36W
- EXHAUST FAN (REFER SERVICES ENG FOR PRODUCT + SPEC)
- TRICKLE VENT EXAUST FAN (FULLY AUTOMATIC PROVIDING CONTINOUS AIR EXCHANGE) (REFER SERVICES ENG FOR PRODUCT + SPEC)
- EXTERNAL WALL LIGHT
- SWEEP FAN AND LIGHT
- METAL PIPE TO HOUSE ELECTRICAL CONDUIT FIXED TO UNDER OF CLT
- HARDWIRED SMOKE DETECTOR (REFER SERVICES DWGS)
- EXTERNAL SPOT LIGHT

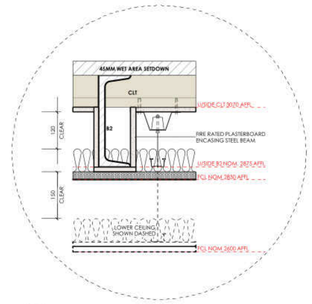

A CLG DETAIL - BEAM B2
SCALE: 1:10

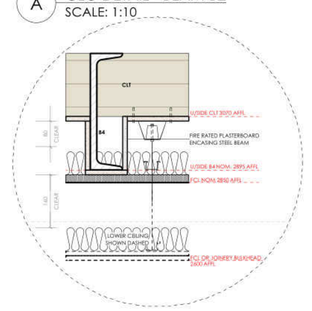

B CLG DETAIL - BEAM B4
SCALE: 1:10

FOR CONSTRUCTION - 17/12/19

ISSUE	DATE	REVISION
D	17/12/19	FOR CONSTRUCTION
C	31/5/19	CONTRACT SET
A	27/2/18	Exposed engineered timber ceiling in living areas changed to plywood lining

This drawing to require conjunction with the relevant architectural drawings, with the project specification and any instructions issued during the course of the contract. Contractor must verify all dimensions on site before commencing any work. Do not scale from this drawing. Drawing is the property of Gardiner Architects Pty Ltd and may not be reproduced or transmitted.

CLIENT H.CHARALAMBOUS

Gardiner Architects
7/252 St Georges Rd, Fitzroy North, VIC, 3068
Ph: (03) 9486 4092 E: info@paulgardiner.com.au

DWG **RCP - LEVEL 02 + LEVEL 03**
PROJECT RETAIL/RESIDENTIAL DEVELOPMENT
752 HIGH STREET, THORNBURY
DRAWN BY AM
SCALE 1:100 @ A1
JOB NO 141211
A.202
DWG #
REV# D

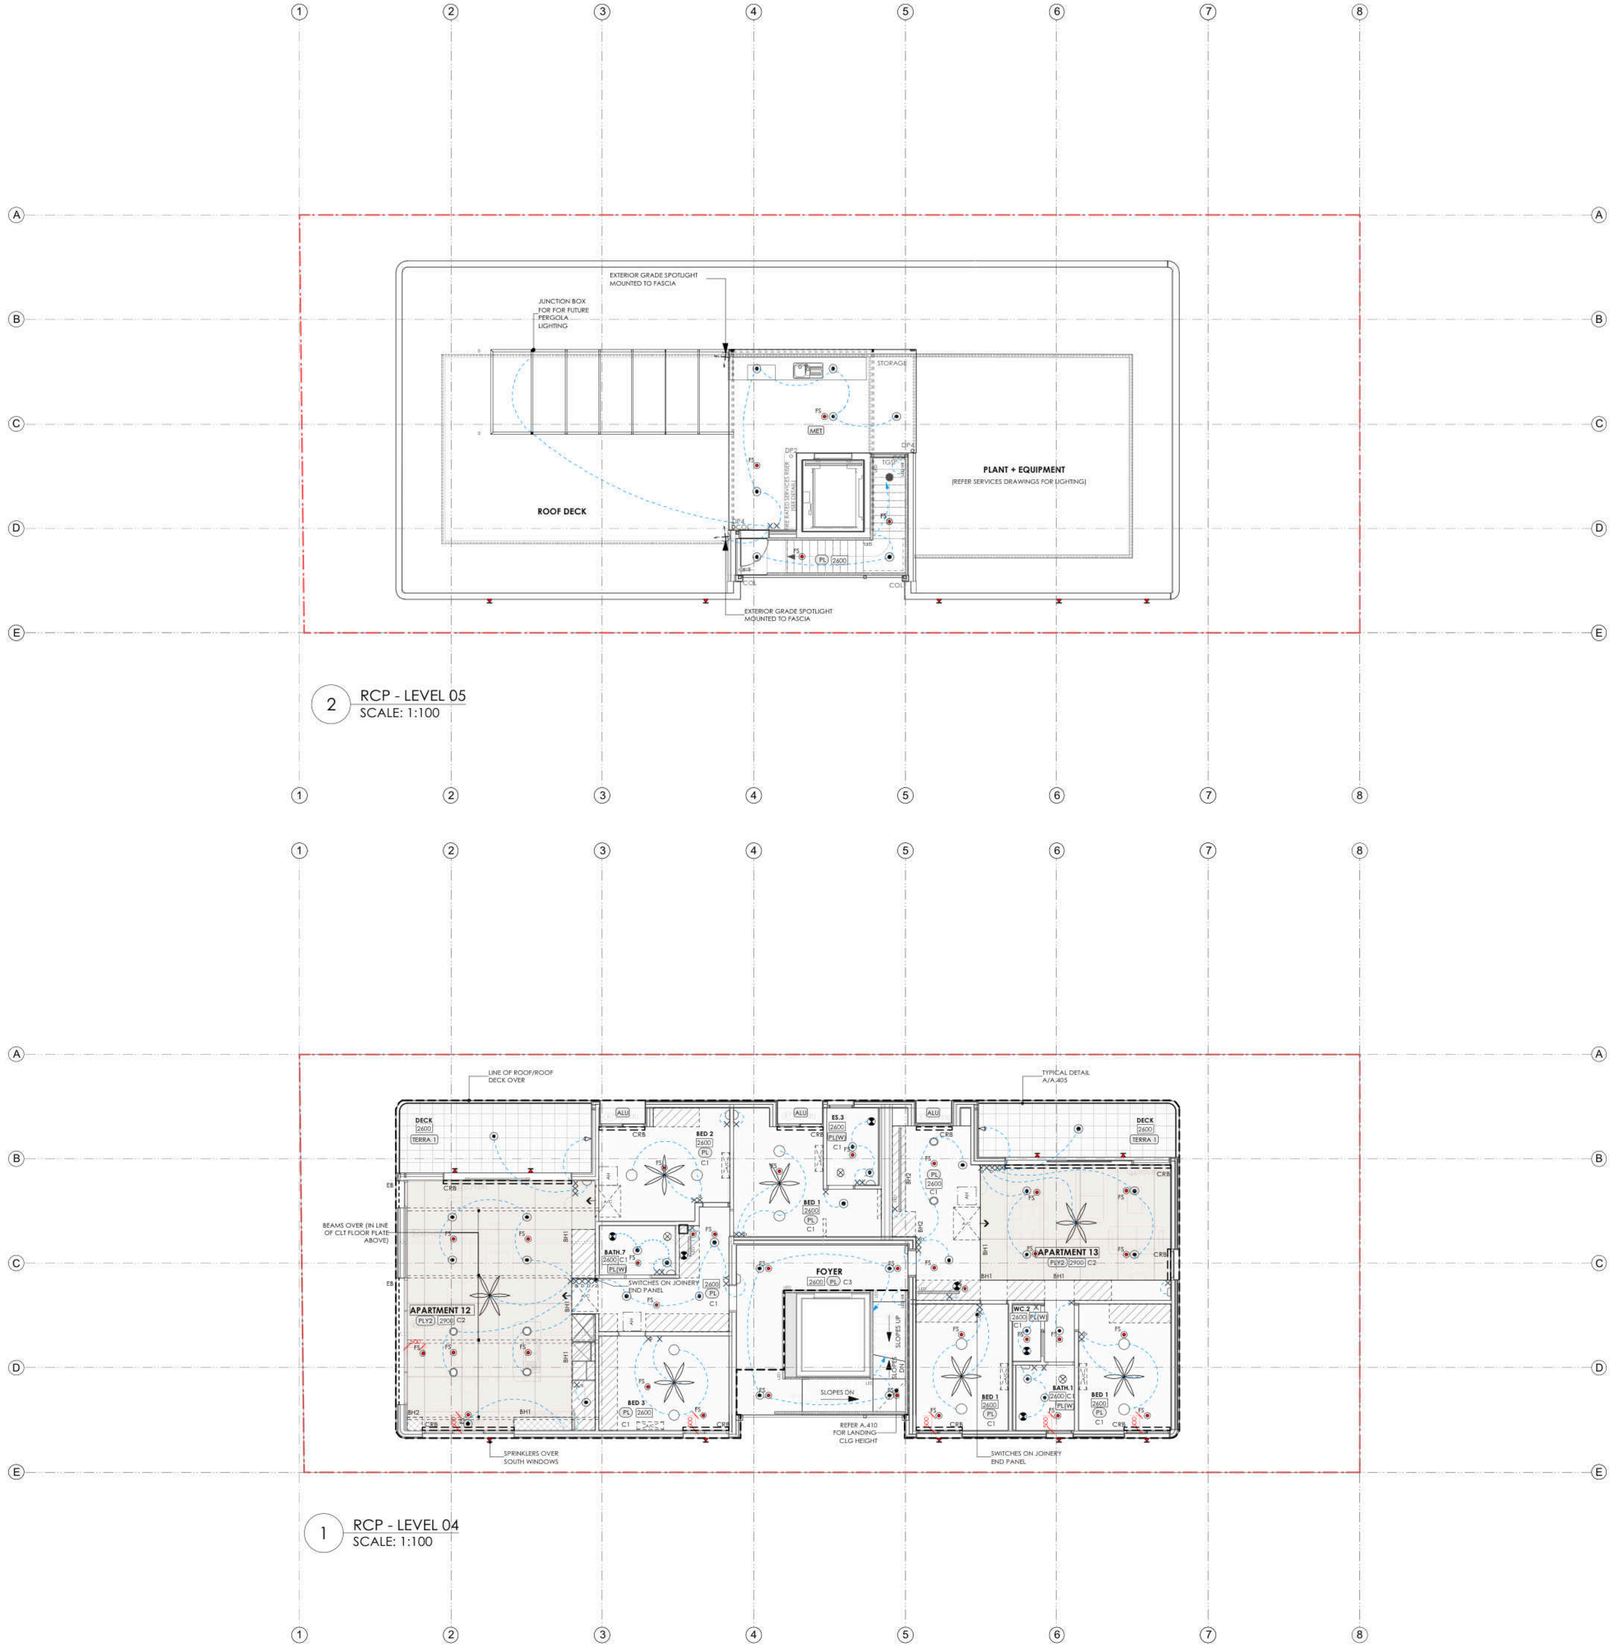

2 RCP - LEVEL 05
SCALE: 1:100

1 RCP - LEVEL 04
SCALE: 1:100

CEILING NOTES

1. READ IN CONJUNCTION WITH SPECIFICATION FOR QUALITY AND WORKMANSHIP
2. **BATTENING**
   ALL PLASTER CEILINGS TO BE BATTENED WITH ADJUSTABLE RONDO FURRING CHANNELS TO ALLOW FLAT + STRAIGHT PLASTER
3. **PREPARATION**
   ALL WALL FRAMING TO BE TRIMMED PACKED & GENERALLY READY FOR PLASTER AND/OR PLYWOOD
4. **PLASTERWORK**

LEVEL OF FINISH
- LEVEL 4 FINISH TO AS 2589:2007 (GENERALLY THROUGHOUT U.O.N.) STANDARD LEVEL OF FINISH FOR STOPPED PLASTERBOARD
- LEVEL 5 FINISH TO AS 2589:2007 HIGH LEVEL OF FINISH FOR GLANCING LIGHT & SEMI GLOSS PAINTS

PRODUCT:
USE BORAL "ENVIRO" RANGE OR SIMILAR APPROVED

GENERAL
- 2600 FINISHED HEIGHT ABOVE FINISHED FLOOR LEVEL (FFL)
- PRODUCTS TO BE ORDERED AS SPECIFIED UNLESS OTHERWISE APPROVED.
- JOINERY BELOW, FULL HEIGHT
- JOINERY BELOW, UP TO BULKHEAD

CEILING LEGEND

LININGS

PL — PLASTERBOARD 13MM THICK FLUSH JOINTED FOR PAINT FINISH

PLW — WATERPROOF PLASTERBOARD 13MM FLUSH JOINTED SOFFIT LINING, PAINTED FINISH - BORAL WET AREA BOARD OR SIMILAR APPROVED

PLY — 26mm THICK PRODUCT: MDF WITH HOOP PINE VENEER (REFER WALL+FLOOR BUILDUP A.107, DETAIL 33 FOR DETAILS)

CONC — EXPOSED CONCRETE SLAB OVER BONDEK TRAY (NO FINISH)

MET — FLAT COLORBOND SHEET
MATERIAL: COLOURBOND STEEL ADHERED TO 18MM MARINE PLY SUBSTRATE
COLOUR: BLACK (TBC)

TERRA 1 — TERRACOTTA SOFFIT TILE
ADHESIVE FIX
REFER SCHEDULES FOR PRODUCT AND A.106/A.107 FOR DETAIL

PM — PERFORATED METAL TO UNDERSIDE OF AWNING
REFER A.407 FOR DETAIL

ALU — FABRICATED PRE-FINISHED ALUMINIUM REVEAL
COLOUR: DARK GREY (TBC)

CORNICES

TYPE 1 CORNICE - SQUARE SET

C1 TYPE 2 CORNICE - 10MM SHADOWLINE (REFER TYPICAL DETAIL C/A.201)

C2 TYPE 2 CORNICE - 5MM SHADOWLINE (REFER TYPICAL DETAIL D/A.201)

MISC.

AH — ACCESS HATCH- FLUSH CONCEALED HATCH PAINTED FINISH, U.O.N.
SIZE: NOM. 600 x 600

MECHANICAL

AIR CONDITIONING DIFUSER
FLUSH TO CEILING.
FINISH: SELECTED POWDERCOAT COLOUR

ABOVE CEILING CONCEALED SPLIT A/C UNIT WITH ACCESS HATCH. ARROW INDICATES GRILLE DIRECTION
SIZE: NOM. 1050 x 850

WALL MOUNTED A/C UNIT

SERVICES

FIRE SPRINKLER BRANCH

FIRE SPRINKLER NEW

FS — FIRE SPRINKLER SIDEWALL

STRUCTURAL STEEL

STRUCTURAL STEEL - CONCEALED IN CEILING
(REFER STRUCTURAL PLANS FOR DETAIL)

INTERNAL WINDOW FURNISHING SCHEDULE

NOTES:
- REFER PROVISIONAL SUMM
- READ IN CONJUNCTION WITH WINDOW SCHEDULE

EB — EXTERNAL MOTORIZED RECESSED DROP DOWN ALUMINIUM VENETIAN BLIND
(REFER SCHEDULES FOR PRODUCT)
REFER DETAIL B/A.405

EBS — EXPOSED ROLLER BLIND ON SASH
REFER DETAIL A/A.405

CRB — CONCEALED ROLLER BLIND
REFER DETAIL A/A.405

LIGHTING NOTES

1. READ IN CONJUNCTION WITH SPECIFICATION.
2. ARTIFICIAL LIGHT TO COMPLY WITH AS1680
3. LIGHTING LAYOUT TBC BY ARCHITECT ON SITE
4. PLY CEILING LAYOUT TBC BY ARCHITECT ON SITE
5. EUROPEAN LAUNDRIES WITH FOLDING DOORS TO HAVE SWITCHES INSIDE CAVITY END PANELS AT NOM. 1500MM AFFL - REFER JOINERY DWGS FOR DETAIL
6. **LIGHT FITTINGS**
   INSTALLATION: BY BUILDER
   SELECTIONS: REFER SCHEDULE OF LIGHT FITTINGS IN "SCHEDULES" + PC SUMS FOR SUPPLY ONLY ALLOWANCE
   SHROUDS: ALL RECESSED DOWNLIGHTS ARE REQUIRED TO HAVE SHROUDS INSTALLED TO MANUFACTURERS SPECIFICATIONS
   PRODUCT: EXFOLIATORS AUSTRALIA FIRE RATED DOWN LIGHT COVERS SIZED AS APPROPRIATE AND INSTALLED AS PER MANUFACTURER'S SPEC
7. **WIRING**
   - ALL EXISTING LIGHTING WIRING TO BE RETAINED/REPLACED WITH NEW TO LOCATIONS AS SHOWN ON PLANS
8. **ENERGY RATING**
   - LED LIGHT FITTINGS TO BE INSTALLED GENERALLY
   - LIGHT FITTINGS TO COMPLY WITH BCA 6 STAR ENERGY RATING REQUIREMENT
   - TOTAL MAXIMUM ILLUMINATION POWER SHOULD NOT EXCEED:
     - 5 WATTS/SQM FOR INTERNAL AREAS
     - 4 WATTS/SQM FOR EXTERNAL AREAS
     - 3 WATTS/SQM FOR GARAGES
9. **SWITCHES & PRODUCTS**
   - PRODUCT: HPM 'LINEA' RANGE
   - COLOURS - WHITE (WHITE WALLS + WHITE JOINERY)
     - BLACK (IN JOINERY END PANEL AS SHOWN)
10. **DIMMERS**
    - DIGINET LED SMART, XPERT DIMMER SWITCH (PUSH BUTTON)
    - INTEGRATED DIMMER + SWITCH

LIGHTING + SWITCHING LEGEND

- SUSPENDED CEILING LIGHT & ROSE
- WIDE BEAM RECESSED DL: CIRCULAR LED
- RECESSED DOWNLIGHT: CIRCULAR LED
- RECESSED DOWNLIGHT: LED WITH DIRECTIONAL FITTING
- WALL/BULKHEAD MOUNTED LIGHT (READ IN CONJUNCTION WITH JOINERY ELEVATIONS)
- LED STRIP LIGHT ADHESIVE-STRIP
- SURFACE MOUNTED DL: SQUARE LED
- LIGHT SWITCH
- LIGHT SWITCH - 2 WAY SWITCHING
- LIGHT SWITCH - DIMMER SWITCHING
- AUTOMATIC LIGHT SENSOR & OVERRIDE SWITCH
- LED STRIP LIGHT (SURFACE MOUNTED/RECESSED) REFER DRAWINGS FOR INSTALLATION DEFINITION
- 1x36W FLUORESCENT LIGHT
- 2x36W FLUORESCENT LIGHT
- EXHAUST FAN (REFER SERVICES ENG FOR PRODUCT + SPEC)
- TRICKLE VENT EXAUST FAN (FULLY AUTOMATIC PROVIDING CONTINOUS AIR EXCHANGE) (REFER SERVICES ENG FOR PRODUCT + SPEC)
- EXTERNAL WALL LIGHT
- SWEEP FAN AND LIGHT
- METAL PIPE TO HOUSE ELECTRICAL CONDUIT FIXED TO UNDER OF CLT
- HARDWIRED SMOKE DETECTOR (REFER SERVICES DWGS)
- EXTERNAL SPOT LIGHT

FOR CONSTRUCTION - 17/12/19

ISSUE	DATE	REVISION
D	17/12/19	FOR CONSTRUCTION
C	31/5/19	CONTRACT SET
A	27/2/18	Exposed engineered timber ceiling in living areas changed to plywood lining

This drawing to require conjuction with the documents and all relevant consultants project specification and any instructions issued during the course of the contract. Contractor must verify all dimensions on site before commencing any work. Do not scale from this drawing. Refer to Architect if unclear or discrepancies in documents.

CLIENT H.CHARALAMBOUS

Gardiner Architects
7/252 St Georges Rd, Fitzroy North, VIC, 3068
Ph: (03) 9486 4092 E: info@paulgardiner.com.au

DWG RCP - LEVEL 04 + LEVEL 05
PROJECT RETAIL/RESIDENTIAL DEVELOPMENT
752 HIGH STREET, THORNBURY
JOB NO 141211
DRAWN BY AM
SCALE 1:100 @ A1
A.203
DWG #
REV# D

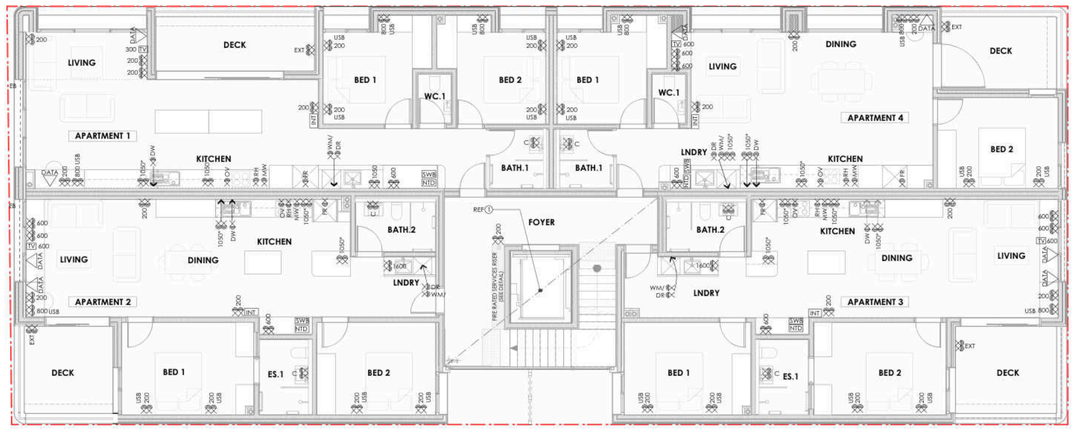

2 ELECTRICAL PLAN - LEVEL 01
SCALE: 1:100

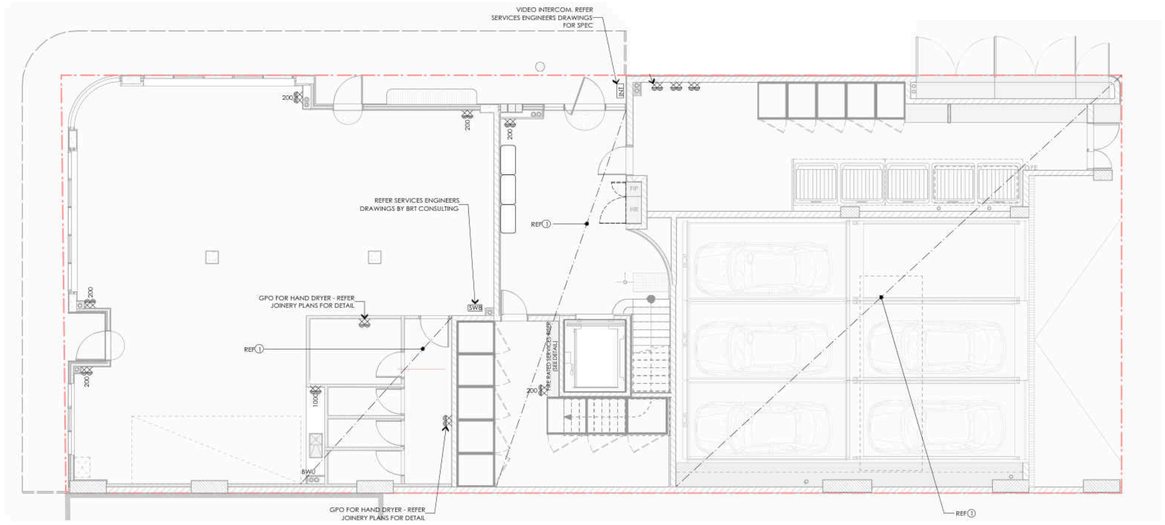

1 ELECTRICAL PLAN - LEVEL GR
SCALE: 1:100

DRAWING DEMARCATION

REF 1 REFER SERVICES ENGINEER'S DRAWINGS BY BRT CONSULTING

U.O.N. - GARDINER ARCHITECTS DRAWINGS INDICATE GPO'S + OTHER ELECTRICAL SERVICES
- SERVICES ENGINEER TO INDICATE ALL SWITCHBOARD + INFRASTRUCTURE

ELECTRICAL NOTES

1. **READ IN CONJUNCTION WITH SPECIFICATION**
2. **READ IN CONJUNCTION WITH ENGINEERS DRAWINGS:** SERVICES ENGINEERING - REFER TO ENGINEER'S DRAWINGS BY BRT CONSULTING (REF 9323 DATED - 18/14/17)
3. **SWITCHBOARD** REFER TO ENGINEER'S DRAWINGS BY BRT CONSULTING
4. **SOLAR POWER GENERATION** REFER TO ENGINEER'S DRAWINGS BY BRT CONSULTING
5. **MAINS** REFER TO ENGINEER'S DRAWINGS BY BRT CONSULTING
6. **FITTINGS** BUILDER TO ALLOW SUPPLY AND DELIVERY OF ALL FITTINGS
   PRODUCT - POWER POINTS & SWITCHES CLIPSAL MPM 'LINEA' RANGE
   COLOUR: - WHITE (WHITE WALLS + WHITE JOINERY)
   - BLACK (COLOURED WALLS + DARK COLOURED/VENEER JOINERY)
   HEIGHTS - U.O.N. ALL SWITCHES TO BE MOUNTED @ 1200mm & POWER POINTS @ 300mm ABOVE FFL
7. **SECURITY SYSTEM** REFER TO ENGINEER'S DRAWINGS BY BRT CONSULTING
8. **INTERCOM SERVICE** LOCATED ADJACENT FRONT DOOR ON INSIDE OF EACH APARTMENT - REFER TO ENGINEER'S DRAWINGS BY BRT CONSULTING
9. **INTERNET SERVICE (NBN).**
   - NBN CONNECTION SUPPLIED TO EACH APARTMENT.
   - NTD (NETWORK TERMINATION DEVICE) FOR INCOMING NBN SUPPLIED TO ALL APARTMENTS
   - REFER TO ENGINEER'S DRAWINGS BY BRT CONSULTING
10. **WIRELESS ACCESS POINTS**
    - CONNECTED TO NTD IN EACH APARTMENT AS PER DRAWINGS - REFER TO ENGINEER'S DRAWINGS BY BRT CONSULTING
11. **TELEPHONE SERVICE (VOIP)** VOIP SUPPLIED DATA POINT CONNECTED TO NTD IN EACH APARTMENT - REFER TO ENGINEER'S DRAWINGS BY BRT CONSULTING
12. **TELEVISION (FREE TO AIR)**
    - AERIAL POINT TO EACH APARTMENT - REFER TO ENGINEER'S DRAWINGS BY BRT CONSULTING
13. **TELEVISION (SMART TV)**
    - DATA POINT CONNECTED TO NTD IN EACH APARTMENT - REFER TO ENGINEER'S DRAWINGS BY BRT CONSULTING
14. **AIR CONDITIONING** REFER TO ENGINEER'S DRAWINGS BY BRT CONSULTING
15. **ELECTRIC OVENS** SEPERATE CIRCUIT FOR OVENS - REFER TO ENGINEER'S DRAWINGS BY BRT CONSULTING

ELECTRICAL LEGEND

300	SINGLE GPO @ 300MM ABOVE FFL
200	DOUBLE GPO @ 200MM ABOVE FFL
600	DOUBLE GPO @ 600MM ABOVE FFL
800	DOUBLE GPO @ 800MM ABOVE FFL
1050*	DOUBLE GPO @ CENTRED ON WALL TILE *NOM. 1050MM ABOVE FFL NOTE LAUNDRY GPOS TO BE MOUNTED ON SIDE PANEL. IF SPLASHBACK LOCATION IS NOT POSSIBLE DUE TO REGULATIONS
1600	DOUBLE GPO @ 1600MM ABOVE FFL MOUNTED ON LAUNDRY JOINERY SIDE PANEL
C	DOUBLE GPO FLUSH MOUNTED AND CONCEALED IN UNDERSIDE OF BATHROOM CABINET
EXT	EXTERNAL GPO - WATERPROOF - @ 300MM ABOVE FFL
DW	SINGLE GPO (DISHWASHER) - LOCATED AS PER DRAWINGS
FR	SINGLE GPO (FRIDGE)@ 1700MM ABOVE FFL - LOCATED AS PER DRAWINGS
OV	OVEN - DIRECT WIRE
RH	SINGLE GPO (RANGEHOOD) - LOCATED AS PER DRAWINGS
MW	SINGLE GPO (MICROWAVE) - LOCATED AS PER DRAWINGS
WM/DR	DOUBLE GPO (WASHING MACHINE + DRYER) - LOCATED AS PER DRAWINGS
USB	GPO WITH INTEGRATED USB
TV 300	TV AERIAL POINT @ 300MM ABOVE FFL
TV 600	TV AERIAL POINT @ 600MM ABOVE FFL
NTD	NTD (NETWORK TERMINATION DEVICE)
DATA	INTERNET/DATA POINT - FOR WI-FI MODEM/VOIP COMPATIBLE PHONE - BY TENANT
INT	VIDEO INTERCOM
MET	ELECTRICITY METER
SWB	SWITCHBOARD
SEC	SECURITY SYSTEM HUB
BWU	BOILING WATER UNIT
EB	EXTERNAL MOTORISED ALUMINIUM VENETIAN BLIND HARDWIRED (REFER SCHEDULES FOR PRODUCT)

FOR CONSTRUCTION - 17/12/19

This drawing to require conjunction with the whole of the architect's and consultant's documentation and any instruction issued during the course of the contract. Verify all dimensions on site before commencing any work. Do not scale any dimensions from drawings. Refer to architect of all discrepancies in documents.

ISSUE	DATE	REVISION
D	17/12/19	FOR CONSTRUCTION
C	31/5/19	CONTRACT SET

CLIENT H.CHARALAMBOUS

Gardiner Architects
77/252 St Georges Rd, Fitzroy North, VIC, 3068
Ph: (03) 9486 4092 E: info@paulgardiner.com.au

DWG **ELECTRICAL PLAN - GROUND FLOOR + LEVEL 01**
PROJECT RETAIL/RESIDENTIAL DEVELOPMENT 752 HIGH STREET, THORNBURY
DRAWN BY AM
SCALE 1:100 @ A1
JOB NO 141211
DWG # A.204
REV# D

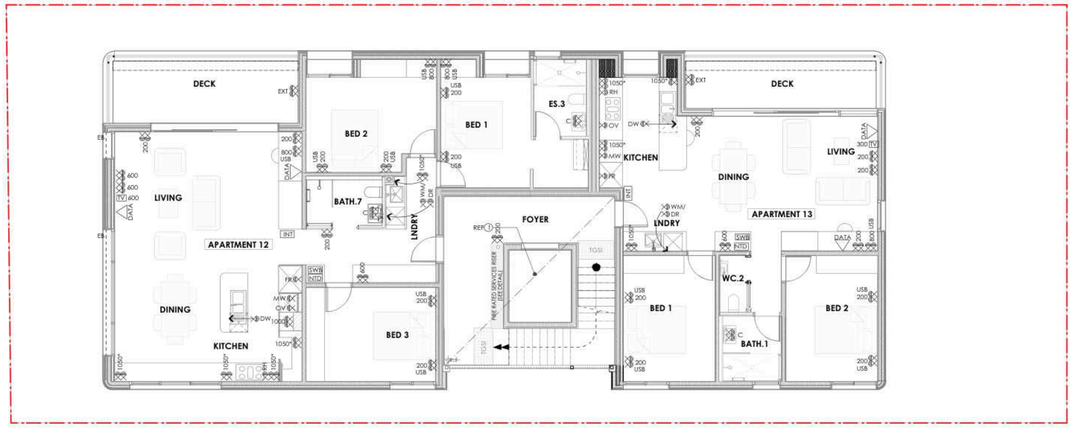

3 ELECTRICAL PLAN - LEVEL 04
SCALE: 1:100

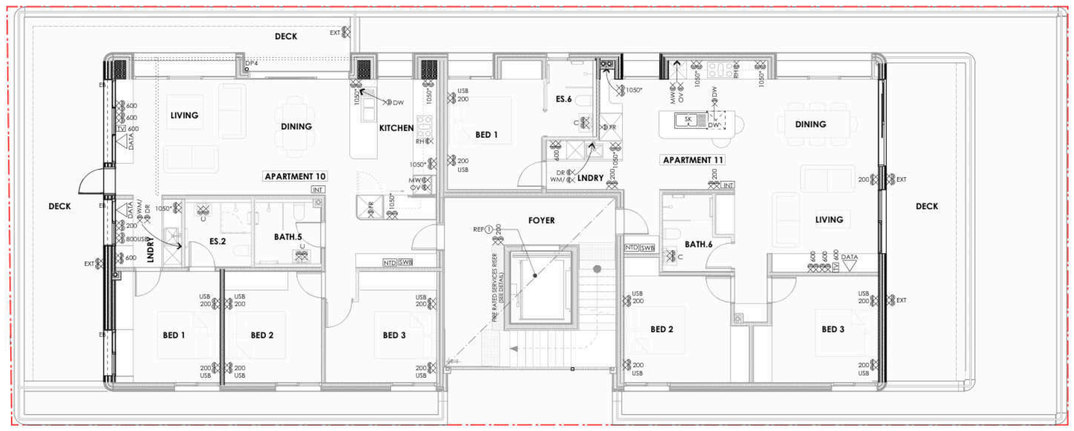

2 ELECTRICAL PLAN - LEVEL 03
SCALE: 1:100

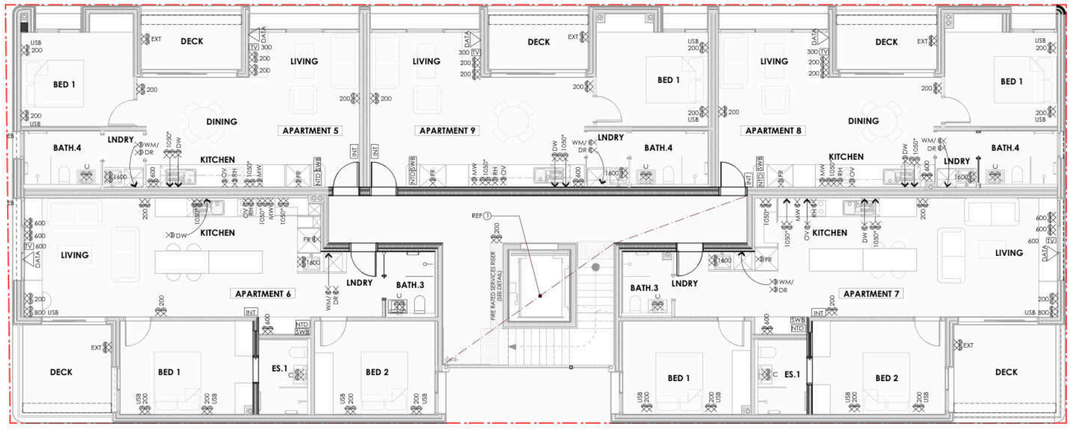

1 ELECTRICAL PLAN - LEVEL 02
SCALE: 1:100

DRAWING DEMARCATION

REF 1 REFER SERVICES ENGINEER'S DRAWINGS BY BRT CONSULTING

U.O.N. - GARDINER ARCHITECTS DRAWINGS INDICATE GPO'S + OTHER ELECTRICAL SERVICES
- SERVICES ENGINEER TO INDICATE ALL SWITCHBOARD + INFRASTRUCTURE

ELECTRICAL NOTES

1. **READ IN CONJUNCTION WITH SPECIFICATION**
2. **READ IN CONJUNCTION WITH ENGINEERS DRAWINGS:** SERVICES ENGINEERING - REFER TO ENGINEER'S DRAWINGS BY BRT CONSULTING (REF 9323 DATED - 18/14/17)
3. **SWITCHBOARD** REFER TO ENGINEER'S DRAWINGS BY BRT CONSULTING
4. **SOLAR POWER GENERATION** REFER TO ENGINEER'S DRAWINGS BY BRT CONSULTING
5. **MAINS** REFER TO ENGINEER'S DRAWINGS BY BRT CONSULTING
6. **FITTINGS** BUILDER TO ALLOW SUPPLY AND DELIVERY OF ALL FITTINGS
   PRODUCT - POWER POINTS & SWITCHES CLIPSAL 'IPM/ LINEA' RANGE
   COLOUR: - WHITE (WHITE WALLS + WHITE JOINERY)
   - BLACK (COLOURED WALLS + DARK COLOURED/VENEER JOINERY)
   HEIGHTS - U.O.N. ALL SWITCHES TO BE MOUNTED @ 1200mm & POWER POINTS @ 300mm ABOVE FFL
7. **SECURITY SYSTEM** REFER TO ENGINEER'S DRAWINGS BY BRT CONSULTING
8. **INTERCOM SERVICE** LOCATED ADJACENT FRONT DOOR ON INSIDE OF EACH APARTMENT - REFER TO ENGINEER'S DRAWINGS BY BRT CONSULTING
9. **INTERNET SERVICE (NBN).** - NBN CONNECTION SUPPLIED TO EACH APARTMENT. - NTD (NETWORK TERMINATION DEVICE) FOR INCOMING NBN SUPPLIED TO ALL APARTMENTS - REFER TO ENGINEER'S DRAWINGS BY BRT CONSULTING
10. **WIRELESS ACCESS POINTS** - CONNECTED TO NTD IN EACH APARTMENT AS PER DRAWINGS - REFER TO ENGINEER'S DRAWINGS BY BRT CONSULTING
11. **TELEPHONE SERVICE (VOIP)** VOIP SUPPLIED DATA POINT CONNECTED TO NTD IN EACH APARTMENT - REFER TO ENGINEER'S DRAWINGS BY BRT CONSULTING
12. **TELEVISION (FREE TO AIR)** - AERIAL POINT TO EACH APARTMENT - REFER TO ENGINEER'S DRAWINGS BY BRT CONSULTING
13. **TELEVISION (SMART TV)** - DATA POINT CONNECTED TO NTD IN EACH APARTMENT - REFER TO ENGINEER'S DRAWINGS BY BRT CONSULTING
14. **AIR CONDITIONING** REFER TO ENGINEER'S DRAWINGS BY BRT CONSULTING
15. **ELECTRIC OVENS** SEPERATE CIRCUIT FOR OVENS - REFER TO ENGINEER'S DRAWINGS BY BRT CONSULTING

ELECTRICAL LEGEND

- 300 SINGLE GPO @ 300MM ABOVE FFL
- 200 DOUBLE GPO @ 200MM ABOVE FFL
- 600 DOUBLE GPO @ 600MM ABOVE FFL
- 800 DOUBLE GPO @ 800MM ABOVE FFL
- 1050* DOUBLE GPO @ CENTRED ON WALL TILE *NOM. 1050MM ABOVE FFL NOTE LAUNDRY GPOS TO BE MOUNTED ON SIDE PANEL. IF SPLASHBACK LOCATION IS NOT POSSIBLE DUE TO REGULATIONS
- 1600 DOUBLE GPO @ 1600MM ABOVE FFL MOUNTED ON LAUNDRY JOINERY SIDE PANEL
- C DOUBLE GPO FLUSH MOUNTED AND CONCEALED IN UNDERSIDE OF BATHROOM CABINET
- EXT EXTERNAL GPO - WATERPROOF - @ 300MM ABOVE FFL
- DW SINGLE GPO (DISHWASHER) - LOCATED AS PER DRAWINGS
- FR SINGLE GPO (FRIDGE)@ 1700MM ABOVE FFL - LOCATED AS PER DRAWINGS
- OV OVEN - DIRECT WIRE
- RH SINGLE GPO (RANGEHOOD) - LOCATED AS PER DRAWINGS
- MW SINGLE GPO (MICROWAVE) - LOCATED AS PER DRAWINGS
- WM/DR DOUBLE GPO (WASHING MACHINE + DRYER) - LOCATED AS PER DRAWINGS
- USB GPO WITH INTEGRATED USB
- TV 300 TV AERIAL POINT @ 300MM ABOVE FFL
- TV 600 TV AERIAL POINT @ 600MM ABOVE FFL
- NTD NTD (NETWORK TERMINATION DEVICE)
- DATA INTERNET/DATA POINT - FOR WI-FI MODEM/VOIP COMPATIBLE PHONE - BY TENANT
- INT VIDEO INTERCOM
- MET ELECTRICITY METER
- SWB SWITCHBOARD
- SEC SECURITY SYSTEM HUB
- BWU BOILING WATER UNIT
- EB EXTERNAL MOTORISED ALUMINIUM VENETIAN BLIND HARDWIRED (REFER SCHEDULES FOR PRODUCT)

FOR CONSTRUCTION - 17/12/19

ISSUE	DATE	REVISION
D	17/12/19	FOR CONSTRUCTION
C	31/5/19	CONTRACT SET

This drawing to require conjunction with the architectural drawings and specification, with all project specifications and any instructions issued during the course of the contract. Contractor to check verify all dimensions on site before commencing any work. Do not scale from drawing. Figured dimensions to be taken in preference to scaled measurements.

CLIENT H.CHARALAMBOUS

Gardiner Architects
7/252 St Georges Rd, Fitzroy North, VIC, 3068
Ph: (03) 9486 4092 E: info@paulgardiner.com.au

DWG **ELECTRICAL PLAN - LEVEL 02/LEVEL 03/LEVEL 04**
PROJECT RETAIL/RESIDENTIAL DEVELOPMENT 752 HIGH STREET, THORNBURY
DRAWN BY AM
SCALE 1:100 @ A1
JOB NO 141211
DWG # A.205
REV# D

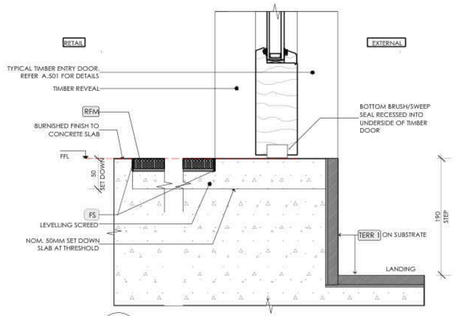

A RETAIL/ENTRY THRESHOLD
Scale: 1:5

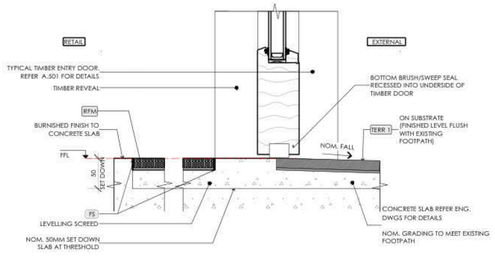

B RETAIL/ENTRY THRESHOLD
Scale: 1:5

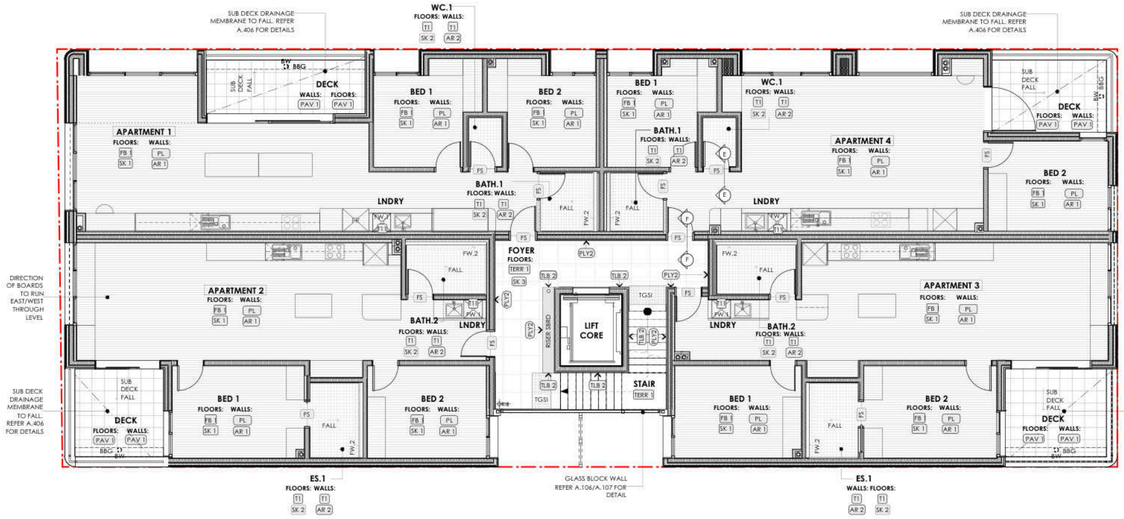

2 FINISHES PLAN - LEVEL 01
SCALE: 1:100

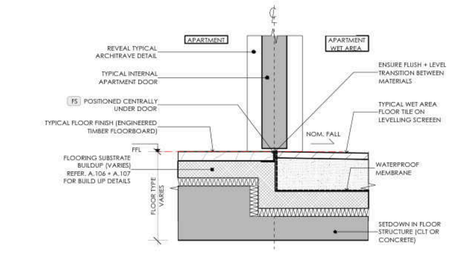

E TYPICAL APARTMENT WET AREA THREHSOLD
Scale: 1:5

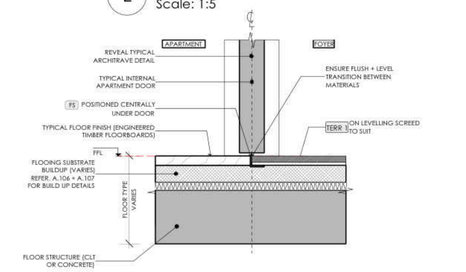

F TYPICAL APARTMENT/FOYER THREHSOLD
Scale: 1:5

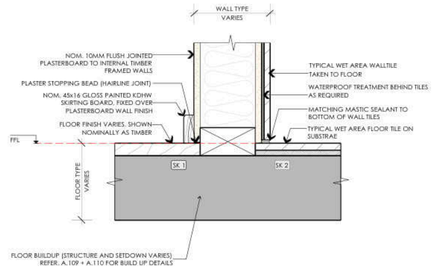

G SKIRTING TYPE 1 + 2
Scale: 1:5

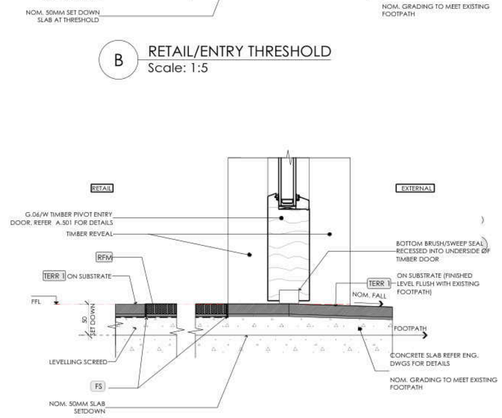

C FOYER/ENTRY THRESHOLD
Scale: 1:5

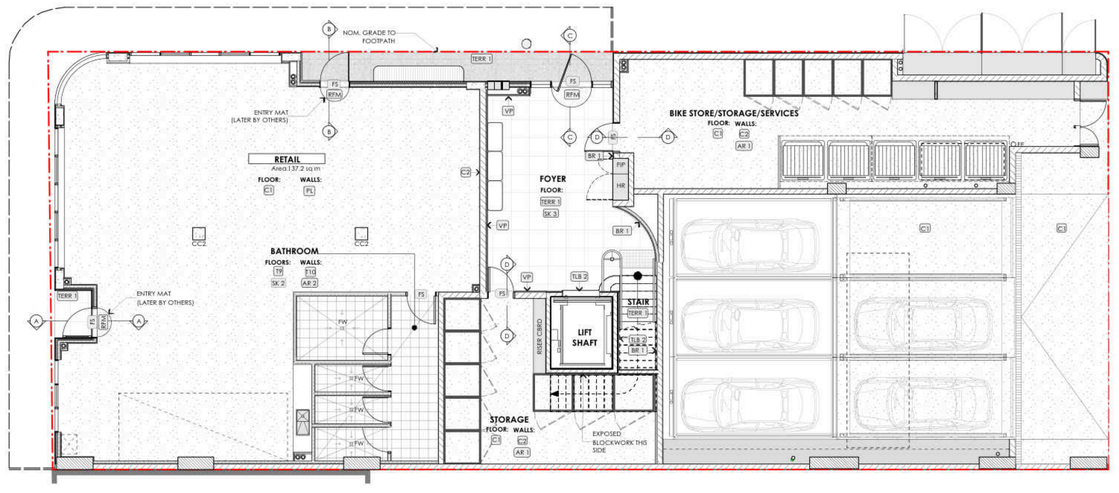

1 FINISHES PLAN - LEVEL GR
SCALE: 1:100

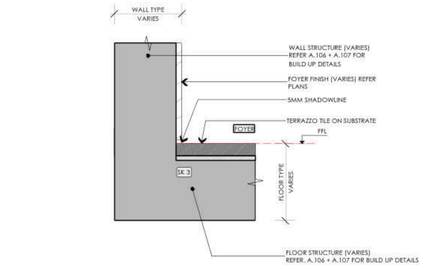

H SKIRTING TYPE 3
Scale: 1:5

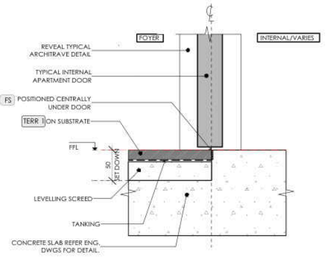

D FOYER THRESHOLD
Scale: 1:5

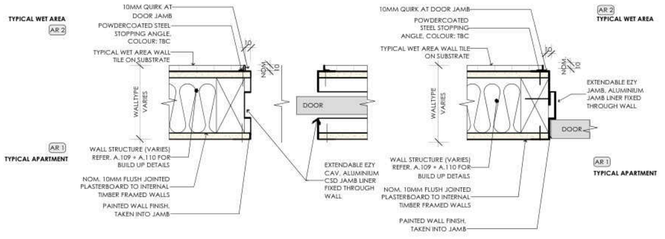

I TYPICAL ARCHITRAVE DETAILS
Scale: 1:5

FINISHES NOTES

- REFER TO SEPARATE INTERNAL FINISHES SCHEDULES FOR SPECIFIC SELECTIONS
- REFER TO FLOOR PLAN FOR FURTHER FLOOR FINISH DETAILS
- READ IN CONJUNCTION WITH PROJECT SPECIFICATION

SLIP RESISTANCE SCHEDULE

- AS PER BCA

FOYERS	P4
STAIRS	P4
PUBLIC CORRIDORS	P4
APARTMENT BATH/SHOWER	P4
RETAIL BATHROOMS	P4

REFER SCHEDULES FOR SELECTED PRODUCT INFORMATION

FINISHES LEGEND

GENERAL

FW.1	FLOOR WASTE 1	TILE INSET 1:100 FALL TO WASTE (REFER SCHEDULE FOR PRODUCT)
OUTLET SHOWN, NOM. FW.2	FLOOR WASTE 2 BATHROOM	STRIP DRAIN WITH TILE INSET LOCATE OUTLET ADJACENT SHOWER 1:100 FALL TO STRIP DRAIN (REFER SCHEDULE FOR PRODUCT)
BW	BALCONY WASTE	(REFER A.406 FOR DETAIL)
BBG	BALCONY SUB DECK BOX GUTTER	(REFER A.406 FOR DETAIL)
TGSI	TACTILE INDICATOR	(REFER SCHEDULE OF TACTILE INDICATORS FOR PRODUCT)

FLOOR FINISHES

C1	BURNISHED CONCRETE SLAB	
T1 > T11	SELECTED TILE	(REFER JOINERY DRAWINGS FOR SCOPE + SCHEDULES FOR TILE SELECTIONS)
TERR 1	SELECTED TERRAZZO STONE TILE	(REFER SCHEDULE OF FLOOR FINISHES FOR PRODUCT)
FB 1	SELECTED PREFINISHED ENGINEERED	(REFER SCHEDULE OF FLOOR FINISHES FOR PRODUCT)
FB 2	SELECTED PREFINISHED ENGINEERED	(REFER SCHEDULE OF FLOOR FINISHES FOR PRODUCT)
TC	SELECTED TIMBER DECKING	(REFER SCHEDULE OF FLOOR FINISHES FOR PRODUCT)
PAV 1	SELECTED TERACOTTA TILE	(REFER SCHEDULE OF FLOOR FINISHES FOR PRODUCT)
MG	SELECTED METAL GRATE	(REFER A.106/A.107 FOR DETAILS)
RFM	SELECTED RECESSED FLOOR MAT	(REFER SCHEDULE OF FLOOR FINISHES FOR PRODUCT)
FS	FLOOR STRIP	STEEL FLAT BAR RECESSED INTO FLOOR POWDERCOATED BLACK

FLOOR SUBSTRATES

CONC	CONCRETE (STRUCTURAL SUBSTRATE)

WALLS FINISHES

T1 > T11	SELECTED TILE	(REFER JOINERY DRAWINGS FOR SCOPE + SCHEDULES FOR TILE SELECTIONS)
C2	STRUCTURAL CONCRETE BLOCK	(REFER A.106/A.107 FOR DETAILS + SCHEDULES FOR PAINT COLOURS)
PL	WALL WITH PLASTER + PAINT FINISH	(REFER A.106/A.107 FOR DETAILS + SCHEDULES FOR PAINT COLOURS)
VP	VITRAPANEL	(REFER JOINERY DRAWINGS FOR SCOPE + REFER A.106/A.107 FOR DETAIL)
PAV 1	TERRACOTTA TILE	(REFER A.106/A.107 FOR DETAILS + SCHEDULES FOR PRODUCT)
TLB 2	INTERNAL TIMBER LINING	(REFER SCHEDULES FOR PRODUCT)
PLY2	PLYWOOD SHEET	(REFER SCHEDULE FOR PRODUCT DETAIL)
BR 1	EXTERNAL BRICK CLADDING	(REFER A.106/A.107 FOR DETAIL)

ARCHITRAVES

AR 1	ARCHITRAVE TYPE 1 PRODUCT: EZY JAMB	- GENERAL (REFER TO TYPICAL SQUARE SET JAMB DETAIL)
AR 2	ARCHITRAVE TYPE 2 PRODUCT: EZY JAMB	- TILED (REFER TO TYPICAL TILED JAMB DETAIL)

SKIRTINGS

SK 1	SKIRTING TYPE 1	- GENERAL APARTMENT (REFER A.206 FOR TYPICAL DETAIL)
SK 2	SKIRTING TYPE 2	- WET AREA TILED (REFER A.206 FOR TYPICAL DETAIL)
SK 3	SKIRTING TYPE 3	- FOYER SKIRTING (REFER A.206 FOR TYPICAL DETAIL)

FOR CONSTRUCTION - 17/12/19

ISSUE	DATE	REVISION
D	17/12/19	FOR CONSTRUCTION
C	31/5/19	CONTRACT SET

This drawing is issued in conjunction with the other architectural documents including the project specification and is the property of the author. Contractors must verify all dimensions on site before commencing any work or shop drawings. Do not scale drawing. Any discrepancies to be reported to the Architect for clarification/corrections in writing.

CLIENT H.CHARALAMBOUS

Gardiner Architects
7/252 St Georges Rd, Fitzroy North, VIC, 3068
Ph: (03) 9486 4092 E: info@paulgardiner.com.au

DWG FINISHES PLAN - BASEMENT + GROUND FLOOR
PROJECT RETAIL/RESIDENTIAL DEVELOPMENT 752 HIGH STREET, THORNBURY
DRAWN BY AM
SCALE 1:100 @ A1
JOB NO 141211
A.206
DWG # REV D

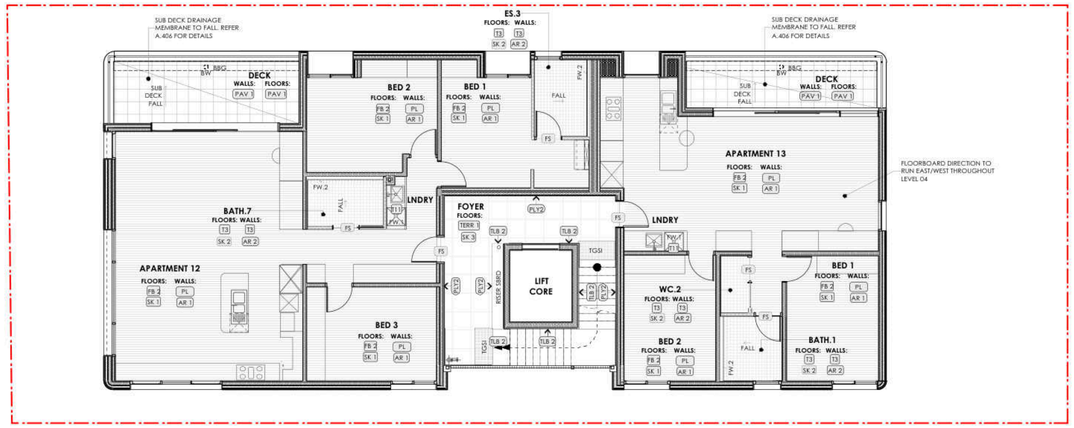

3 FINISHES PLAN - LEVEL 04
SCALE: 1:100

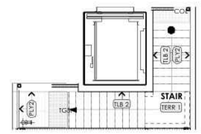

4 FINISHES PLAN - LEVEL 05
SCALE: 1:100

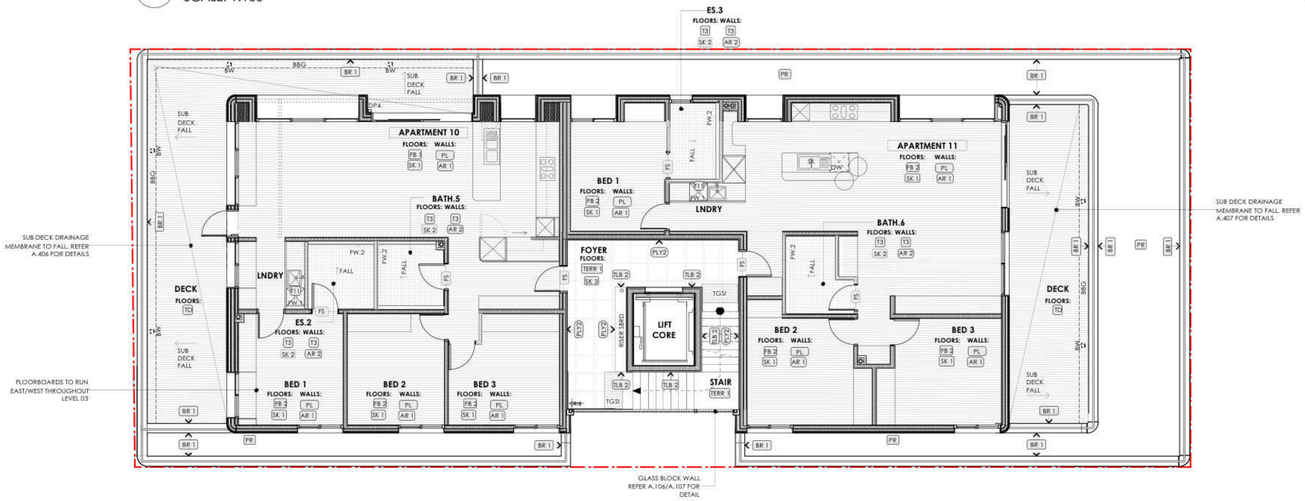

2 FINISHES PLAN - LEVEL 03
SCALE: 1:100

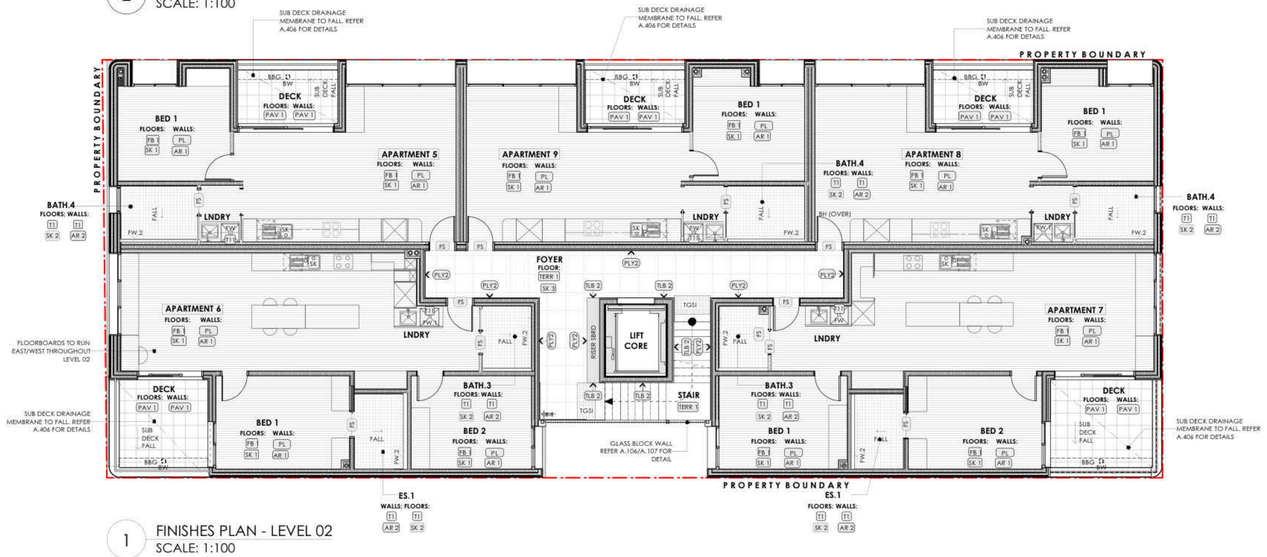

1 FINISHES PLAN - LEVEL 02
SCALE: 1:100

FINISHES NOTES

- REFER TO SEPARATE INTERNAL FINISHES SCHEDULES FOR SPECIFIC SELECTIONS
- REFER TO FLOOR PLAN FOR FURTHER FLOOR FINISH DETAILS
- READ IN CONJUNCTION WITH PROJECT SPECIFICATION

SLIP RESISTANCE SCHEDULE

- AS PER BCA

FOYERS	P4
STAIRS	P4
PUBLIC CORRIDORS	P4
APARTMENT BATH/SHOWER	P4
RETAIL BATHROOMS	P4

REFER SCHEDULES FOR SELECTED PRODUCT INFORMATION

FINISHES LEGEND

GENERAL

FW.1	FLOOR WASTE 1	TILE INSET 1:100 FALL TO WASTE (REFER SCHEDULE FOR PRODUCT)
OUTLET SHOWN, NOM.		
FW.2	FLOOR WASTE 2 BATHROOM	STRIP DRAIN WITH TILE INSET LOCATE OUTLET ADJACENT SHOWER 1:100 FALL TO STRIP DRAIN (REFER SCHEDULE FOR PRODUCT)
BW	BALCONY WASTE	(REFER A.406 FOR DETAIL)
BBG	BALCONY SUB DECK BOX GUTTER	(REFER A.406 FOR DETAIL)
TGSI	TACTILE INDICATOR	(REFER SCHEDULE OF TACTILE INDICATORS FOR PRODUCT)

FLOOR FINISHES

C1	BURNISHED CONCRETE SLAB	
T1 > T11	SELECTED TILE	(REFER JOINERY DRAWINGS FOR SCOPE + SCHEDULES FOR TILE SELECTIONS)
TERR 1	SELECTED TERRAZZO STONE TILE	(REFER SCHEDULE OF FLOOR FINISHES FOR PRODUCT)
FB.1	SELECTED PREFINISHED ENGINEERED	(REFER SCHEDULE OF FLOOR FINISHES FOR PRODUCT)
FB.2	SELECTED PREFINISHED ENGINEERED	(REFER SCHEDULE OF FLOOR FINISHES FOR PRODUCT)
TC	SELECTED TIMBER DECKING	(REFER SCHEDULE OF FLOOR FINISHES FOR PRODUCT)
PAV.1	SELECTED TERACOTTA TILE	(REFER SCHEDULE OF FLOOR FINISHES FOR PRODUCT)
MG	SELECTED METAL GRATE	(REFER A.106/A.107 FOR DETAILS)
RFM	SELECTED RECESSED FLOOR MAT	(REFER SCHEDULE OF FLOOR FINISHES FOR PRODUCT)
FS	FLOOR STRIP	STEEL FLAT BAR RECESSED INTO FLOOR POWDERCOATED BLACK

FLOOR SUBSTRATES

CONC	CONCRETE (STRUCTURAL SUBSTRATE)

WALLS FINISHES

T1 > T11	SELECTED TILE	(REFER JOINERY DRAWINGS FOR SCOPE + SCHEDULES FOR TILE SELECTIONS)
C2	STRUCTURAL CONCRETE BLOCK	(REFER A.106/A.107 FOR DETAILS + SCHEDULES FOR PAINT COLOURS)
PL	WALL WITH PLASTER + PAINT FINISH	(REFER A.106/A.107 FOR DETAILS + SCHEDULES FOR PAINT COLOURS)
VP	VITRAPANEL	(REFER JOINERY DRAWINGS FOR SCOPE + REFER A.106/A.107 FOR DETAIL)
PAV.1	TERRACOTTA TILE	(REFER A.106/A.107 FOR DETAILS + SCHEDULES FOR PRODUCT)
TLB.2	INTERNAL TIMBER LINING	(REFER SCHEDULES FOR PRODUCT)
PLY2	PLYWOOD SHEET	(REFER SCHEDULE FOR PRODUCT DETAIL)
BR.1	EXTERNAL BRICK CLADDING	(REFER A.106/A.107 FOR DETAIL)

ARCHITRAVES

AR.1	ARCHITRAVE TYPE 1 PRODUCT: EZY JAMB	- GENERAL (REFER TO TYPICAL SQUARE SET JAMB DETAIL)
AR.2	ARCHITRAVE TYPE 2 PRODUCT: EZY JAMB	- TILED (REFER TO TYPICAL TILED JAMB DETAIL)

SKIRTINGS

SK.1	SKIRTING TYPE 1	- GENERAL APARTMENT (REFER A.206 FOR TYPICAL DETAIL)
SK.2	SKIRTING TYPE 2	- WET AREA TILED (REFER A.206 FOR TYPICAL DETAIL)
SK.3	SKIRTING TYPE 3	- FOYER SKIRTING (REFER A.206 FOR TYPICAL DETAIL)

FOR CONSTRUCTION - 17/12/19

ISSUE	DATE	REVISION
D	17/12/19	FOR CONSTRUCTION
C	31/5/19	CONTRACT SET

This drawing is read in conjunction with the project specification and any instructions issued during the course of the contract. Contractor to check all dimensions on site before commencing any work. Do not scale any dimensions from drawing. Refer any discrepancies in documents.

CLIENT H.CHARALAMBOUS

Gardiner Architects
7/252 St Georges Rd, Fitzroy North, VIC 3068
Ph: (03) 9486 4092 E: info@paulgardiner.com.au

DWG FINISHES PLAN - LEVEL 01/LEVEL 02/LEVEL 03
PROJECT RETAIL/RESIDENTIAL DEVELOPMENT 752 HIGH STREET, THORNBURY
DRAWN BY AM
SCALE 1:100 @ A1
JOB NO 141211
A.207
DWG # REV# D

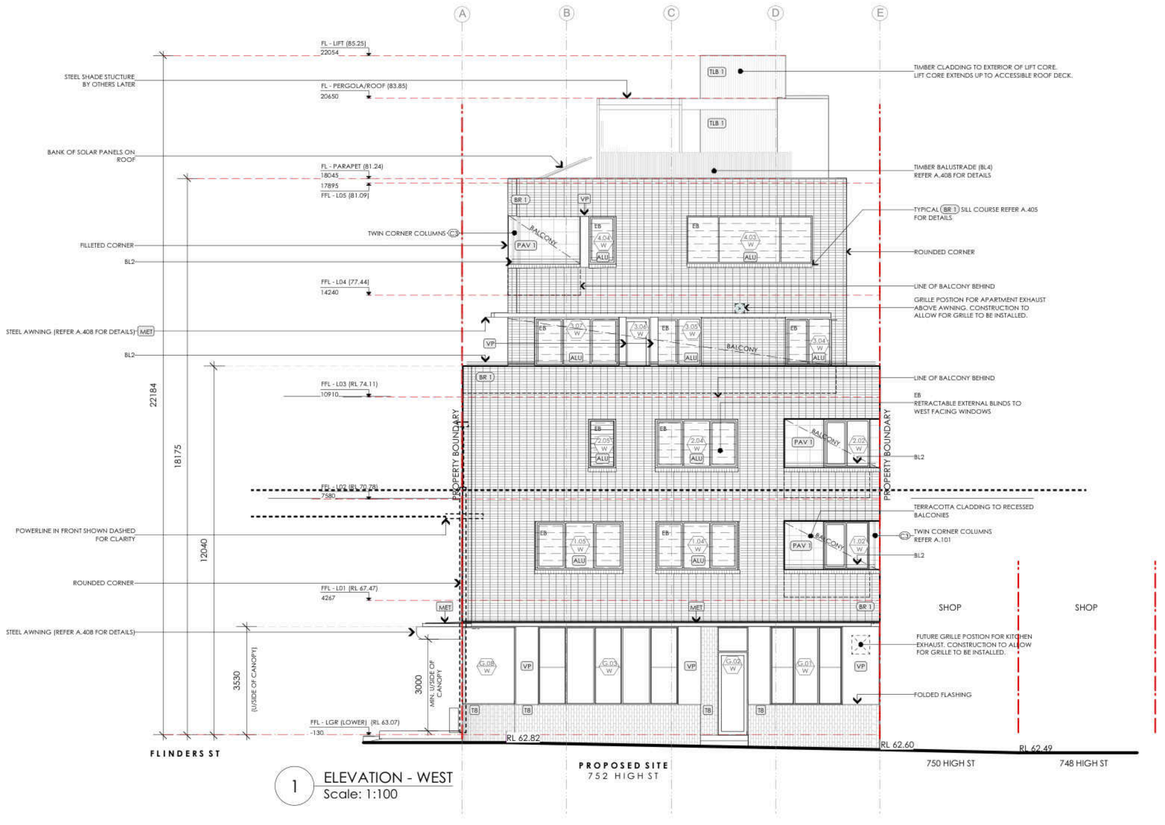

1 ELEVATION - WEST
Scale: 1:100

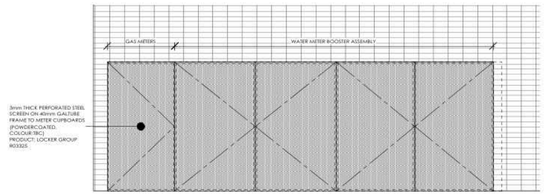

A CONCEALED WATER METER DETAIL - ELEVATION
Scale: 1:50

2 ELEVATION - NORTH
Scale: 1:100

ELEVATION NOTES

1. READ IN CONJUNCTION WITH FLOOR PLAN A.103 - A.106 FOR DIMENSIONING
2. READ IN CONJUNCTION WITH SERVICES ENG. DWGS.
3. READ IN CONJUNCTION WITH SCHEDULES FOR PRODUCT SELECTIONS AND FINISHES
4. **SUB-FLOOR VENTILATION**
   ALLOW OPEN VENTILATION TO A MINIMUM OF 2000mm² PER 1m OF WALL
5. WINDOWS + DOORS SHOWN NOMINALLY. REFER A.501-A.503 FOR DIMENSIONS

ELEVATION LEGEND

- TB — TERRAZZO TILE
  REFER SCHEDULES FOR PRODUCT
- BR 1 — BRICK FACING TILE (PGH AVANTE SYSTEM)
  REFER A.106/A.107 FOR DETAIL
- PAV 1 — TERRACOTTA TILE
  REFER A.106/A.107 FOR DETAIL
  + SCHEDULES FOR PRODUCT
- GB1 — GLASS BLOCK
  PRODUCT: GLASS BLOCK SHOP 'CLEAR'
  REFER A.106/A.107 FOR PRODUCT DETAIL
- GB2 — GLASS BLOCK
  PRODUCT: GLASS BLOCK SHOP, 'JAVA'
  REFER A.106/A.107 FOR PRODUCT DETAIL
- CB — STRUCTURAL CONCRETE BLOCK
  PAINT FINISH, COLOUR: (TBC)
- MET — SHEET METAL AWNING
  MATERIAL: STEEL
  COLOUR: POWDERCOATED, BLACK (TBC)
- PM2 — PERFORATED SHEET METAL ON STEEL TUBE FRAME SURROUND TO CARSTACKER (MATCHING CAR STACKER SLIDING DOORS)
  MATERIAL: STEEL
  COLOUR: POWDERCOATED MESH AND FRAME, BLACK (TBC)
- VP — VITRAPANEL PREFINISHED SHEET CLADDING
  REFER A.106/A.107 FOR DETAIL
  + SCHEDULES FOR PRODUCT
- EB — EXTERNAL MOTORISED ALUMINIUM VENETIAN BLIND
  (REFER A.405 FOR DETAIL + SCHEDULES FOR PRODUCT)
- PS — FIXED METAL PRIVACY SCREEN
  (REFER A.408 FOR DETAIL)
  MATERIAL: ALUMINIUM
  COLOUR: BLACK (TBC)
- ALU — ALUMINIUM WINDOW SHROUD
  MATERIAL: ALUMINIUM FLAT PLAT
  COLOUR: DARK GREY (TBC)
- TLB 1 — TIMBER LINING BOARDS
  REFER A.106 FOR DETAIL + SCHEDULES FOR PRODUCT

ELEVATION SYMBOLS LEGEND

WINDOWS
- 4.01 W — REFER A.501-A.503

DOORS
- 1.01 D — REFER A.501-A.503 + DOOR HARDWARE SCHEDULE

DIFFUSER/EXHAUST
- REFER SERVICES ENGINEER DRAWINGS FOR DETAIL

BALUSTRADES
- BL1 -DELETED-
- BL2 BALUSTRADE TYPE 2 - REFER TO A.408 BALUSTRADE DETAIL
- BL3/PS BALUSTRADE TYPE 3 (INC. PRIVACY SCREEN) - REFER TO A.408 BALUSTRADE DETAIL
- BL4 BALUSTRADE TYPE 4 - REFER TO A.408 BALUSTRADE DETAIL
- BL5 BALUSTRADE TYPE 5 - REFER TO A.408 BALUSTRADE DETAIL
- PS PRIVACY SCREEN (FIXED METAL PRIVACY SCREEN) - REFER TO A.408 FOR DETAIL

- REFER PROVISIONAL SUMM
- READ IN CONJUNCTION WITH WINDOW SCHEDULE

EB — EXTERNAL MOTORIZED RECESSED DROP DOWN ALUMINIUM VENETIAN BLIND (REFER SCHEDULES FOR PRODUCT) REFER DETAIL B/A.405

EXPOSED ROLLER BLIND ON SASH

FOR CONSTRUCTION - 17/12/19

ISSUE	DATE	REVISION
E	17/12/19	FOR CONSTRUCTION
D	25/10/19	FOR CLT SHOP DRAWING
C	31/5/19	CONTRACT SET

This drawing is to be in conjunction with the other contract documents including the specification and all other consultants drawings. Any discrepancies found in the dimensions must be reported immediately to the Architect. Contractors must verify all dimensions on site before commencing any work or shop drawings. Do not scale any dimensions from this drawing. Copyright of this drawing is vested in the Architect and must not be reproduced or used except for the purpose for which it was supplied.

CLIENT: H.CHARALAMBOUS

Gardiner Architects
77/252 St Georges Rd, Fitzroy North, VIC, 3068
Ph: (03) 94864092 E: info@paulgardiner.com.au

DWG: **ELEVATIONS - WEST & NORTH**
PROJECT: RETAIL/RESIDENTIAL DEVELOPMENT
752 HIGH STREET, THORNBURY
DRAWN BY: AM
SCALE: 1:100
JOB NO: 141211
A.301
DWG #
REV# E

10 ELEVATION - EAST
Scale: 1:100

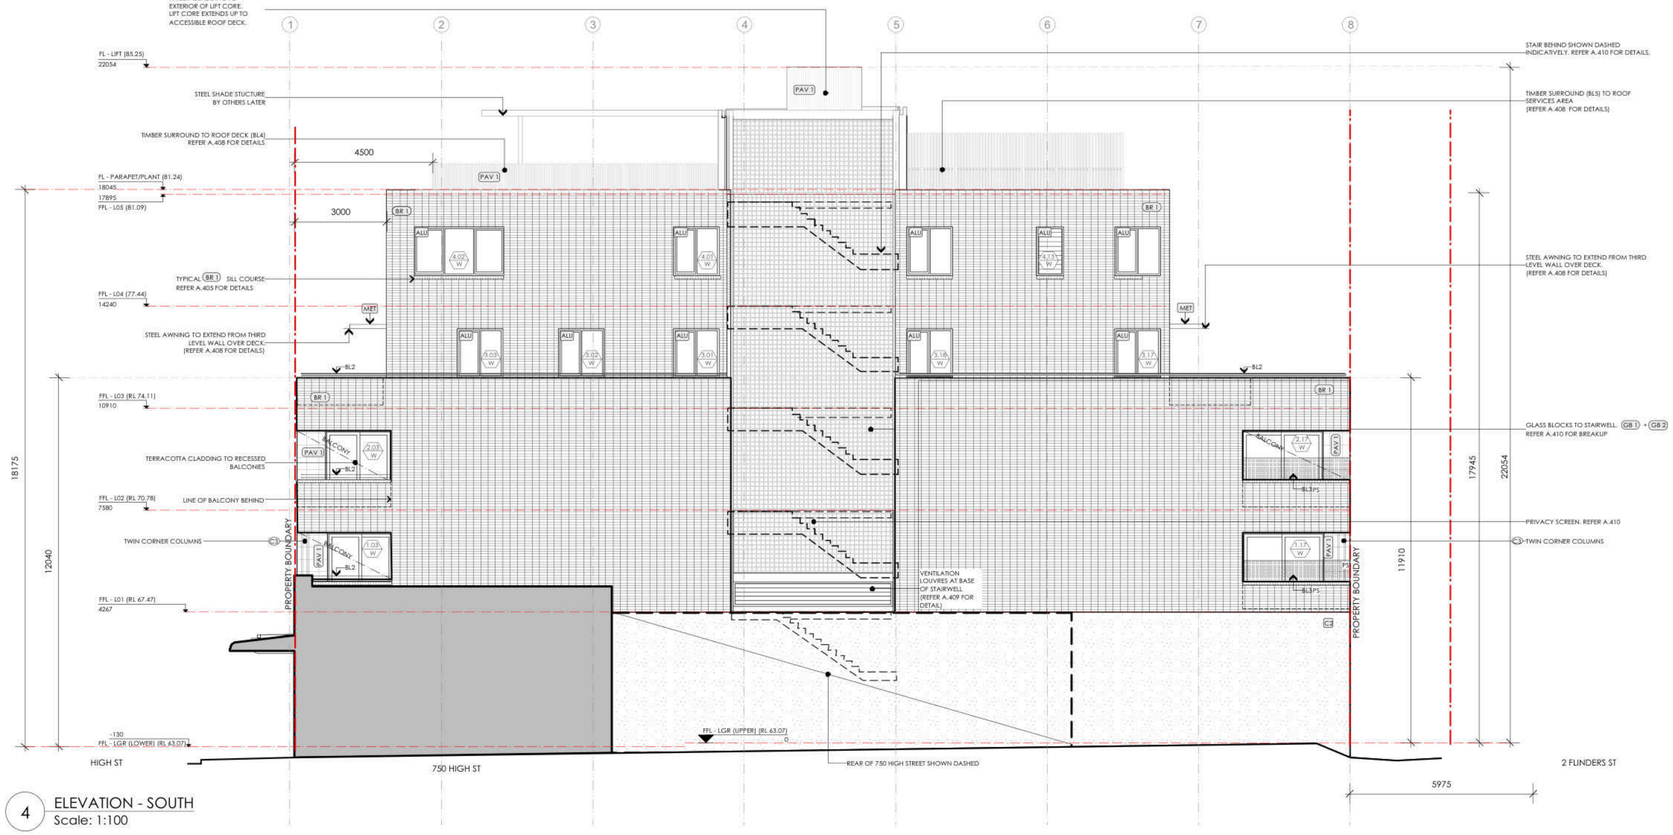

4 ELEVATION - SOUTH
Scale: 1:100

ELEVATION NOTES

1. READ IN CONJUNCTION WITH FLOOR PLAN A.103 - A.106 FOR DIMENSIONING
2. READ IN CONJUNCTION WITH SERVICES ENG. DWGS.
3. READ IN CONJUNCTION WITH SCHEDULES FOR PRODUCT SELECTIONS AND FINISHES
4. **SUB-FLOOR VENTILATION**
   ALLOW OPEN VENTILATION TO A MINIMUM OF 2000mm² PER 1m OF WALL
5. WINDOWS + DOORS SHOWN NOMINALLY. REFER A.501-A.503 FOR DIMENSIONS

ELEVATION LEGEND

- TB — TERRAZZO TILE
  REFER SCHEDULES FOR PRODUCT
- BR 1 — BRICK FACING TILE (PGH AVANTE SYSTEM)
  REFER A.106/A.107 FOR DETAIL
- PAV 1 — TERRACOTTA TILE
  REFER A.106/A.107 FOR DETAIL
  + SCHEDULES FOR PRODUCT
- GB1 — GLASS BLOCK
  PRODUCT: GLASS BLOCK SHOP, 'CLEAR'
  REFER A.106/A.107 FOR PRODUCT DETAIL
- GB2 — GLASS BLOCK
  PRODUCT: GLASS BLOCK SHOP, 'JAVA'
  REFER A.106/A.107 FOR PRODUCT DETAIL
- CC2 — STRUCTURAL CONCRETE BLOCK
  PAINT FINISH, COLOUR: (TBC)
- MET — SHEET METAL AWNING
  MATERIAL: STEEL
  COLOUR: POWDERCOATED, BLACK (TBC)
- PM2 — PERFORATED SHEET METAL ON STEEL TUBE FRAME SURROUND TO CARSTACKER (MATCHING CAR STACKER SLIDING DOORS)
  MATERIAL: STEEL
  COLOUR: POWDERCOATED MESH AND FRAME, BLACK (TBC)
- VP — VITRAPANEL PREFINISHED SHEET CLADDING
  REFER A.106/A.107 FOR DETAIL
  + SCHEDULES FOR PRODUCT
- EB — EXTERNAL MOTORISED ALUMINIUM VENETIAN BLIND
  (REFER A.405 FOR DETAIL + SCHEDULES FOR PRODUCT)
- PS — FIXED METAL PRIVACY SCREEN
  (REFER A.408 FOR DETAIL)
  MATERIAL: ALUMINIUM
  COLOUR: BLACK (TBC)
- ALU — ALUMINIUM WINDOW SHROUD
  MATERIAL: ALUMINIUM FLAT PLAT
  COLOUR: DARK GREY (TBC)
- TLB 1 — TIMBER LINING BOARDS
  REFER A.106 FOR DETAIL + SCHEDULES FOR PRODUCT

ELEVATION SYMBOLS LEGEND

WINDOWS
1.01 W — REFER A.501-A.503

DOORS
1.01 D — REFER A.501-A.503 + DOOR HARDWARE SCHEDULE

DIFFUSER/EXHAUST
- REFER SERVICES ENGINEER DRAWINGS FOR DETAIL

BALUSTRADES
- BL1 — -DELETED-
- BL2 — BALUSTRADE TYPE 2 - REFER TO A.408 BALUSTRADE DETAIL
- BL3/PS — BALUSTRADE TYPE 3 (INC. PRIVACY SCREEN) - REFER TO A.408 BALUSTRADE DETAIL
- BL4 — BALUSTRADE TYPE 4 - REFER TO A.408 BALUSTRADE DETAIL
- BL5 — BALUSTRADE TYPE 5 - REFER TO A.408 BALUSTRADE DETAIL
- PS — PRIVACY SCREEN (FIXED METAL PRIVACY SCREEN) - REFER TO A.408 FOR DETAIL

- REFER PROVISIONAL SUMM
- READ IN CONJUNCTION WITH WINDOW SCHEDULE

EB — EXTERNAL MOTORIZED RECESSED DROP DOWN ALUMINIUM VENETIAN BLIND (REFER SCHEDULES FOR PRODUCT) REFER DETAIL B/A.405

EXPOSED ROLLER BLIND ON SASH

FOR CONSTRUCTION - 17/12/19

ISSUE	DATE	REVISION
F	17/12/19	FOR CONSTRUCTION
E	4/11/19	FOR CLT SHOP DRAWING
D	23/10/19	FOR CLT SHOP DRAWING
C	31/5/19	CONTRACT SET

This drawing to read in conjunction with the other contract documents forming the project specification and any instructions issued during the course of the contract. Contractor to verify all dimensions on site before commencing any work. Do not scale from drawing. Report any errors or omissions in documents.

CLIENT H.CHARALAMBOUS

Gardiner Architects
7/252 St Georges Rd, Fitzroy North, VIC. 3068
Ph: (03) 94864092 E: info@paulgardiner.com.au

DWG ELEVATIONS EAST & SOUTH
PROJECT RETAIL/RESIDENTIAL DEVELOPMENT
752 HIGH STREET, THORNBURY
DRAWN BY AM
SCALE 1:100 @ A1
JOB NO 141211
A.302
DWG #
REV# F

SECTION NOTES

1. READ IN CONJUNCTION WITH SPECIFICATION
2. READ IN CONJUNCTION WITH STRUCTURAL ENGINEERS DWG - REFER COVER PAGE FOR REFERENCES
3. REFER TO GEOTECHNICAL REPORT BY GEOAUST - REFER COVER PAGE FOR REFERENCES
4. ALL FRAMING TO BE IN ACCORDANCE WITH THE "LIGHT TIMBER FRAMING CODE"
5. **BRACKETS, CLEATS, ETC.** PROVIDE ALL MINOR CLEATS AND BRACKETS AS REQUIRED FOR CONNECTING BEAMS, PLATES & THE LIKE.
6. **BULDUPS** REFER A.106 + 107 FOR TYPICAL WALL + FLOOR BUILDUPS CEILING BULKHEADS SHOWN NOM. REFER RCPS FOR SCOPE
7. **LEGEND**
FFL = FINISHED FLOOR LEVEL
FCL = FINISHED CEILING LEVEL
FSL = FINISHED STRUCTURAL LEVEL
FL = FINISHED LEVEL

ELEVATION LEGEND

BR 1 BRICK FACING TILE (PGH AVANTE SYSTEM) REFER A.106/A.107 FOR DETAIL

PAV 1 TERRACOTTA TILE REFER A.106/A.107 FOR DETAIL + SCHEDULES FOR PRODUCT

TLB 1 TIMBER LINING BOARDS REFER A.106 FOR DETAIL + SCHEDULES FOR PRODUCT

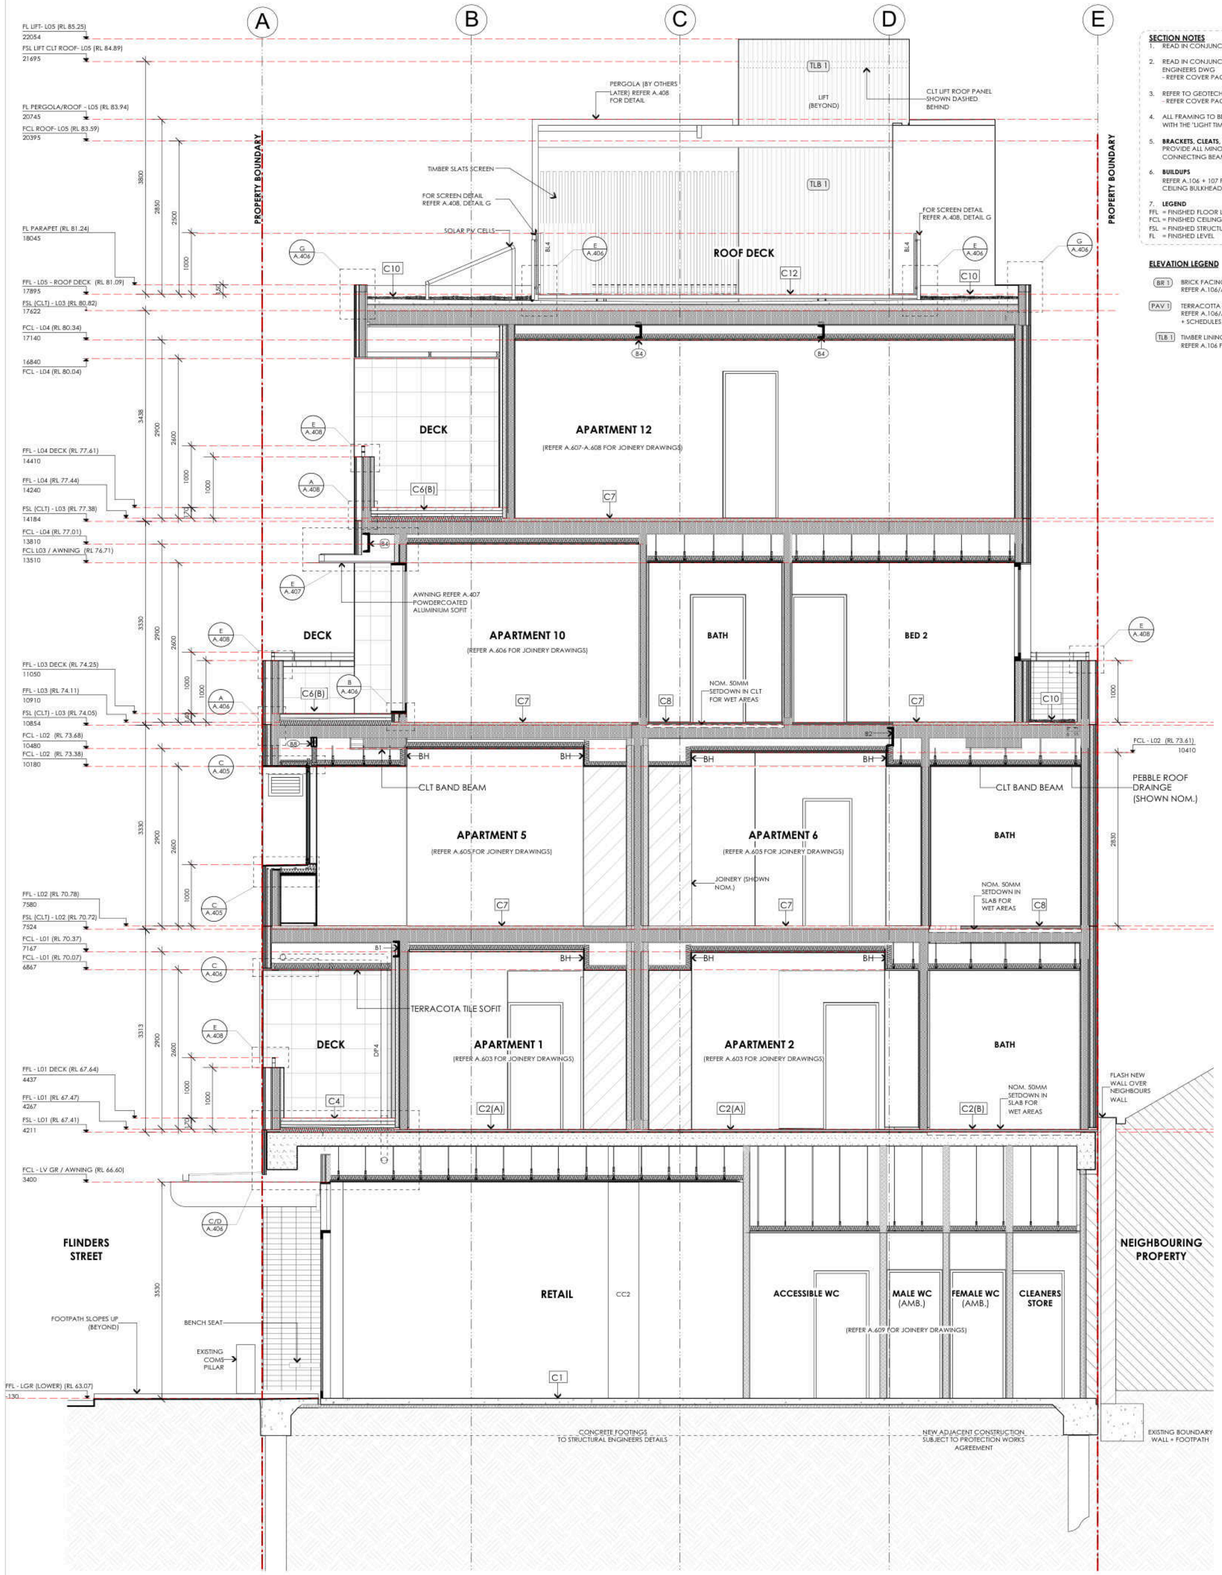

1 SECTION A:A
Scale: 1:50

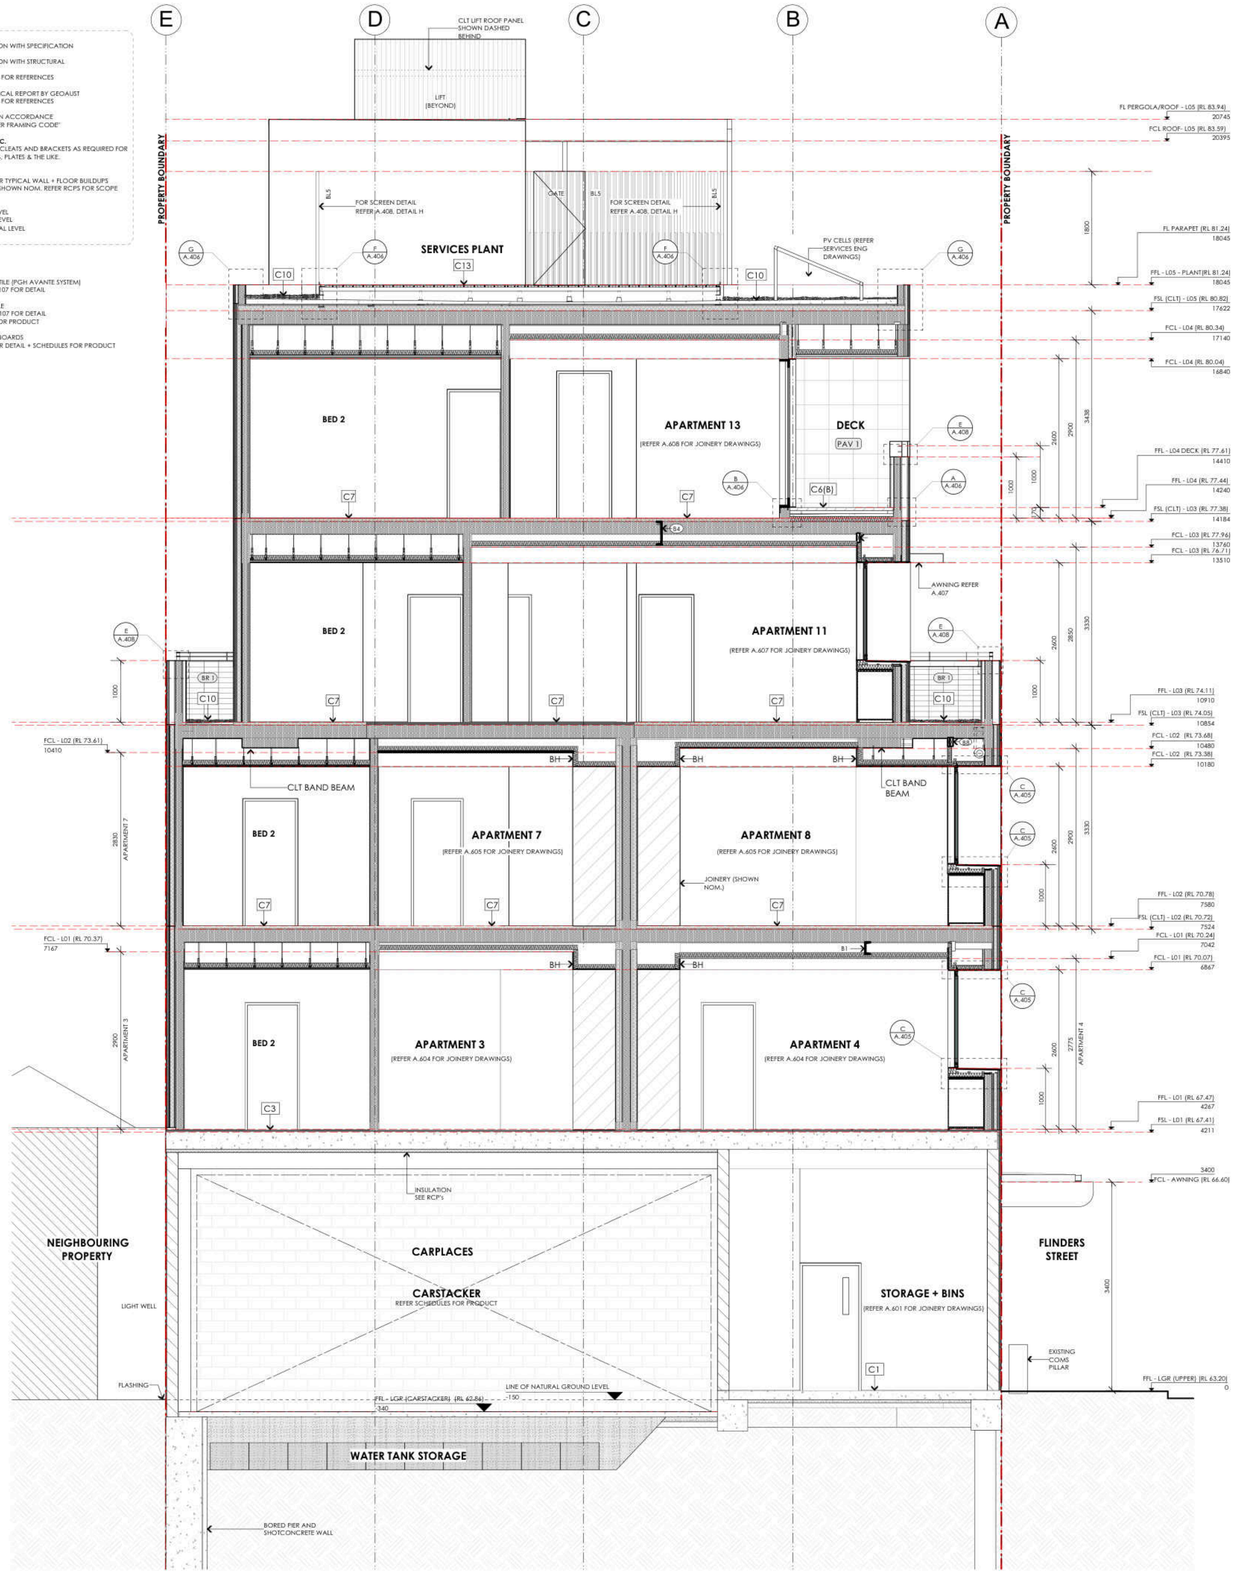

2 SECTION B:B
Scale: 1:50

FOR CONSTRUCTION - 17/12/19

ISSUE	DATE	REVISION
F	17/12/19	FOR CONSTRUCTION
E	23/10/19	FOR CLT SHOP DRAWING
D	6/6/19	EARLY WORKS PERMIT (CONSTRUCTION ISSUE)
C	31/5/19	CONTRACT SET

This drawing to be read in conjunction with the project specification and any instructions issued during the course of the contract. Verify all dimensions on site before commencing any work. Do not scale any dimensions from drawing. Refer any discrepancies to the Architect.

CLIENT H.CHARALAMBOUS

Gardiner Architects
7/252 St Georges Rd, Fitzroy North, VIC 3068
Ph: (03) 9486 4092, E: info@paulgardiner.com.au

DWG: **SECTIONS - PROPOSED**

PROJECT: RETAIL/RESIDENTIAL DEVELOPMENT
752 HIGH STREET, THORNBURY

DRAWN BY: AM
SCALE: 1:100 @ A1

JOB NO: 141211
A.401
DWG #
REV# F

SECTION NOTES

1. READ IN CONJUNCTION WITH SPECIFICATION
2. READ IN CONJUNCTION WITH STRUCTURAL ENGINEERS DWG - REFER COVER PAGE FOR REFERENCES
3. REFER TO GEOTECHNICAL REPORT BY GEOAUST - REFER COVER PAGE FOR REFERENCES
4. ALL FRAMING TO BE IN ACCORDANCE WITH THE 'LIGHT TIMBER FRAMING CODE'
5. **BRACKETS, CLEATS, ETC.** PROVIDE ALL MINOR CLEATS AND BRACKETS AS REQUIRED FOR CONNECTING BEAMS, PLATES & THE LIKE.
6. **BULDUPS** REFER A.106 + 107 FOR TYPICAL WALL + FLOOR BUILDUPS CEILING BULKHEADS SHOWN NOM. REFER RCPS FOR SCOPE
7. **LEGEND** FFL = FINISHED FLOOR LEVEL FCL = FINISHED CEILING LEVEL FSL = FINISHED STRUCTURAL LEVEL FL = FINISHED LEVEL

ELEVATION LEGEND

BR 1 BRICK FACING TILE (PGH AVANTE SYSTEM) REFER A.106/A.107 FOR DETAIL

PAV 1 TERRACOTTA TILE REFER A.106/A.107 FOR DETAIL + SCHEDULES FOR PRODUCT

TLB 1 TIMBER LINING BOARDS REFER A.106 FOR DETAIL + SCHEDULES FOR PRODUCT

FFL - L05 - PLANT(RL 81.24) 18045

CLT LIFT ROOF PANEL SHOWN DASHED BEHIND

LIFT (BEYOND)

PERGOLA (BY OTHERS LATER) REFER A.408 FOR DETAIL

FOR SCREEN DETAIL REFER A.408/H

OPEN UNDER

SHW COLLECTORS (REFER SERVICES DRAWINGS FOR DETAILS

SOLAR PV PANELS (REFER SERVICES DRAWINGS FOR DETAILS

PEBBLE ROOF

PROPERTY BOUNDARY

FFL - L04 DECK (RL 77.61) 14410

FFL - L04 (RL 77.44) 14240

FCL - L03 (RL 77.94) 13790 13510

FCL - L03/AWNING (RL 76.71)

DECK

APARTMENT 13 (REFER A.608 FOR JOINERY DRAWINGS)

BATH

BED 1

APARTMENT 12 (REFER A.608 FOR JOINERY DRAWINGS)

NOM. 50MM SETDOWN IN CLT FOR WET AREAS

APARTMENT 11 (REFER A.607 FOR JOINERY DRAWINGS)

APARTMENT 10 (REFER A.606 FOR JOINERY DRAWINGS)

BALCONY DRAINGE (SHOWN NOM.)

APARTMENT 8 (REFER A.605 FOR JOINERY DRAWINGS)

APARTMENT 9 (REFER A.605 FOR JOINERY DRAWINGS)

APARTMENT 5 (REFER A.605 FOR JOINERY DRAWINGS)

APARTMENT 4 (REFER A.604 FOR JOINERY DRAWINGS)

WC

BED 2

APARTMENT 1 (REFER A.603 FOR JOINERY DRAWINGS)

REFER STRUCTURAL ENGINEERS DRAWING FOR REINFORCED CONCRETE

STORAGE + BINS (REFER A.601 FOR JOINERY DRAWINGS)

FOYER

RETAIL

HIGH STREET

LANEWAY

RUN FINISH DOWN TO FOOTPATH

FFL - LGR (UPPER) (RL 63.2)

FFL - LGR (LOWER) (RL 63.07)

RL 62.82

RL 62.78

RL 62.66

FL LIFT- L05 (RL 85.25) 22054

FSL LIFT CLT ROOF- L05 (RL 84.89) 21695

FL PERGOLA/ROOF - L05 (RL 83.94) 20745

FCL ROOF- L05 (RL 83.59) 20395

FL PARAPET (RL 81.24) 18045

17895

FFL - L05 - ROOF DECK (RL 8

FSL (CLT) - L05 (RL 80.82) 17622

FCL - L04 (RL 80.34) 17140

FCL - L04 (RL 80.04) 16840

FFL - L04 DECK (RL 77.61) 14410

FFL - L04 (RL 77.44) 14240

FSL (CLT) - L03 (RL 77.38) 14184

FCL - L03 (RL 77.94) 13810

FCL - L03/AWNING (RL 76.71) 13510

11090

FFL - L03 DECK (RL 74.25)

FFL - L03 (RL 74.11) 10910

FSL (CLT) - L03 (RL 74.05) 10854

FCL - L02 (RL 73.68) 10480

FCL - L02 (RL 73.38) 10180

FFL - L02 (RL 70.78) 7580

FSL (CLT) - L02 (RL 70.72) 7524

FCL - L01 (RL 70.37) 7167

FCL - L01 (RL 70.07) 6867

FFL - L01 DECK (RL 67.64) 4437

FFL - L01 (RL 67.47) 4267

FSL - L01 (RL 67.41) 4211

3400

FCL GR / AWNING (RL 66.60)

1 SECTION C:C
Scale: 1:50

FOR CONSTRUCTION - 17/12/19

F	17/12/19	FOR CONSTRUCTION
E	23/10/19	FOR CLT SHOP DRAWING
D	6/6/19	EARLY WORKS PERMIT (CONSTRUCTION ISSUE) - 06/06/19
C	31/5/19	CONTRACT SET
ISS'E	DATE	REVISION

This drawing to require conjection with the architectural documentation and the project specification and any instructions issued during the course of the contract. Contractor must verify all dimensions on site before commencing any work. Do not scale from this drawing unless drawing is issue for full planning process or documents.

CLIENT H.CHARALAMBOUS

Gardiner Architects
7/252 St Georges Rd, Fitzroy North, VIC, 3068
Ph: (03) 9486 4092 E: info@paulgardiner.com.au

DWG **SECTIONS - PROPOSED**

PROJECT RETAIL/RESIDENTIAL DEVELOPMENT 752 HIGH STREET, THORNBURY

DRAWN BY AM

SCALE 1:100 @ A1

JOB NO 141211

DWG # A.402

REV# F

1 2 3 4 5 6 7 8

FL LIFT- LO5 (RL 85.25) 22054
FSL LIFT CLT ROOF- LO5 (RL 84.89) 21695
FL PERGOLA/ROOF - LO5 (RL 83.94) 20745
FL PARAPET (RL 81.24) 18045
FFL - LO5 - ROOF DECK (RL 81.09) 17895
FSL (CLT) - LO3 (RL 80.82) 17622
FCL - LO4 (RL 80.34) 17140
16840
FCL - LO4 (RL 80.04)
FFL - LO4 (RL 77.44) 14240
FSL (CLT) - LO4 (RL 77.38) 14184
13510
FCL - LO3/AWNING (RL 76.71)
FFL - LO3 DECK (RL 74.25) 11050
FFL - LO3 (RL 74.11) 10910
FSL (CLT) - LO3 (RL 74.05) 10854
FCL - LO2 (RL 73.38) 10180
FFL - LO2 DECK (RL 70.95) 7750
FFL - LO2 (RL 70.78) 7580
FSL (CLT) - LO2 (RL 70.72) 7524
FCL - LO1 (RL 70.07) 6867
FFL - LO1 DECK (RL 67.64) 4437
FFL - LO1 (RL 67.47) 4267
FSL - LO1 (RL 67.41) 4211
FCL - LV GR / AWNING (RL 66.60) 3400
FFL - LGR (LOWER) (RL 63.07) -130
RL 62.59

3800 2850 1050 3438 2900 2600 1000 3330 2600 2460 1000 3330 2600 2460 1000 3313 2600 1000 1000 3550

PROPERTY BOUNDARY

CLT LIFT ROOF PANEL SHOWN DASHED BEHIND
LIFT (BEYOND)
PERGOLA (BY OTHERS (LATER) REFER A.408 FOR DETAIL
FOR SCREEN DETAIL REFER A.408, DETAIL G
FOR SCREEN DETAIL REFER A.408, DETAIL H

DINING/KITCHEN
APARTMENT 12
(REFER A.608 FOR JOINERY DRAWINGS)
BED 3
BED 1
BATH
NOM. 50MM SETDOWN IN CLT FOR WET AREAS
APARTMENT 13
BED 2
(REFER A.608 FOR JOINERY DRAWINGS)

DECK
BED 1
APARTMENT 10
(REFER A.606 FOR JOINERY DRAWINGS)
BED 2
BED 3

GLASS BLOCK WALL
(REFER A.409 FOR STAIRWELL WALL DETAILS)

APARTMENT 6
(REFER A.605 FOR JOINERY DRAWINGS)
APARTMENT 7
(REFER A.605 FOR JOINERY DRAWINGS)

APARTMENT 2
(REFER A.603 FOR JOINERY DRAWINGS)
APARTMENT 3
(REFER A.603 FOR JOINERY DRAWINGS)

VENTILATION LOUVRES AT BASE OF STAIRWELL (REFER A.409 FOR DETAIL)

HIGH STREET
RETAIL
CC2
CLEANERS STORE
(REFER A.601 FOR JOINERY DRAWINGS)
RESIDENT STORAGE
(REFER A.601 FOR JOINERY DRAWINGS)

CARSTACKER
REFER SCHEDULE FOR PRODUCT
RAMP TO CARSTACKER TO COMPLY WITH PRODUCT SPECIFICATION, MAX 3% (1.72 DEG) DOWN
RAMP TO CARSTACKER TO COMPLY WITH PRODUCT SPECIFICATION, MAX 5% (2.86 DEG. DOWN) UP
ADJUST LEVEL OF LANE AS REQUIRED.
FFL - LGR (CARSTACKER) (RL 62.86)
-340
FFL - LGR (RL 60.86)
-2340
VERTICAL DPC
BORED PIER
REFER STRUCTURAL ENGINEERS DRAWINGS FOR ALL CONCRETE WALLS
TANKED CAR STACKER PIT - REFER STRUCTURAL AND CIVIL DRAWINGS

FFL - LO5 - PLANT(RL 81.24) 18045
FCL LO3 / AWNING (RL 76.71) 13510

2NO. EXPOSED DOWNPIPES, PAINTED
R2.0 GLASSWOOL + CEMENT SHEET TO UNDERSIDE OF CONCRETE SLAB
PERFORATED STEEL SCREEN ON GALTUBE FRAM ABOVE CARSTACKER GATE
LANEWAY

SECTION NOTES
1. READ IN CONJUNCTION WITH SPECIFICATION
2. READ IN CONJUNCTION WITH STRUCTURAL ENGINEERS DWG - REFER COVER PAGE FOR REFERENCES
3. REFER TO GEOTECHNICAL REPORT BY GEOAUST - REFER COVER PAGE FOR REFERENCES
4. ALL FRAMING TO BE IN ACCORDANCE WITH THE 'LIGHT TIMBER FRAMING CODE'
5. **BRACKETS, CLEATS, ETC.** PROVIDE ALL MINOR CLEATS AND BRACKETS AS REQUIRED FOR CONNECTING BEAMS, PLATES & THE LIKE.
6. **BULDUPS** REFER A.106 + 107 FOR TYPICAL WALL + FLOOR BULDUPS CEILING BULKHEADS SHOWN NOM. REFER RCPS FOR SCOPE
7. **LEGEND**
FFL = FINISHED FLOOR LEVEL
FCL = FINISHED CEILING LEVEL
FSL = FINISHED STRUCTURAL LEVEL
FL = FINISHED LEVEL

ELEVATION LEGEND
BR 1 BRICK FACING TILE (PGH AVANTE SYSTEM) REFER A.106/A.107 FOR DETAIL
PAV 1 TERRACOTTA TILE REFER A.106/A.107 FOR DETAIL + SCHEDULES FOR PRODUCT
TLB 1 TIMBER LINING BOARDS REFER A.106 FOR DETAIL + SCHEDULES FOR PRODUCT

5 SECTION C:C
Scale: 1:50

FOR CONSTRUCTION - 17/12/19

ISSUE	DATE	REVISION
F	17/12/19	FOR CONSTRUCTION
E	23/10/19	FOR CLT SHOP DRAWING
D	6/6/19	EARLY WORKS PERMIT (CONSTRUCTION ISSUE)
C	31/5/19	CONTRACT SET

This drawing to be read in conjuction with the other contract documents including the specification. Builder to verify all dimensions prior to starting the works of the contract. Contractor to verify all dimensions on site before commencing any shop drawings. Do not scale any dimensions from drawings. Advise Architect of all discrepancies in documents.

CLIENT H.CHARALAMBOUS
Gardiner Architects
77252 1 Georges Rd Fitzroy North, VIC. 3068
Ph: (03) 9486 4092 E: info@paulgardiner.com.au

DWG **SECTIONS - PROPOSED**
PROJECT RETAIL/RESIDENTIAL DEVELOPMENT
752 HIGH STREET, THORNBURY
DRAWN BY AM
SCALE 1:100 @ A1
JOB NO 141211
A.403
DWG # REV# F

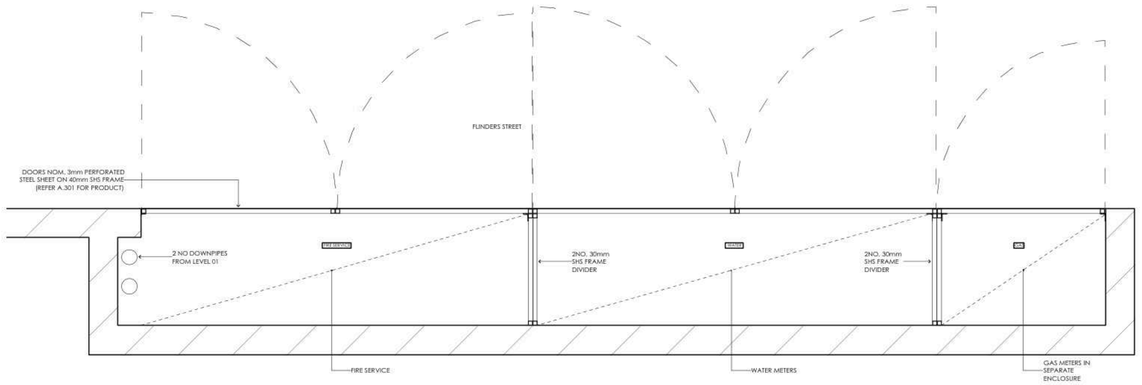

4 FIRE/WATER/GAS CBRD REFER ELEVATION A.601
Scale: 1:20

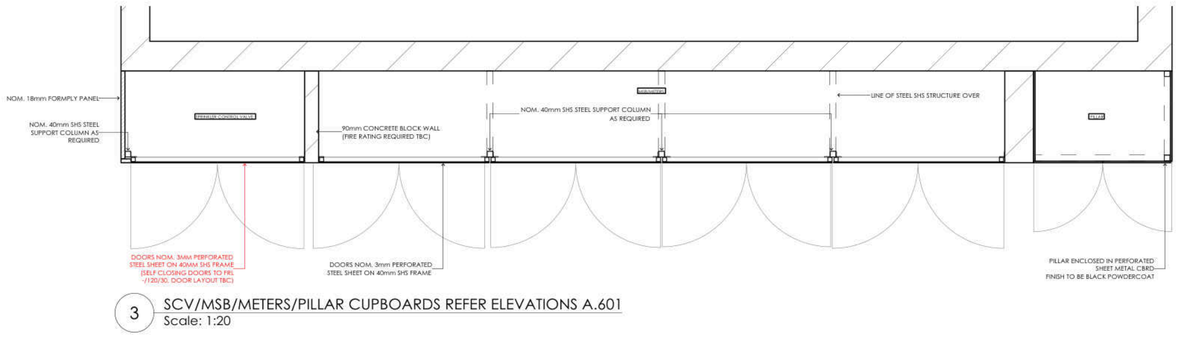

3 SCV/MSB/METERS/PILLAR CUPBOARDS REFER ELEVATIONS A.601
Scale: 1:20

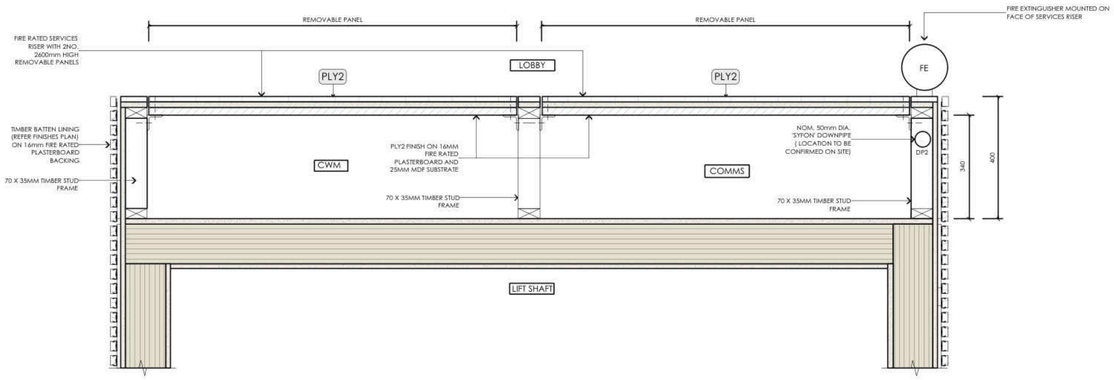

1 SERVICE RISER TYPICAL FIRE RATED. REFER ELEVATIONS A.601
Scale: 1:10

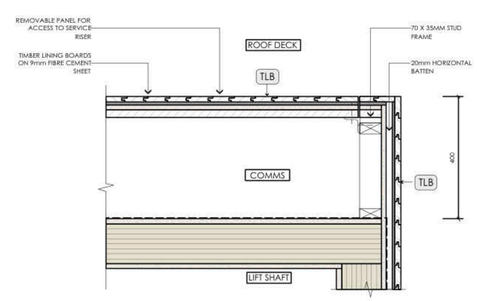

2 SERVICE RISER ROOF DECK
Scale: 1:10

FOR CONSTRUCTION - 17/12/19

ISSUE	DATE	REVISION
D	17/12/19	FOR CONSTRUCTION
C	31/5/19	CONTRACT SET

This drawing to read in conjunction with the relevant consultants drawings, engineers drawings, project specification and any instructions issued during the course of the contract. Contractor to check all dimensions on site before commencing any work. Do not scale any dimensions from drawings. Refer any discrepancies in documents.

CLIENT H.CHARALAMBOUS

Gardiner Architects
77252 St Georges Rd Fitzroy North, VIC 3068
Ph: (03) 9486 4092 E: info@paulgardiner.com.au

DWG **DETAILS - SERVICES RISER + METER CUPBOARDS**
PROJECT RETAIL/RESIDENTIAL DEVELOPMENT
752 HIGH STREET, THORNBURY
JOB NO 141211
DRAWN BY AM
SCALE 1:100
DWG # A.404
REV# D

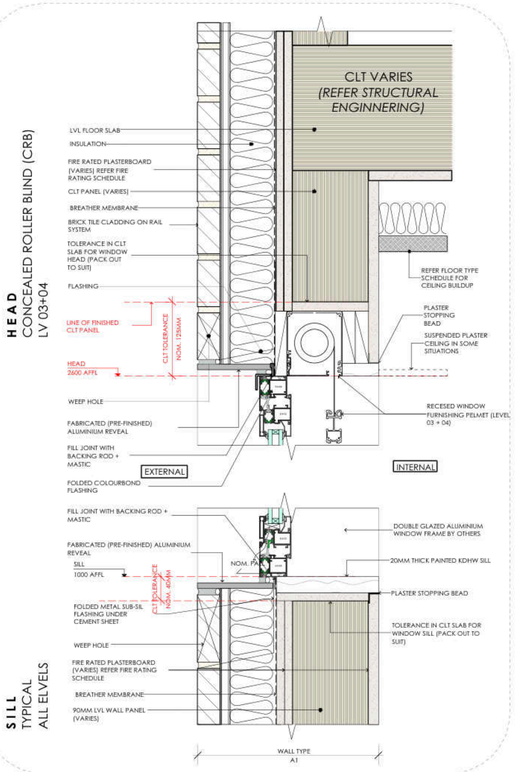

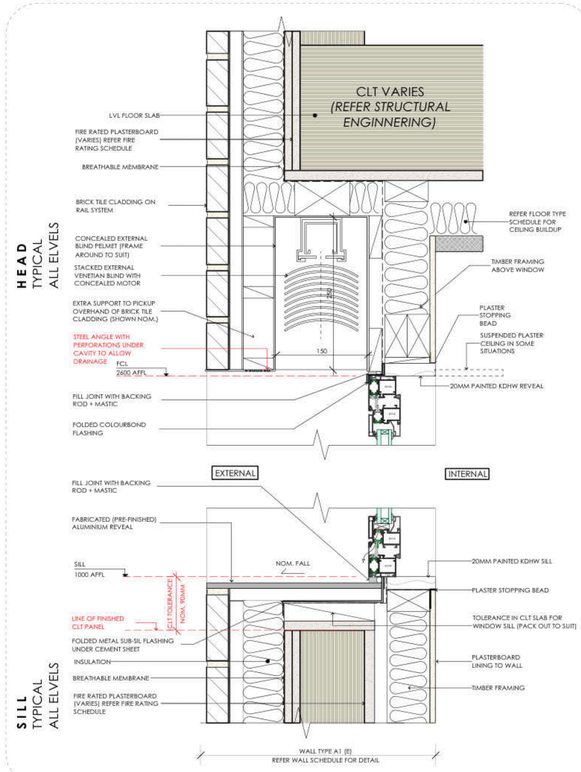

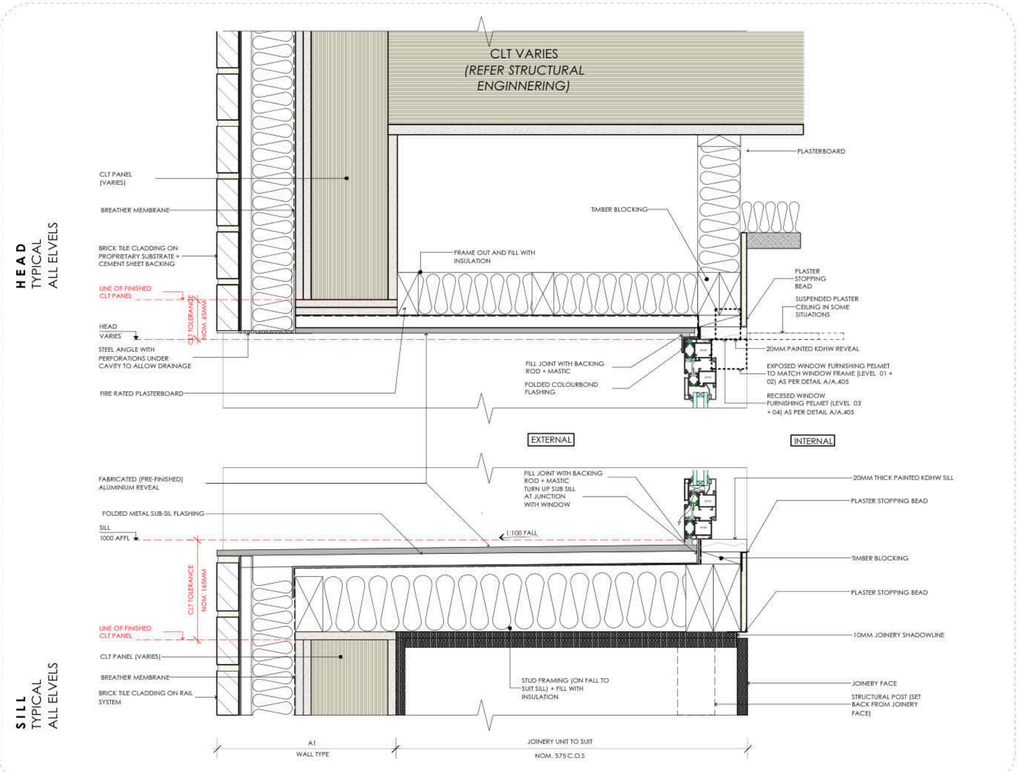

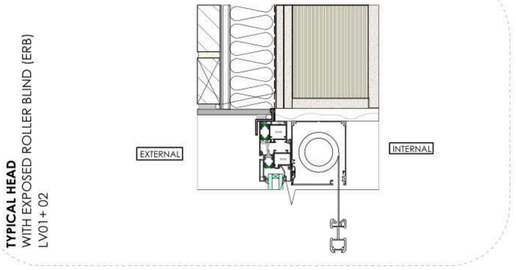

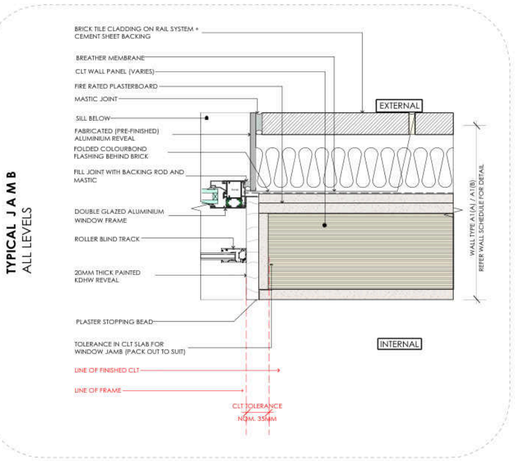

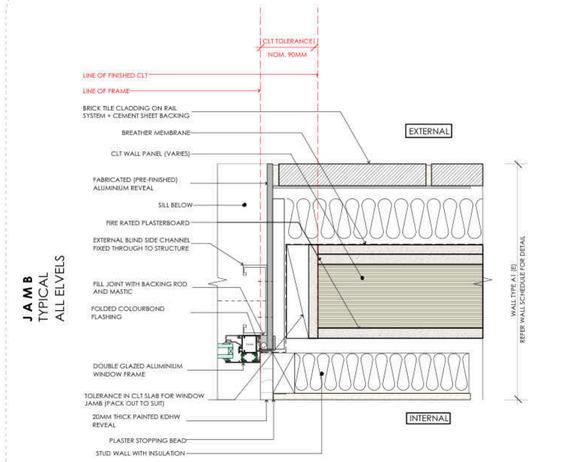

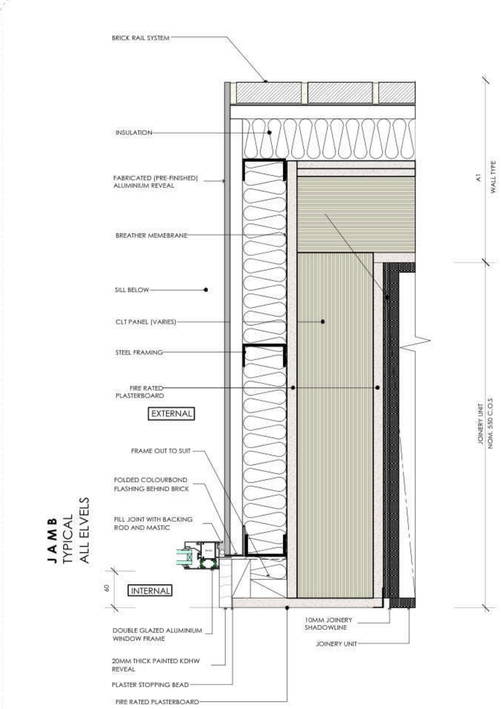

A A.405 TYPICAL WINDOW DETAIL (STANDARD)
SCALE: 1:5

B A.405 TYPICAL WINDOW DETAIL (EXTERNAL BLIND)
SCALE: 1:5

C A.405 TYPICAL WINDOW DETAIL (DEEP REVEAL)
SCALE: 1:5

FOR CONSTRUCTION - 17/12/19

This drawing is to be read in conjunction with the relevant consultants drawings and the project specification and any instructions issued during the course of the contract. Verify all dimensions on site and report errors before commencing the work. Do not scale any dimensions from drawings. All setout to be confirmed on site prior to fabrication.

ISSUE	DATE	REVISION
D	17/12/19	FOR CONSTRUCTION
C	31/5/19	CONTRACT SET

CLIENT CHALLEN

Gardiner Architects
77/252 St Georges Rd, Fitzroy North, VIC, 3068
Ph: (03) 9486 4092 E: info@paulgardiner.com.au

DWG DETAILS - TYPICAL WINDOW DETAILS
PROJECT RETAIL/RESIDENTIAL DEVELOPMENT
752 HIGH STREET, THORNBURY

JOB NO 141211
DRAWN BY AM
SCALE 1:100
DWG # A.405
REV# D

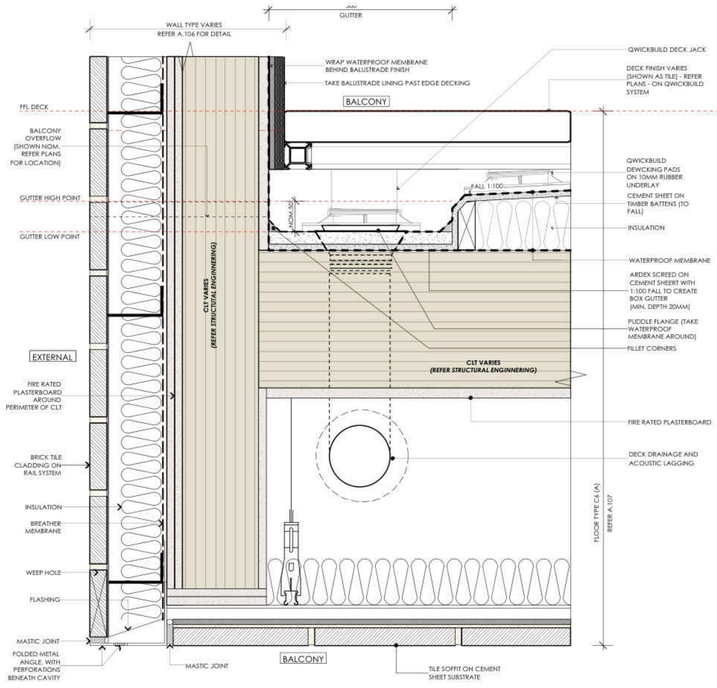

A A.406 TYPICAL DECK/BALUSTRADE JUNCTION (CLT) - LV 02/03/04
Scale: 1:5

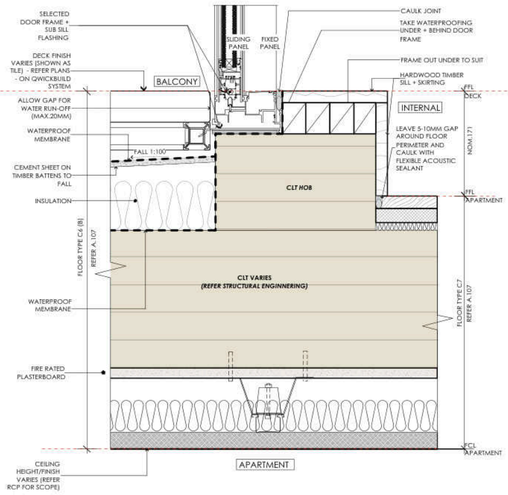

B A.406 TYPICAL DECK THRESHOLD (CLT) - LV 02/03/04
SCALE: 1:5

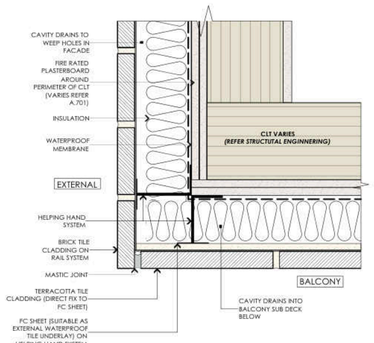

I A.406 TYPICAL JAMB DETAIL BALCONY & EXT WALL (CLT) - LV 01/02/03/04
Scale: 1:5

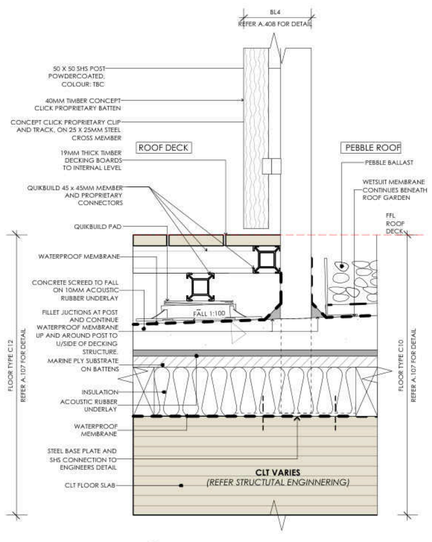

E A.406 TYPICALROOF DECK/BL4 JUNCTION
SCALE: 1:5

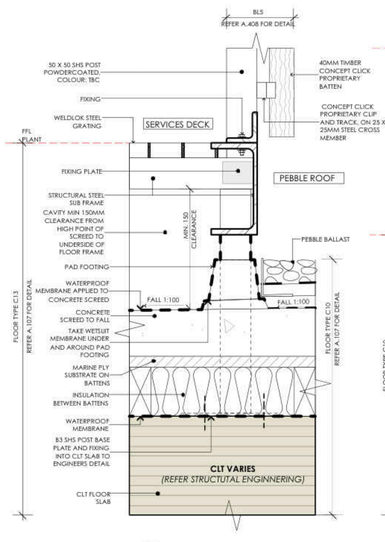

F A.406 TYPICAL PLANT/BL5 JUNCTION
SCALE: 1:5

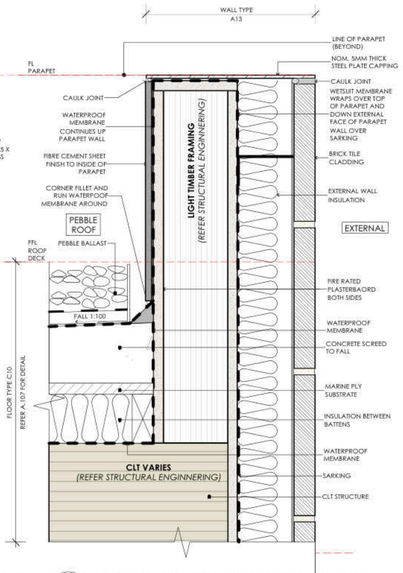

G A.406 TYPICAL LV 05 ROOF DECK PARAPET
SCALE: 1:5

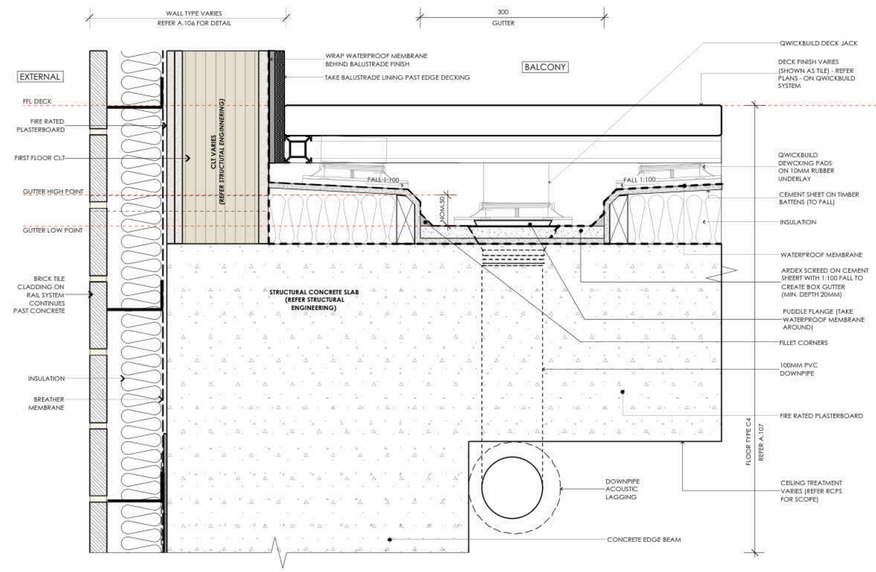

C A.406 TYPICAL DECK/BALUSTRADE JUNCTION (CONCRETE) - LV 01
Scale: 1:5

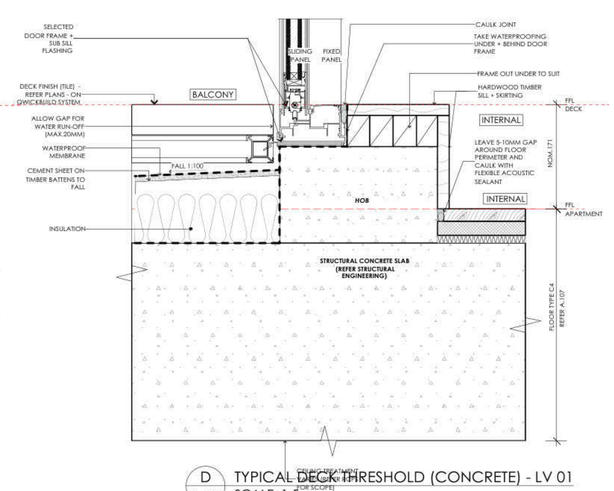

D A.406 TYPICAL DECK THRESHOLD (CONCRETE) - LV 01
SCALE: 1:5

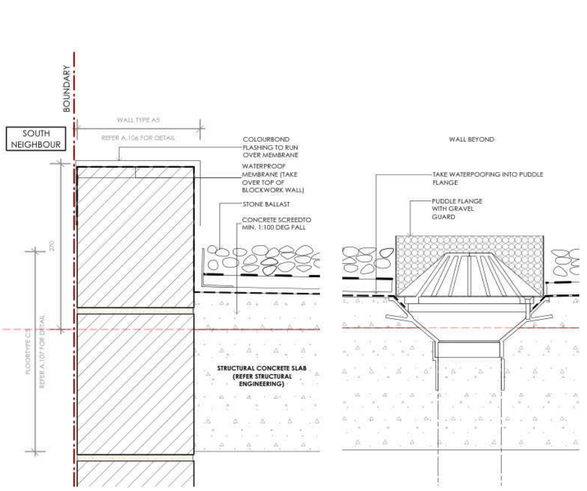

H A.406 FIRST FLOOR PEBBLE ROOF
Scale: 1:5

ISSUE	DATE	REVISION
D	17/12/19	FOR CONSTRUCTION
C	31/5/19	CONTRACT SET

This drawing is to be read in conjection with the relevant architectural drawings, engineers drawings, project specification and any instruction issued during the course of the contract. Contractor to check all dimensions on site before commencing any work. Do not scale any dimensions from this drawing. Any discrepancies or omissions to be reported immediately.

FOR CONSTRUCTION - 17/12/19

CLIENT H.CHARALAMBOUS

Gardiner Architects
77/252 St Georges Rd, Fitzroy North, VIC. 3068
Ph: (03) 9486 4092 E: info@paulgardiner.com.au

DWG DETAILS - TYPICAL BALCONY + ROOF DETAILS
PROJECT RETAIL/RESIDENTIAL DEVELOPMENT
752 HIGH STREET, THORNBURY

JOB NO 141211
DRAWN BY AM
SCALE 1:100
A.406
DWG # REVE D

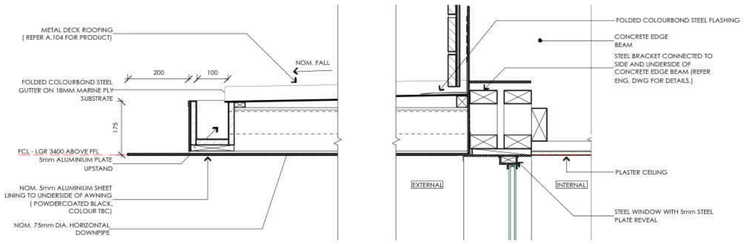

A SECTION DETAIL - AWNING TYPE 1 (TYPICAL)
Scale: 1:10

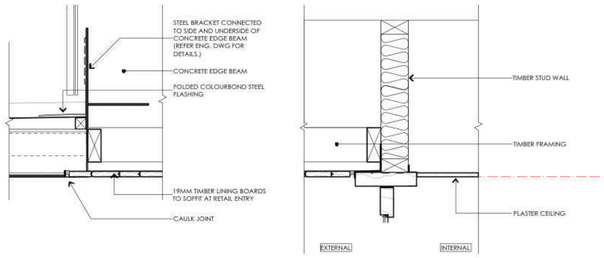

B SECTION DETAIL - AWNING TYPE 1
Scale: 1:10

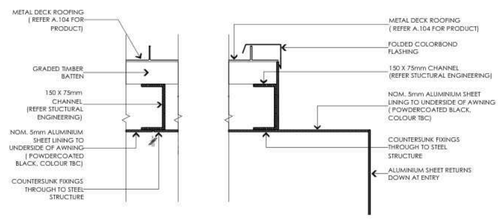

C SECTION DETAIL - AWNING TYPE 1
Scale: 1:10

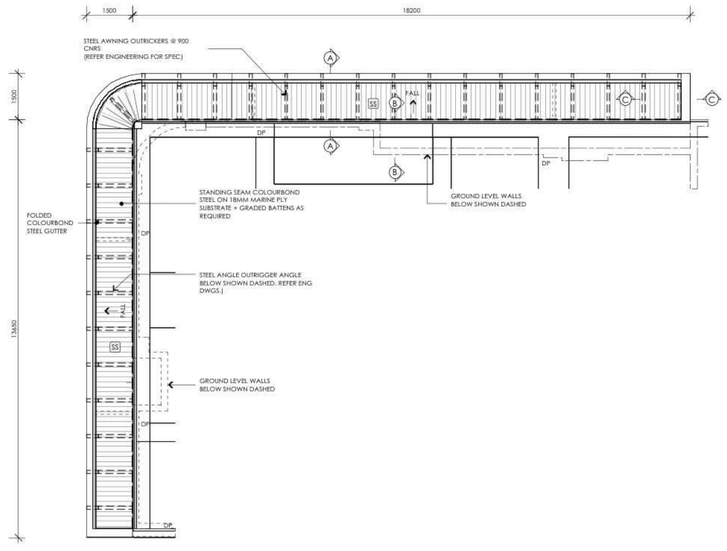

1 PLAN - AWNING TYPE 1
Scale: 1:100

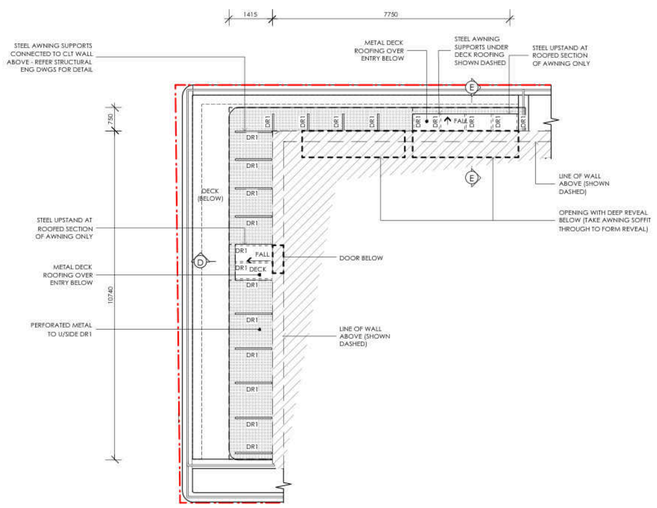

2 PLAN - AWNING TYPE 2
Scale: 1:100

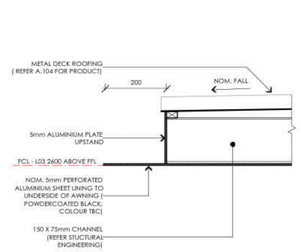

D SECTION DETAIL - AWNING TYPE 2
Scale: 1:10

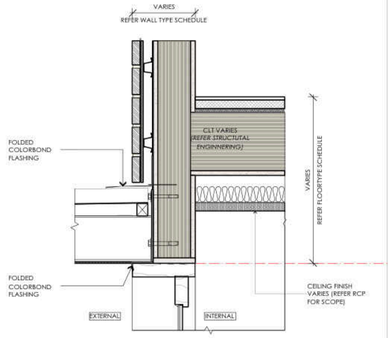

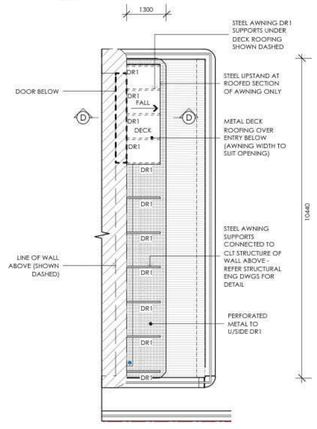

3 PLAN - AWNING TYPE 2 (APARTMENT 11)
Scale: 1:100

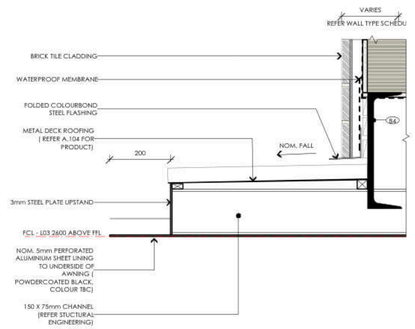

E SECTION DETAIL - AWNING TYPE 2
Scale: 1:10

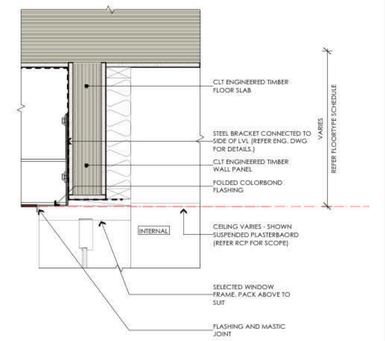

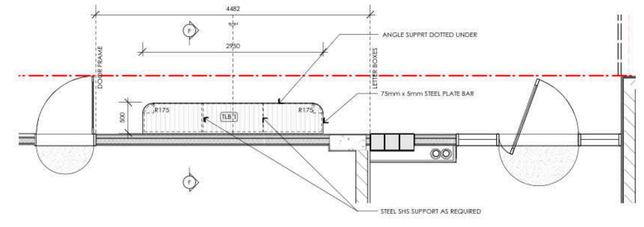

4 SECTION - EXTERNAL BENCH
Scale: 1:50

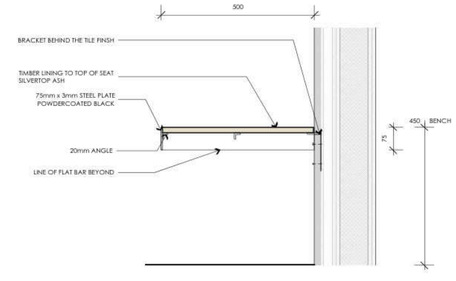

F SECTION DETAIL - EXTERNAL BENCH
Scale: 1:10

FOR CONSTRUCTION - 17/12/19

This drawing is to be in conjunction with the other contract documents including the specification and any addenda issued during the course of the contract. Contractors must verify all dimensions on site before commencing any work. Do not scale any dimensions from drawings. Advise Architect of all discrepancies or omissions.

ISSUE	DATE	REVISION
D	17/12/19	FOR CONSTRUCTION
C	31/5/19	CONTRACT SET

CLIENT: H.CHARALAMBOUS

Gardiner Architects
7/252 St Georges Rd, Fitzroy North, VIC, 3068
Ph: (03) 9486 4092 E: info@paulgardiner.com.au

DWG: **DETAILS - AWNINGS (LEVEL GR + 3)**
PROJECT: RETAIL/RESIDENTIAL DEVELOPMENT
752 HIGH STREET, THORNBURY
JOB NO. 141211
DRAWN BY AM
SCALE AS SHOWN
DWG # A.407
REV # D

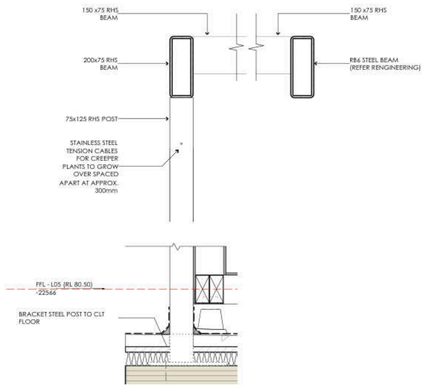

A SECTION - AWNING TYPE 4
Scale: 1:10

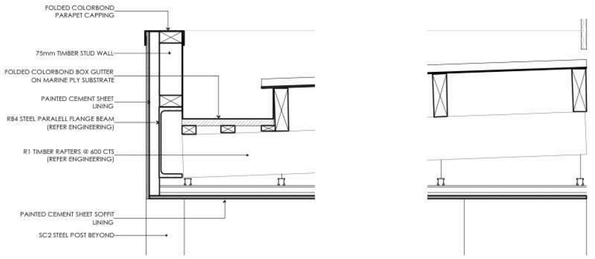

B SECTION - AWNING TYPE 4
Scale: 1:10

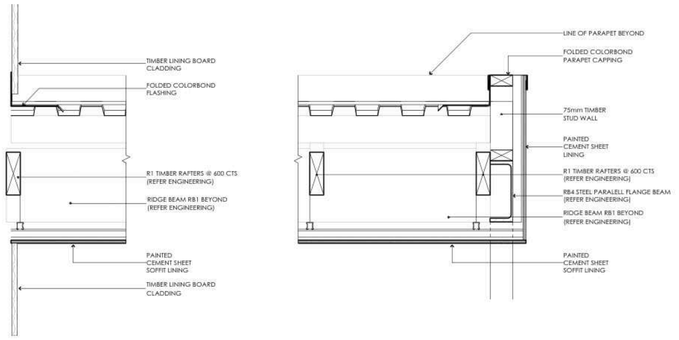

C SECTION - AWNING TYPE 4
Scale: 1:10

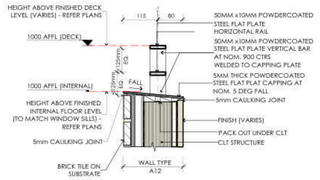

2 BALUSTRADE (BL2) - DETAIL
Scale: 1:10

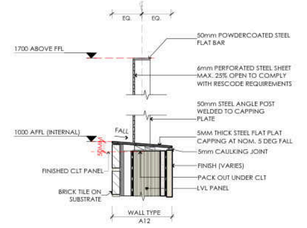

3 BALUSTRADE (BL3) - DETAIL
SCALE: 1:10

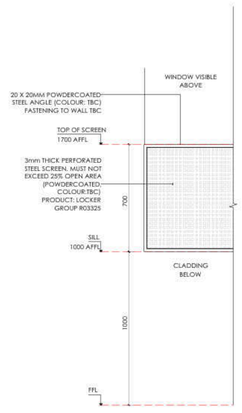

D PRIVACY SCREEN (PS) - ELEVATION DETAIL
Scale: 1:20

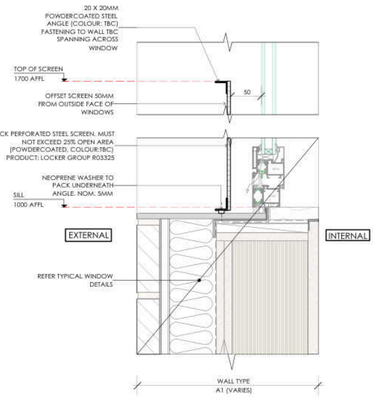

E PRIVACY SCREEN (PS) - SECTION DETAIL
Scale: 1:5

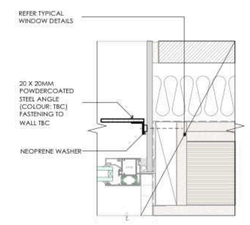

F PRIVACY SCREEN (PS) - JAMB DETAIL
Scale: 1:5

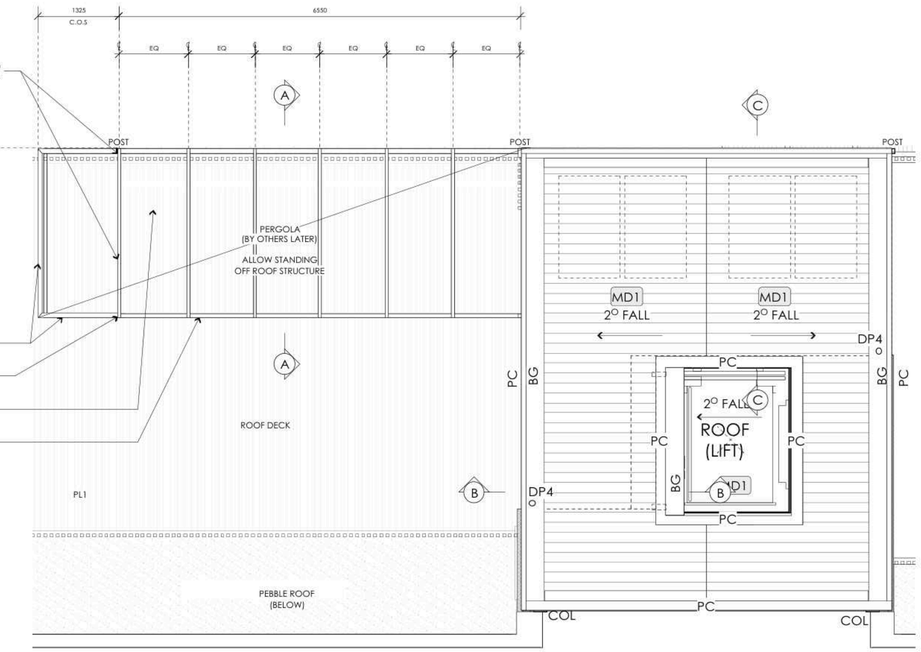

1 PLAN - ROOF DECK SHADE STRUCTURE + ROOF
Scale: 1:50

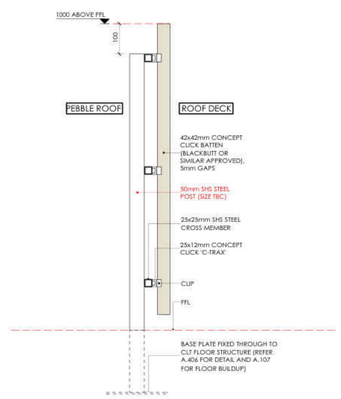

G BALUSTRADE (BL4) - DETAIL
Scale: 1:10

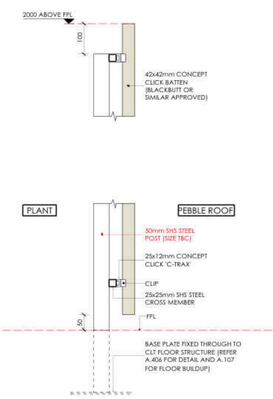

H BALUSTRADE (BL5) - DETAIL
Scale: 1:10

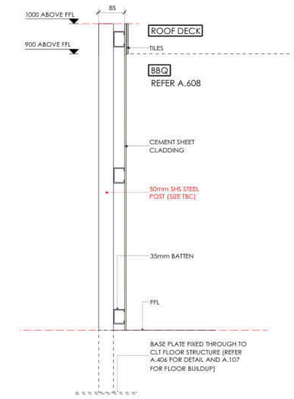

I BALUSTRADE (BL6) - DETAIL
Scale: 1:10

FOR CONSTRUCTION - 17/12/19

ISSUE	DATE	REVISION
D	17/12/19	FOR CONSTRUCTION
C	31/5/19	CONTRACT SET

This drawing to be read in conjection with the relevant consultant drawings, engineers drawings, project specification and any instruction issued during the course of the contract. Contractor to check all dimensions on site before commencing any work. Do not scale any dimensions from drawings. Report any discrepancies in dimensions.

CLIENT H.CHARALAMBOUS

Gardiner Architects
77252 St George's Rd, Fitzroy North, VIC. 3068
Ph: (03) 94864092 E: info@paulgardiner.com.au

DWG DETAILS - LEVEL 05 SHADE STRUCTURE + ROOF
PROJECT RETAIL/RESIDENTIAL DEVELOPMENT 752 HIGH STREET, THORNBURY
DRAWN BY AM
SCALE AS SHOWN
JOB NO 141211
A.408
DWG #
REV# D

ELEVATION LEGEND

GB1 GLASS BLOCK
PRODUCT: GLASS BLOCK SHOP:'CLEAR'
REFER A.106/A.107 FOR PRODUCT DETAIL

GB2 GLASS BLOCK
PRODUCT: GLASS BLOCK SHOP: 'JAVA'
REFER A.106/A.107 FOR PRODUCT DETAIL

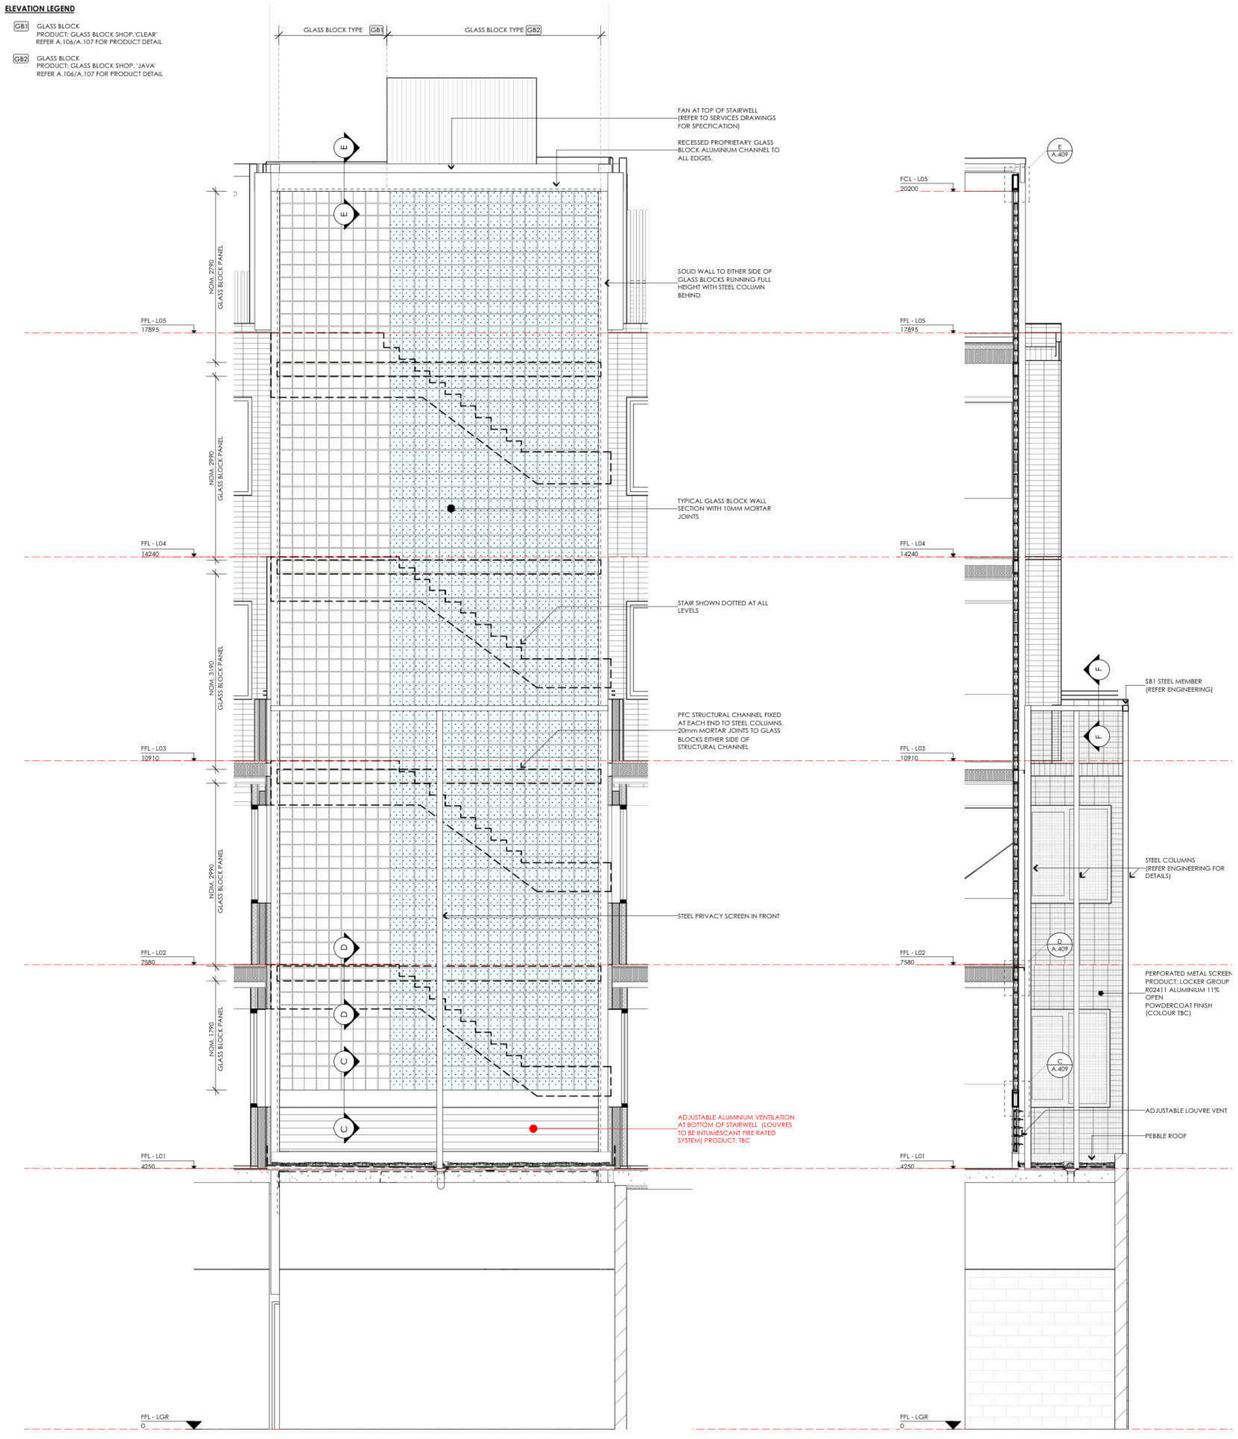

A SECTION A
Scale: 1:50

B SECTION B
Scale: 1:50

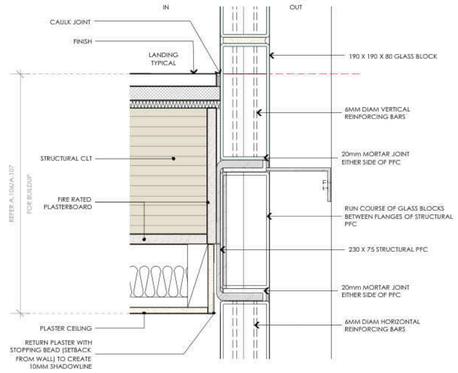

D DETAIL - GLASS BLOCK + STAIR LANDING JUNCTION
Scale: 1:5

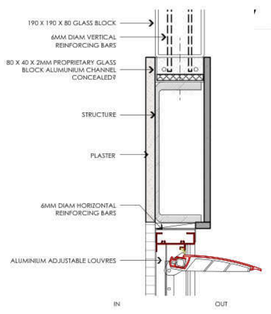

C DETAIL - GLASS BLOCK
Scale: 1:5

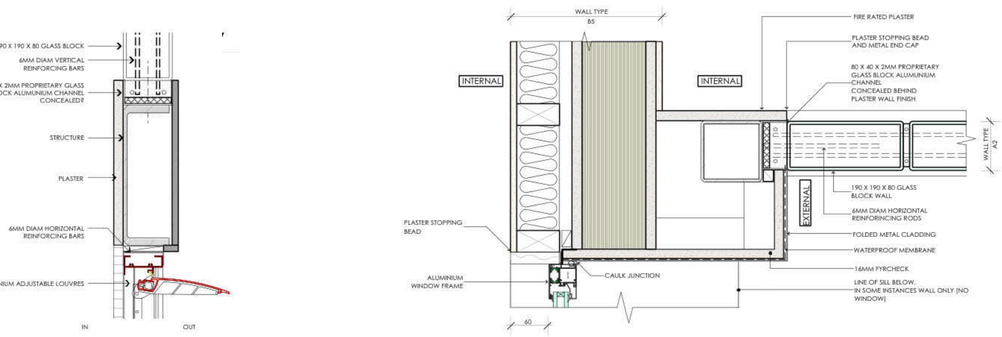

G DETAIL (PLAN) - GLASS BLOCK
Scale: 1:5

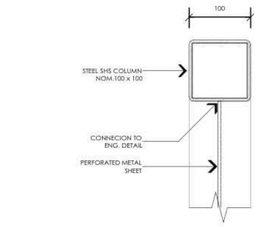

F DETAIL - PRIVACY SCREEN
Scale: 1:5

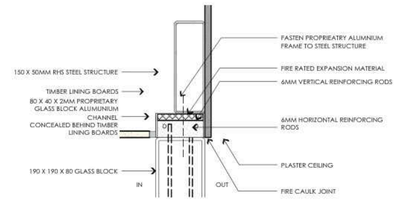

E DETAIL - GLASS BLOCK
Scale: 1:5

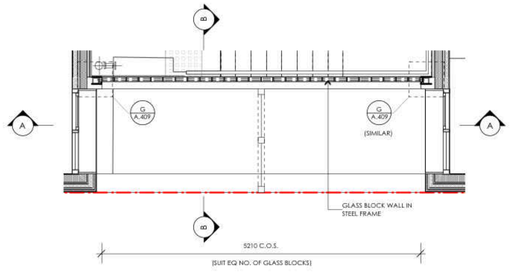

1 FLOOR PLAN - LEVEL 01
Scale: 1:50

This drawing is read in conjuction with the project specification and any subsequent addenda and any instructions issued during the course of the contract. Contractor to verify all dimensions on site before commencing any work. Do not scale any dimensions from drawing. Refer any discrepancies in documents.

ISSUE	DATE	REVISION
D	17/12/19	FOR CONSTRUCTION
C	31/5/19	CONTRACT SET

FOR CONSTRUCTION - 17/12/19

CLIENT H.CHARALAMBOUS

Gardiner Architects
7/252 St George's Rd, Fitzroy North, VIC 3068
Ph: (03) 9486 4092, E: info@paulgardiner.com.au

DWG **DETAILS - GLASS BLOCK WALL**
PROJECT RETAIL/RESIDENTIAL DEVELOPMENT
752 HIGH STREET, THORNBURY

JOB NO 141211
DRAWN BY AM
SCALE AS SHOWN
A.409
DWG #
REV# D

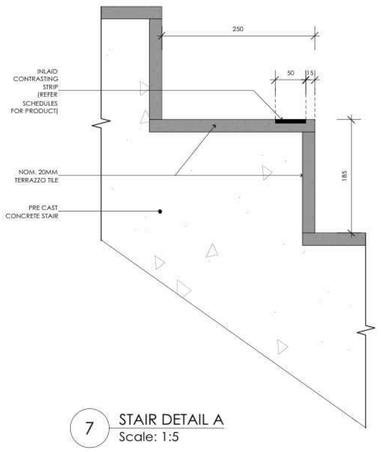

7 STAIR DETAIL A
Scale: 1:5

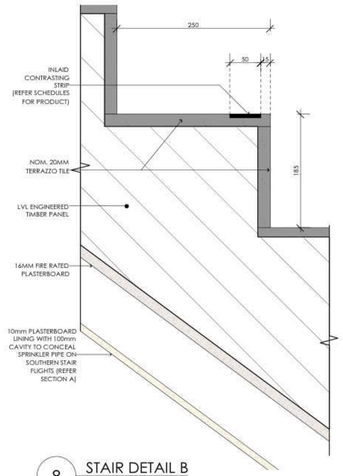

8 STAIR DETAIL B
Scale: 1:5

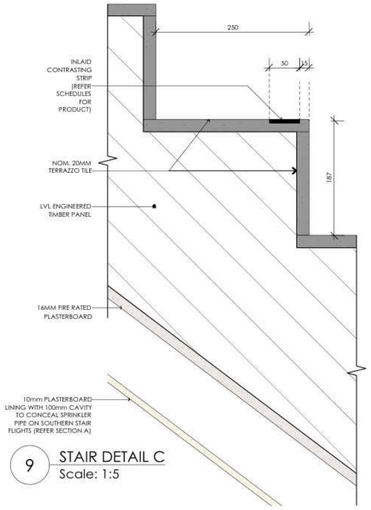

9 STAIR DETAIL C
Scale: 1:5

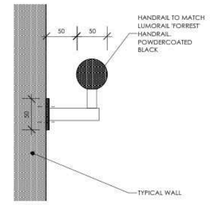

10 TYPICAL HANDRAIL
Scale: 1:5

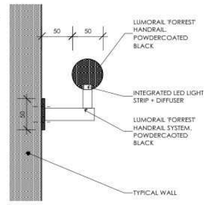

11 TYPICAL HANDRAIL (WITH LIGHT)
Scale: 1:5

FINISHES LEGEND

TERR 1	SELECTED TERRAZZO STONE TILE	(REFER SCHEDULE OF FLOOR FINISHES FOR PRODUCT)
TLB 2	INTERNAL TIMBER LINING	(REFER SCHEDULES FOR PRODUCT)

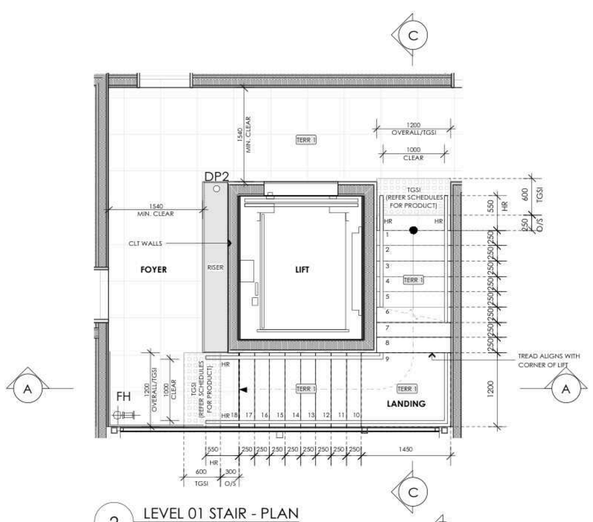

2 LEVEL 01 STAIR - PLAN
Scale: 1:50

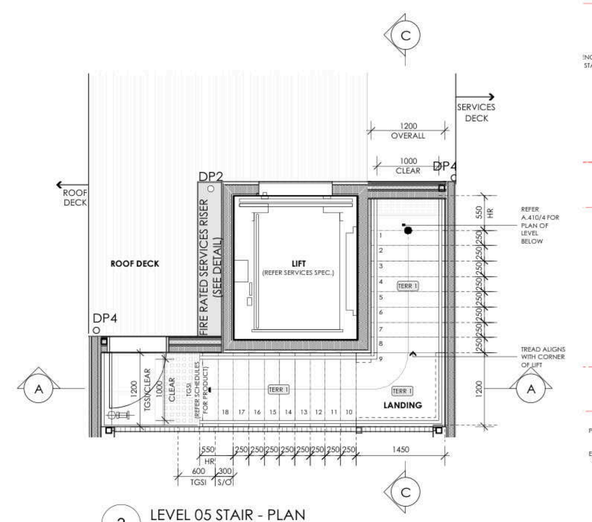

3 LEVEL 05 STAIR - PLAN
Scale: 1:50

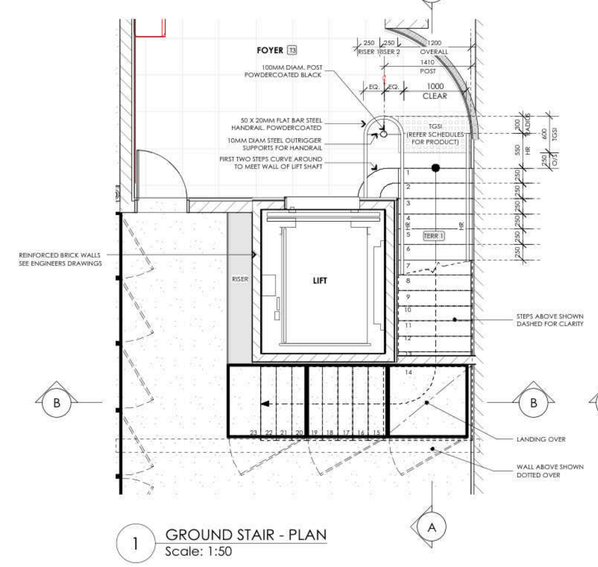

1 GROUND STAIR - PLAN
Scale: 1:50

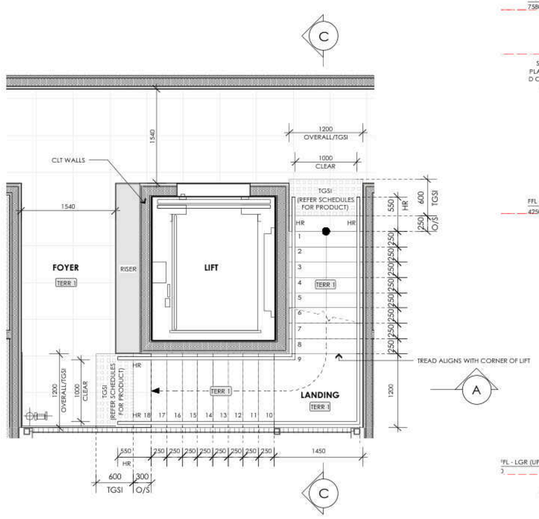

4 LEVEL 02/03/04 STAIR - TYPICAL PLAN
Scale: 1:50

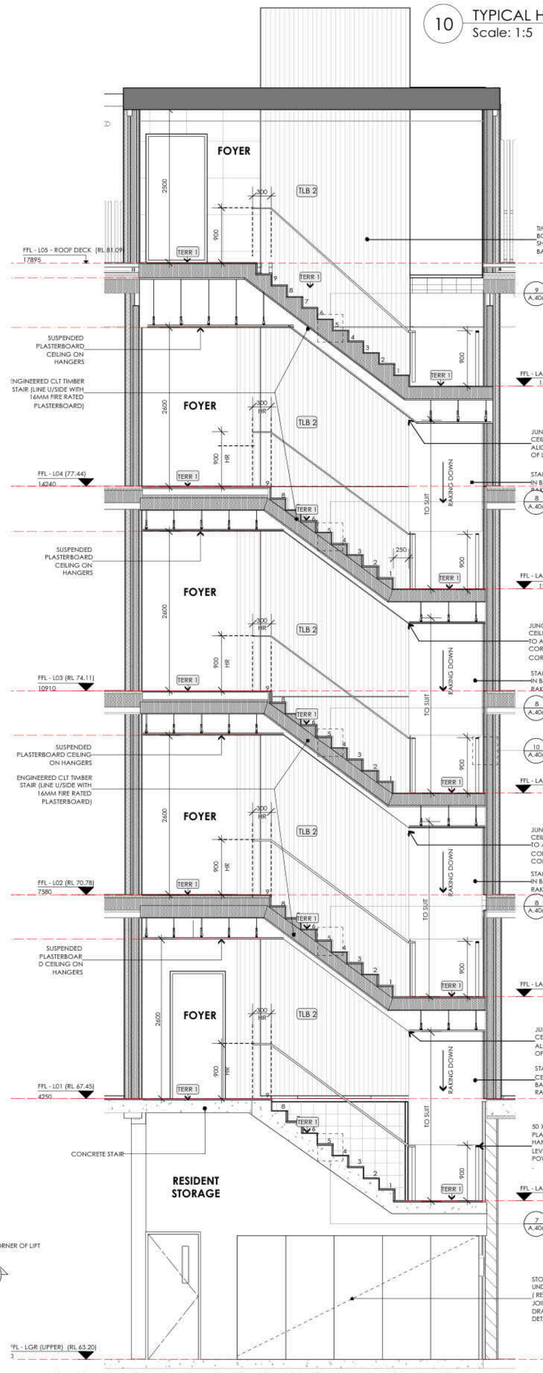

5 SECTION B:B
Scale: 1:50

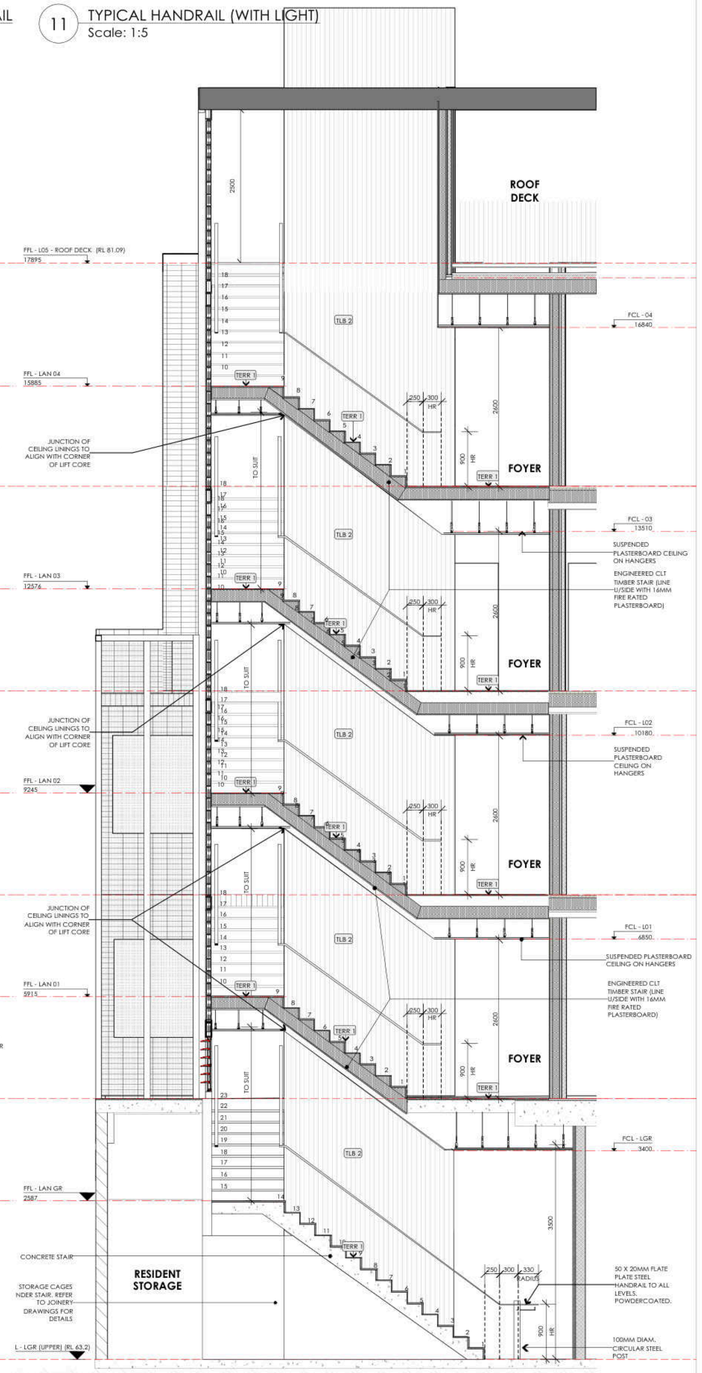

6 SECTION B:B
Scale: 1:50

FOR CONSTRUCTION - 17/12/19

ISSUE	DATE	REVISION
D	17/12/19	FOR CONSTRUCTION
C	31/5/19	CONTRACT SET

This drawing is to be in conjunction with the relevant consultants drawings and the project specification and any instruction issued during the course of the contract. Contractor to check all dimensions on site before commencing any work. Do not scale any dimensions from drawings. All setout to be confirmed by contractor on site prior to fabrication.

CLIENT CHALLEN

Gardiner Architects
77/252 St Georges Rd, Fitzroy North, VIC, 3068
Ph: (03) 9486 4092 E: info@paulgardiner.com.au

DWG DETAILS - STAIRWELL
PROJECT RETAIL/RESIDENTIAL DEVELOPMENT 752 HIGH STREET, THORNBURY
DRAWN BY AM
SCALE AS SHOWN
JOB NO 141211
A.410
DWG # REV# D

WINDOWS — GROUND FLOOR

Image	ID	Apartment #	Frame Height (MM)	Frame Width (MM)	Glazed Area	Sill Height (MM)	Frame Type	Finish	Glazing	Flyscreen	Window Furnishing	Trickle Vent
	G.01	GROUND RETAIL	2530	2355	5.21	1000	STEEL	3	DG, C	NA	NA	NA
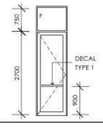	G.02	GROUND RETAIL	3530	1000	2.55	-130	STEEL	1	DG, C	NA	REFER DOOR HARDWARE SCHEDULE	NA
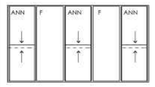	G.03	GROUND RETAIL	2530	4580	10.38	1000	STEEL	3	DG, C	NA	NA	NA
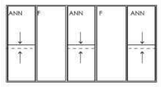	G.04	GROUND RETAIL	2530	4900	11.17	1000	STEEL	3	DG, C	NA	NA	NA
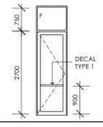	G.05	GROUND RETAIL	3530	1000	2.55	-130	STEEL	1	DG, C	NA	NA	NA
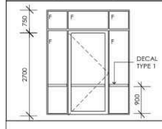	G.06	GROUND RETAIL	3400	2700	7.62	0	TIMB	1	DG, C	NA	NA	NA
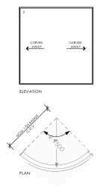	G.07	GROUND RETAIL	2450	1725 RADIUS C.O.S	NA	1000	STEEL	3	DG, C	NA	NA	NA

WINDOWS — FIRST FLOOR

Image	ID	Apartment #	Frame Height (MM)	Frame Width (MM)	Glazed Area	Sill Height (MM)	Frame Type	Finish	Glazing	Flyscreen	Window Furnishing	Trickle Vent
	1.01	2	1600	1378	1.59	1000	ALU	3	DG, C, SAF	1	ERB	YES
	1.02	2	1600	1500	1.77	1000	ALU	3	DG, C, AG, SAF	1	ERB	YES
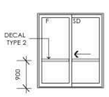	1.03	2	2413	2145	3.73	187	ALU	3	DG, C, AG	2	NA	YES

WINDOWS — FIRST FLOOR CONT.

Image	ID	Apartment #	Frame Height (MM)	Frame Width (MM)	Glazed Area	Sill Height (MM)	Frame Type	Finish	Glazing	Flyscreen	Window Furnishing	Trickle Vent
	1.04	2	1600	2700	3.23	1000	ALU	3	DG, C, AG	1	EB	YES
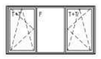	1.05	1	1600	2880	3.48	1000	ALU	3	DG, C, AG	1	EB	YES
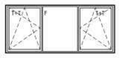	1.06	1	1600	3570	4.45	1000	ALU	3	DG, C, AG	1	NA	YES
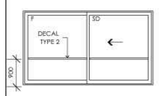	1.07	1	2413	4200	8.07	187	ALU	3	DG, C, AG	2	NA	YES
	1.08	1	1600	1500	1.77	1000	ALU	3	DG, C, AG	1	ERB	YES
	1.09	1	1600	1500	1.77	1000	ALU	3	DG, C, AG	1	ERB	YES
	1.10	4	1600	1500	1.77	1000	ALU	3	DG, C	1	ERB	YES
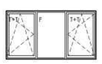	1.11	4	1600	2937	3.56	1000	ALU	3	DG, C	1	NA	YES
	1.12	4	1600	2500	3.52	1000	ALU	3	DG, C	1	NA	YES
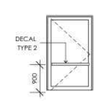	1.13	4	2413	1500	2.63	187	ALU	3	DG, C	2	NA	YES
	1.14	4	1600	900	0.92	1000	ALU	3	DG, C	1	ERB	YES
	1.15	4	1600	1500	1.77	1000	ALU	3	DG, C, SAF	1	ERB	YES

WINDOWS — FIRST FLOOR CONT.

Image	ID	Apartment #	Frame Height (MM)	Frame Width (MM)	Glazed Area	Sill Height (MM)	Frame Type	Finish	Glazing	Flyscreen	Window Furnishing	Trickle Vent
	1.16	3	1600	2700	3.23	1000	ALU	3	DG, C, SAF	1	NA	YES
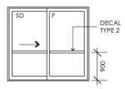	1.17	3	2413	2645	4.79	187	ALU	3	DG, C	2	NA	YES
	1.18	3	1600	1500	1.77	1000	ALU	3	DG, C, SAF	1	ERB	YES
	1.19	3	1600	1378	1.59	1000	ALU	3	DG, C, SAF	1	ERB	YES

WINDOWS — SECOND FLOOR

Image	ID	Apartment #	Frame Height (MM)	Frame Width (MM)	Glazed Area	Sill Height (MM)	Frame Type	Finish	Glazing	Flyscreen	Window Furnishing	Trickle Vent
	2.01	6	1600	1400	1.62	1000	ALU	3	DG, C, SAF	1	ERB	YES
	2.02	6	1600	1500	1.77	1000	ALU	3	DG, C, AG, SAF	1	ERB	YES
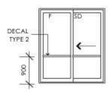	2.03	6	2430	2145	3.76	170	ALU	3	DG, C, AG	2	NA	YES
	2.04	6	1600	2700	3.23	1000	ALU	3	DG, C, AG	1	EB	YES
	2.05	5	1600	900	1.11	1000	ALU	3	SG, OG	1	EB	YES
	2.06		1600	1500	1.77	1000	ALU	3	DG, C, AG	1	ERB	YES

WINDOW LEGEND

F	FIXED GLASS	S	SASH
SD	SLIDING	CSD	CAVITY SLIDING DOOR
LAM	LAMINATE GLASS	EG	EXISTING GLASS
C	CLEAR GLASS	SG	SINGLE GLAZED
TH	TOP HUNG	DG	DOUBLE GLAZED
DH	DOUBLE HUNG	OG	OBSCURE GLASS
SH	SIDE HUNG	WG	WHITE GLASS
FS	FLYWIRE SCREEN	FS(R)	RETRACTABLE FLYWIRE SCREEN
SAF	SAFETY GLASS (TOUGHENED)	CGL	COLOUR GLASS PANEL
		LHH	LOCK + HANDLE SET
PH	PULL HANDLE	T+T	TILT + TURN WINDOW
SP	SOLID STEEL PLATE/PANEL	BF	BI-FOLDING WINDOW/DOOR
ANS	ANEETA SASHLESS SLIDER	AG	ACOUSTIC GLAZING

WINDOW NOTES

GENERAL

1. READ IN CONJUNCTION WITH SPECIFICATION
2. CONFIRM ALL DIMENSIONS ON SITE PRIOR TO FABRICATION
3. ALL WINDOWS VIEWED FROM THE OUTSIDE
4. PREFERRED SUBCONTRACTORS
   REFER SCHEDULE OF PREFERRED SUBCONTRACTORS FOR WINDOW SUPPLIERS
5. ASSUME EQUAL WIDTH DIMENSIONS U.O.N
6. * REFERS TO THE TOTAL VENTILATION/GLAZING PERCENTAGE VALUE OF ALL OPERABLE OPENINGS WITHIN THAT ROOM
7. **GLAZED AREA RATIO** REFERS TO PROVISION OF NATURAL LIGHT AS SPECIFIED IN NCC VOL. SECTION F4.1-4.2
8. **VENT AREA RATIO** REFERS TO TO PROVISION OF NATURAL VENTILATION AS SPECIFIED IN NCC VOL SECTION F4.5-4.6
9. OPENABLE PARTS TO ALL WINDOWS GREATER THAN 2.0M ABOVE SURFACE LEVEL TO HAVE A MAXIMUM OPENING SIZE OF 125MM.

HARDWARE

REFER SCHEDULE OF DOOR HARDWARE

WINDOW TYPES

ALUMINIUM FRAME:
- FRAME - THERMALLY BROKEN ALUMINIUM
- FINISH - POWDERCOATES (SEE NOTES)
- COLOUR - TBC
- GLAZING - DOUBLE GLAZED (SEE NOTES)
- ENERGY RATING REQUIRMENT - REFER ENERGY REPORT
- SEALED FOR RAIN AND WIND
- FLYWIRE TYPE - TYPE 1
- HARDWARE PRODUCT - INCLUDE PROPRIETARY HANDLES AND LOCKS
- BUILDER NOMINATED SYSTEM

TIMBER FRAME:
- FRAME - KILN DRIED HARDWOOD
- SUSTAINABLY FORESTED AND CERTIFIED
- ENGINEERED PROFILE FOR WIND AND RAIN
- FINISH - RAW FOR STAINING AND FINISHING
- COLOUR - NATURAL
- GLAZING - DOUBLE GLAZED (SEE NOTES)
- ENERGY RATING REQUIRMENT - REFER ENERGY REPORT
- COMPLY WITH 6 STAR RATING
- HARDWARE PRODUCT - INCLUDE PROPRIETARY HANDLES AND LOCKS
- BUILDER NOMINATED SYSTEM

STEEL FRAME:
- FRAME - ROLLED STEEL, PROPRIETARY SYSTEM
- PROVISION IN FRAME TO ALLOW FOR FUTURE INSTALLATION OF FLYWIRE
- FINISH - POWDERCOAT ON GALVINISED FINISH
- COLOUR - TBC
- GLAZING - DOUBLE GLAZED (SEE NOTES)
- ENERGY RATING REQUIRMENT - REFER ENERGY REPORT
- FLYWIRE TYPE - NA
- HARDWARE PRODUCT - INCLUDE PROPRIETARY HANDLES AND LOCKS
- WINDOWS ON THE WORLD OR SIMILAR APPROVED
- REFER SCHEDULE OF PREFERRED SUBCONTRACTORS

GLAZING

- SAFETY GLAZING TO BE MIN. 6MM THICKNESS + SUBJECTED TO HEAT SOAKING PROCESS TO RID NICKEL SULPHIDE IMPURITIES AS PER FIRE ENGINEER SPEC.

FLYWIRE

1. ALL OPENING SASHES TO HAVE FLYWIRE SCREENS
2. TYPES
   - TYPE 1 - FIXED STANDARD BLACK ALUMINIUM MESH
     - POWDERCOATED FRAMES
     - COLOUR: MATCH FRAME
   - TYPE 2 - HORIZONTAL ACTION RETRACTABLE SCREEN, TRACKS TOP AND BOTTOM
     - POWDERCOATED FRAMES
     - COLOUR: MATCH FRAMES
     - PRODUCT: BRIO OR SIMILAR APPROVED

FINISHES

1. STAINED - FINE SANDED & STAINED
   - DANISH OIL OR SIMILAR
2. PAINTED - FINE SANDED & PRIMED
   - 2 TOP COATS
3. POWERCOAT - SELECTED FROM DULUX OR SIMILAR
   - COLOUR: MATCH FRAME

SASHLESS GLASS UNITS

- FUNCTION - COUNTER BALANCED FRAMELESS GLASS UP/DOWN
- PRODUCT - ANEETA OR SIMILAR APPROVED
- GLAZING - DOUBLE GLAZED U.O.N. (SEE 'GLAZING')
- FRAME + BEAD TYPE - POWDERKOTED ALUMINIUM, SELECTED COLOUR
- LOCKING - STANDARD KEY LOCK
  - SECOND POSITION 100mm HIGHER
- FLYSCREENS - INCLUDE INTEGRATED FLYSCREEN TYPE 1

GLAZING DECALS

- TYPE 1 - PUBLIC AREAS AS SHOWN IN SCHEDULE
  - ACHIEVING 75MM THICK, SOLID, NON TRANSPARENT CONTRASTING STRIP (MIN. 30% LUMINANCE CONTRAST WHEN VIEWED AGAINST FLOOR OR WALL
  - APPEARANCE: TBC
- TYPE 2 - APARTMENTS IN GLAZED DOORS
  - AS ABOVE TO ABOVE
  - APPEARANCE: TBC

WINDOW FURNISHING

(REFER A.405 FOR TYPICAL WINDOW DETAILS)

- ERB - **EXPOSED** INTERNAL PELMET ROLLER BLIND
  REFER SCHEDULES FOR PRODUCT + A.405 FOR DETAIL)
- CRB - **CONCEALED** INTERNAL PELMET ROLLER BLIND
  (REFER SCHEDULES FOR PRODUCT + A.405 FOR DETAIL)
- EB - EXTERNAL BLIND
  (REFER SCHEDULES FOR PRODUCT + A.405 FOR DETAIL)

TRICKLE VENTILATION

AS NOTED ON SCHEDULE

PRODUCT: PROCTOR VENTENT
ARRANGEMENT: HORIZONTAL WITHIN WINDOW FRAMING SUITE

FOR CONSTRUCTION - 17/12/19

ISSUE	DATE	REVISION
D	17/12/19	FOR CONSTRUCTION
C	31/5/19	CONTRACT SET

CLIENT: H.CHARALAMBOUS

Gardiner Architects
77/252 St Georges Rd, Fitzroy North, VIC, 3068
Ph: (03) 9486 4092, E: info@paulgardiner.com.au

DWG: **WINDOWS, DOORS & PARTITIONS SCHEDULE**
PROJECT: RETAIL/RESIDENTIAL DEVELOPMENT
752 HIGH STREET, THORNBURY
DRAWN BY: AM
SCALE: 1:100 @A1
JOB NO: 141211
A.501
DWG #
REV# D

WINDOWS SECOND FLOOR

Image	ID	Apartment #	Frame Height (MM)	Frame Width (MM)	Glazed Area	Sill Height (MM)	Frame Type	Finish	Glazing	Flyscreen	Window Furnishing	Trickle Vent
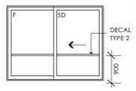	2.07	5	2430	3150	5.9	170	ALU	3	DG, C, AG	2	NA	YES
	2.08	5	1600	3600	4.49	1000	ALU	3	DG, C, AG	1	NA	YES
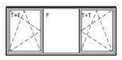	2.09	9	1600	3600	4.49	1000	ALU	3	DG, C, AG	1	NA	YES
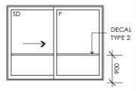	2.10	9	2430	3150	5.9	170	ALU	3	DG, C	2	NA	YES
	2.11	9	1600	1500	1.77	1000	ALU	3	DG, C	1	CRB	YES
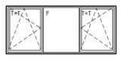	2.12	8	1600	3600	4.49	1000	ALU	3	DG, C	1	NA	YES
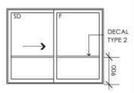	2.13	8	2430	3150	5.9	170	ALU	3	DG, C	2	NA	YES
	2.14	8	1600	1500	1.77	1000	ALU	3	DG, C	1	ERB	YES
	2.15	8	1600	900	1.11	1000	ALU	3	SG, OG, SAF	1	NA	YES
	2.16	7	1600	2700	3.23	1000	ALU	3	DG, C, SAF	1	NA	YES
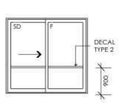	2.17	7	2430	2645	4.82	170	ALU	3	DG, C	2	NA	YES
	2.18	7	1600	1500	1.77	1000	ALU	3	DG, C, SAF	1	ERB	YES

WINDOWS SECOND FLOOR CONT.

Image	ID	Apartment #	Frame Height (MM)	Frame Width (MM)	Glazed Area	Sill Height (MM)	Frame Type	Finish	Glazing	Flyscreen	Window Furnishing	Trickle Vent
	2.19	7	1600	1400	1.62	1000	ALU	3	DG, C, SAF	1	ERB	YES

WINDOWS THIRD FLOOR

Image	ID	Apartment #	Frame Height (MM)	Frame Width (MM)	Glazed Area	Sill Height (MM)	Frame Type	Finish	Glazing	Flyscreen	Window Furnishing	Trickle Vent
	3.01	10	1600	1500	1.77	1000	ALU	3	DG, C, AG, SAF	1	CRB	YES
	3.02	10	1600	1500	1.77	1000	ALU	3	DG, C, AG, SAF	1	CRB	YES
	3.03	10	1600	1500	1.77	1000	ALU	3	DG, C, AG, SAF	1	CRB	YES
	3.04	10	1600	1500	1.77	1000	ALU	3	DG, C, AG	1	EB + CRB	YES
	3.05	10	1600	1525	1.8	1000	ALU	3	DG, C, AG	1	EB	YES
	3.06	10	2460	900	1.36	140	ALU	3	DG, C, AG	2	CRB	YES
	3.07	10	1600	2750	3.3	1000	ALU	3	DG, C, AG	1	EB	YES
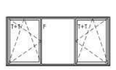	3.08	10	1600	3358	4.15	1000	ALU	3	DG, C, AG	1	RP	YES
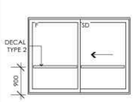	3.09	10	2460	3300	6.31	140	ALU	3	DG, C, AG	1	CRB	YES
	3.10	10	1600	1200	1.33	1000	ALU	3	DG, C, AG	1	CRB	YES

WINDOWS THIRD FLOOR CONT.

Image	ID	Apartment #	Frame Height (MM)	Frame Width (MM)	Glazed Area	Sill Height (MM)	Frame Type	Finish	Glazing	Flyscreen	Window Furnishing	Trickle Vent
	3.11	11	1600	1500	1.77	1000	ALU	3	DG, C	1	CRB	YES
	3.12	11	1600	755	0.9	1000	ALU	3	SG, OG	1	NA	YES
	3.13	11	1600	1225	1.37	1000	ALU	3	DG, C	1	CRB	YES
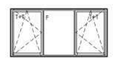	3.14	11	1600	3150	3.86	1000	ALU	3	DG, C	1	CRB	YES
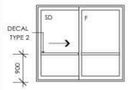	3.15	11	2460	2850	5.34	140	ALU	3	DG, C	2	CRB	YES
	3.16		1600	2100	2.75	1000	ALU	3	DG,C	1	CRB	YES
	3.17	11	1600	1500	1.77	1000	ALU	3	DG, C, SAF	1	CRB	YES
	3.18	11	1600	1500	1.77	1000	ALU	3	DG, C, SAF	1	CRB	YES

WINDOWS FOURTH FLOOR

Image	ID	Apartment #	Frame Height (MM)	Frame Width (MM)	Glazed Area	Sill Height (MM)	Frame Type	Finish	Glazing	Flyscreen	Window Furnishing	Trickle Vent
	4.01	12	1600	1500	1.77	1000	ALU	3	DG, C, AG, SAF	1	CRB	YES
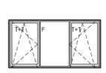	4.02	12	1600	3000	3.65	1000	ALU	3	DG, C, AG, SAF	1	CRB	YES
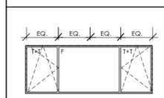	4.03	12	1600	4140	5.83	1000	ALU	3	DG, C, AG	1	EB	YES

WINDOW LEGEND

F	FIXED GLASS	S	SASH
SD	SLIDING	CSD	CAVITY SLIDING DOOR
LAM	LAMINATE GLASS	EG	EXISTING GLASS
C	CLEAR GLASS	SG	SINGLE GLAZED
TH	TOP HUNG	DG	DOUBLE GLAZED
DH	DOUBLE HUNG	OG	OBSCURE GLASS
SH	SIDE HUNG	WG	WHITE GLASS
FS	FLYWIRE SCREEN	FS(R)	RETRACTABLE FLYWIRE SCREEN
SAF	SAFETY GLASS (TOUGHENED)	CGL	COLOUR GLASS PANEL
		LHH	LOCK + HANDLE SET
PH	PULL HANDLE	T+T	TILT + TURN WINDOW
SP	SOLID STEEL PLATE/PANEL	BF	BI-FOLDING WINDOW/DOOR
ANS	ANEETA SASHLESS SLIDER	AG	ACOUSTIC GLAZING

WINDOW NOTES

GENERAL

1. READ IN CONJUNCTION WITH SPECIFICATION
2. CONFIRM ALL DIMENSIONS ON SITE PRIOR TO FABRICATION
3. ALL WINDOWS VIEWED FROM THE OUTSIDE
4. PREFERRED SUBCONTRACTORS
   REFER SCHEDULE OF PREFERRED SUBCONTRACTORS FOR WINDOW SUPPLIERS
5. ASSUME EQUAL WIDTH DIMENSIONS U.O.N
6. * REFERS TO THE TOTAL VENTILATION/GLAZING PERCENTAGE VALUE OF ALL OPERABLE OPENINGS WITHIN THAT ROOM
7. **GLAZED AREA RATIO** REFERS TO PROVISION OF NATURAL LIGHT AS SPECIFIED IN NCC VOL SECTION F4.1-4.2
8. **VENT AREA RATIO** REFERS TO TO PROVISION OF NATURAL VENTILATION AS SPECIFIED IN NCC VOL SECTION F4.5-4.6
9. OPENABLE PARTS TO ALL WINDOWS GREATER THAN 2.0M ABOVE SURFACE LEVEL TO HAVE A MAXIMUM OPENING SIZE OF 125MM.

HARDWARE

REFER SCHEDULE OF DOOR HARDWARE

WINDOW TYPES

ALUMINIUM FRAME:
- FRAME - THERMALLY BROKEN ALUMINIUM
- FINISH - POWDERCOATES (SEE NOTES)
- COLOUR - TBC
- GLAZING - DOUBLE GLAZED (SEE NOTES)
- ENERGY RATING REQUIRMENT - REFER ENERGY REPORT - SEALED FOR RAIN AND WIND
- FLYWIRE TYPE - TYPE 1
- HARDWARE PRODUCT - INCLUDE PROPRIETARY HANDLES AND LOCKS - BUILDER NOMINATED SYSTEM

TIMBER FRAME:
- FRAME - KILN DRIED HARDWOOD - SUSTAINABLY FORESTED AND CERTIFIED - ENGINEERED PROFILE FOR WIND AND RAIN
- FINISH - RAW FOR STAINING AND FINISHING
- COLOUR - NATURAL
- GLAZING - DOUBLE GLAZED (SEE NOTES)
- ENERGY RATING REQUIRMENT - REFER ENERGY REPORT - COMPLY WITH 6 STAR RATING
- HARDWARE PRODUCT - INCLUDE PROPRIETARY HANDLES AND LOCKS - BUILDER NOMINATED SYSTEM

STEEL FRAME:
- FRAME - ROLLED STEEL, PROPRIETARY SYSTEM - PROVISION IN FRAME TO ALLOW FOR FUTURE INSTALLATION OF FLYWIRE
- FINISH - POWDERCOAT ON GALVINISED FINISH
- COLOUR - TBC
- GLAZING - DOUBLE GLAZED (SEE NOTES)
- ENERGY RATING REQUIRMENT - REFER ENERGY REPORT
- FLYWIRE TYPE - NA
- HARDWARE PRODUCT - INCLUDE PROPRIETARY HANDLES AND LOCKS - WINDOWS ON THE WORLD OR SIMILAR APPROVED - REFER SCHEDULE OF PREFERRED SUBCONTRACTORS

GLAZING

- SAFETY GLAZING TO BE MIN. 6MM THICKNESS + SUBJECTED TO HEAT SOAKING PROCESS TO RID NICKEL SULPHIDE IMPURITIES AS PER FIRE ENGINEER SPEC.

FLYWIRE

1. ALL OPENING SASHES TO HAVE FLYWIRE SCREENS
2. TYPES
   - TYPE 1 - FIXED STANDARD BLACK ALUMINIUM MESH - POWDERCOATED FRAMES - COLOUR: MATCH FRAME
   - TYPE 2 - HORIZONTAL ACTION RETRACTABLE SCREEN, TRACKS TOP AND BOTTOM - POWDERCOATED FRAMES - COLOUR: MATCH FRAMES - PRODUCT: BRIO OR SIMILAR APPROVED

FINISHES

1. STAINED - FINE SANDED & STAINED - DANISH OIL OR SIMILAR
2. PAINTED - FINE SANDED & PRIMED - 2 TOP COATS
3. POWERCOAT - SELECTED FROM DULUX OR SIMILAR - COLOUR: MATCH FRAME

SASHLESS GLASS UNITS

- FUNCTION - COUNTER BALANCED FRAMELESS GLASS UP/DOWN
- PRODUCT - ANEETA OR SIMILAR APPROVED
- GLAZING - DOUBLE GLAZED U.O.N. (SEE 'GLAZING')
- FRAME + BEAD TYPE - POWDERKOTED ALUMINIUM, SELECTED COLOUR
- LOCKING - STANDARD KEY LOCK - SECOND POSITION 100mm HIGHER
- FLYSCREENS - INCLUDE INTEGRATED FLYSCREEN TYPE 1

GLAZING DECALS

- TYPE 1 - PUBLIC AREAS AS SHOWN IN SCHEDULE - ACHIEVING 75MM THICK, SOLID, NON TRANSPARENT CONTRASTING STRIP (MIN. 30% LUMINANCE CONTRAST WHEN VIEWED AGAINST FLOOR OR WALL - APPEARANCE: TBC
- TYPE 2 - APARTMENTS IN GLAZED DOORS - AS ABOVE TO ABOVE - APPEARANCE: TBC

WINDOW FURNISHING

(REFER A.405 FOR TYPICAL WINDOW DETAILS)

- ERB - **EXPOSED** INTERNAL PELMET ROLLER BLIND REFER SCHEDULES FOR PRODUCT + A.405 FOR DETAIL)
- CRB - **CONCEALED** INTERNAL PELMET ROLLER BLIND (REFER SCHEDULES FOR PRODUCT + A.405 FOR DETAIL)
- EB - EXTERNAL BLIND (REFER SCHEDULES FOR PRODUCT + A.405 FOR DETAIL)

TRICKLE VENTILATION

AS NOTED ON SCHEDULE

PRODUCT: PROCTOR VENTIENT
ARRANGEMENT: HORIZONTAL WITHIN WINDOW FRAMING SUITE

FOR CONSTRUCTION - 17/12/19

ISSUE	DATE	REVISION
D	17/12/19	FOR CONSTRUCTION
C	31/5/19	CONTRACT SET

This drawing to read in conjunction with the other contract documents forming the project specification and any instructions issued during the course of the contract. Contractor must verify all dimensions on site before commencing any work. Discrepancies must be reported to the superintendent/architect of all discrepancies in documents.

CLIENT H.CHARALAMBOUS

Gardiner Architects
7/252 S Georges Rd, Fitzroy North, VIC, 3068
Ph: (03) 9486 4092 E: info@paulgardiner.com.au

DWG WINDOWS, DOORS & PARTITIONS SCHEDULE
PROJECT RETAIL/RESIDENTIAL DEVELOPMENT, 752 HIGH STREET, THORNBURY
DRAWN BY AM
SCALE 1:100 @ A1
JOB NO 141211
A.502
DWG #
REV# D

WINDOWS — FOURTH FLOOR CONT.

Image	ID	Apartment #	Frame Height (MM)	Frame Width (MM)	Glazed Area	Sill Height (MM)	Frame Type	Finish	Glazing	Flyscreen	Window Furnishing	Trickle Vent
	4.04	12	1600	900	0.92	1000	ALU	3	DG, C, AG	1	EB	YES
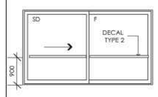	4.05	12	2430	4200	8.14	170	ALU	1	DG, C, AG	2	CRB	YES
	4.06	12	1600	1500	1.77	1000	ALU	3	DG, C, AG	1	CRB	YES
	4.07	12	1600	1500	1.77	1000	ALU	3	DG, C	1	CRB	YES
	4.08	12	1600	877	1.08	1000	ALU	3	SG, OG	1	NA	YES
	4.09	13	1600	1200	1.33	1000	ALU	3	DG, C	1	CRB	YES
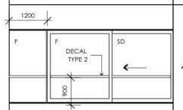	4.10	13	2430	5420	10.91	170	ALU	1	DG, C	2	RP	YES
	4.11	13	1600	1000	1.06	1000	ALU	3	DG, C	1	CRB	YES
	4.12	13	1600	1500	1.77	1000	ALU	3	DG, C, SAF	1	CRB	YES
	4.13	13	1600	900	1.11	1000	ALU	3	SG, OG, SAF	1	NA	YES
	4.14	13	1600	1500	1.77	1000	ALU	3	DG, C, SAF	1	CRB	YES

DOORS — GROUND FLOOR

Image	ID	Location	Opening Height (MM)	Opening Width (MM)	Construction	Frame	FRL REQ.	Function	Finish	Viewing Panel
	G.01	GROUND FLOOR SERVICE AREA (INTERNAL)	2100	1000	SOLID CORE	STEEL	-/90/30	SWING DOOR	3	YES
	G.02	GROUND FLOOR SERVICE AREA (EXTERNAL)	2100	1540	SOLID CORE	TIM	-/60/30	SWING DOOR	2	N/A
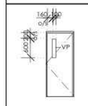	G.03	GROUND FLOOR CLEANER C'PUD (INTERNAL)	2100	900	SOLID CORE	STEEL	-/60/30	SWING DOOR	3	YES
	G.04	GROUND FLOOR DDA WC (INTERNAL)	2100	900	SOLID CORE	TIM	N/A	SWING DOOR	2	N/A
	G.05 G.06	GROUND FLOOR AMBULANTWC (INTERNAL)	2100	900	SOLID CORE	TIM	N/A	SWING DOOR	2	N/A
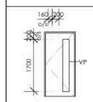	G.07	GROUND FLOOR WET AREAS(INTERNAL)	2100	1000 MIN. 920 DOOR LEAF	SOLID CORE	TIM	N/A	SWING DOOR	2	YES
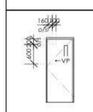	G.08	GROUND FLOOR FOYER/RESIDENT STORAGE(INTERNAL)	2100	900	SOLID CORE	STEEL	-/90/30	SWING DOOR	3	YES

DOORS — FLOORS 01 -05

Image	ID	Location	Opening Height (MM)	Opening Width (MM)	Construction	Frame	FRL REQ.	Function	Finish	Viewing Panel
	1.01 2.14 1.06 2.18 1.11 3.01 1.16 3.07 2.01 4.01 2.06 4.07 2.10	APARTMENTS 1-13 FRONT ENTRY DOORS (INTERNAL)	2400	900	TIMBER SOLID CORE (PYROPANEL PFD 060-38 COMPLIANT WITH FRAME)	TIMBER (PYROPANEL 1 HR FIRE RATED COMPLIANT WITH LEAF)	-/60/30	SWING DOOR	1	N/A
	1.03 2.04 1.05 2.20 1.08 3.04 1.10 3.05 1.12 3.10 1.14 4.06 1.17 4.10 1.19	APARTMENTS 1-13 WET AREA SWING DOORS (INTERNAL)	2100 (NOM. 20MM UNDERCUT)	900	TIMBER SEIM-SOLID CORE	TIMBER	N/A	SWING DOOR	1	N/A
	2.02 2.08 2.12 2.16 2.22 3.09 4.03 4.09	APARTMENTS 1-13 WET AREA CSD (INTERNAL)	2100 (NOM. 20MM UNDERCUT)	900	TIMBER SEMI SOLID CORE	TIMBER	N/A	CSD	1	N/A
	2.07 2.11 2.15	APARTMENTS 1-13 CSD (INTERNAL)	2100 (NOM. 20MM UNDERCUT)	900	TIMBER SEMI SOLID CORE	TIMBER	N/A	CSD	1	N/A
	1.02 2.03 3.03 1.04 2.05 3.06 1.07 2.09 3.08 1.09 2.13 3.11 1.13 2.17 3.12 1.15 2.19 4.02 1.18 2.21 4.04 1.20 3.02 4.05 4.11	APARTMENTS 1-13 BEDROOMS	2100	900	TIMBER SEMI SOLID CORE	TIMBER	N/A	SWING DOOR	1	N/A
	5.01	ROOF DECK (EXTERNAL)	2100	1000	TIMBER SEIM-SOLID CORE	STEEL	-/60/30	SWING DOOR	1	YES

NOTE: SOU FRONT ENTRY DOORS TO ACHIEVE MIN. ACOUSTIC RATING OF Rw >30

WINDOW LEGEND

F	FIXED GLASS	S	SASH
SD	SLIDING	CSD	CAVITY SLIDING DOOR
LAM	LAMINATE GLASS	EG	EXISTING GLASS
C	CLEAR GLASS	SG	SINGLE GLAZED
TH	TOP HUNG	DG	DOUBLE GLAZED
DH	DOUBLE HUNG	OG	OBSCURE GLASS
SH	SIDE HUNG	WG	WHITE GLASS
FS	FLYWIRE SCREEN	RSB	RETRACTABLE FLYWIRE SCREEN
SAF	SAFETY GLASS (TOUGHENED)	CGL	COLOUR GLASS PANEL
		LHH	LOCK + HANDLE SET
PH	PULL HANDLE	T+T	TILT + TURN WINDOW
SP	SOLID STEEL PLATE/PANEL	BF	BI-FOLDING WINDOW/DOOR
ANS	ANEETA SASHLESS SLIDER	AG	ACOUSTIC GLAZING

WINDOW NOTES

GENERAL
1. READ IN CONJUNCTION WITH SPECIFICATION
2. CONFIRM ALL DIMENSIONS ON SITE PRIOR TO FABRICATION
3. ALL WINDOWS VIEWED FROM THE OUTSIDE
4. PREFERRED SUBCONTRACTORS
   REFER SCHEDULE OF PREFERRED SUBCONTRACTORS FOR WINDOW SUPPLIERS
5. ASSUME EQUAL WIDTH DIMENSIONS U.O.N
6. * REFERS TO THE TOTAL VENTILATION/GLAZING PERCENTAGE VALUE OF ALL OPERABLE OPENINGS WITHIN THAT ROOM
7. **GLAZED AREA RATIO** REFERS TO PROVISION OF NATURAL LIGHT AS SPECIFIED IN NCC VOL SECTION F4.1-4.2
8. **VENT AREA RATIO** REFERS TO TO PROVISION OF NATURAL VENTILATION AS SPECIFIED IN NCC VOL SECTION F4.5-4.6
9. OPENABLE PARTS TO ALL WINDOWS GREATER THAN 2.0M ABOVE SURFACE LEVEL TO HAVE A MAXIMUM OPENING SIZE OF 125MM.

HARDWARE
REFER SCHEDULE OF DOOR HARDWARE

WINDOW TYPES
ALUMINIUM FRAME:
- FRAME - THERMALLY BROKEN ALUMINIUM
- FINISH - POWDERCOATES (SEE NOTES)
- COLOUR - TBC
- GLAZING - DOUBLE GLAZED (SEE NOTES)
- ENERGY RATING REQUIRMENT - REFER ENERGY REPORT - SEALED FOR RAIN AND WIND
- FLYWIRE TYPE - TYPE 1
- HARDWARE - INCLUDE PROPRIETARY HANDLES AND LOCKS
- PRODUCT - BUILDER NOMINATED SYSTEM

TIMBER FRAME:
- FRAME - KILN DRIED HARDWOOD - SUSTAINABLY FORESTED AND CERTIFIED - ENGINEERED PROFILE FOR WIND AND RAIN
- FINISH - RAW FOR STAINING AND FINISHING
- COLOUR - NATURAL
- GLAZING - DOUBLE GLAZED (SEE NOTES)
- ENERGY RATING REQUIRMENT - REFER ENERGY REPORT - COMPLY WITH 6 STAR RATING
- HARDWARE - INCLUDE PROPRIETARY HANDLES AND LOCKS
- PRODUCT - BUILDER NOMINATED SYSTEM

STEEL FRAME:
- FRAME - ROLLED STEEL, PROPRIETARY SYSTEM - PROVISION IN FRAME TO ALLOW FOR FUTURE INSTALLATION OF FLYWIRE
- FINISH - POWDERCOAT ON GALVINISED FINISH
- COLOUR - TBC
- GLAZING - DOUBLE GLAZED (SEE NOTES)
- ENERGY RATING REQUIRMENT - REFER ENERGY REPORT
- FLYWIRE TYPE - NA
- HARDWARE - INCLUDE PROPRIETARY HANDLES AND LOCKS
- PRODUCT - WINDOWS ON THE WORLD OR SIMILAR APPROVED - REFER SCHEDULE OF PREFERRED SUBCONTRACTORS

GLAZING
- SAFETY GLAZING TO BE MIN. 6MM THICKNESS + SUBJECTED TO HEAT SOAKING PROCESS TO RID NICKEL SULPHIDE IMPURITIES AS PER FIRE ENGINEER SPEC.

FLYWIRE
1. ALL OPENING SASHES TO HAVE FLYWIRE SCREENS
2. TYPES
   - TYPE 1 - FIXED STANDARD BLACK ALUMINIUM MESH - POWDERCOATED FRAMES - COLOUR: MATCH FRAME
   - TYPE 2 - HORIZONTAL ACTION RETRACTABLE SCREEN, TRACKS TOP AND BOTTOM. - POWDERCOATED FRAMES - COLOUR: MATCH FRAMES - PRODUCT: BRIO OR SIMILAR APPROVED

FINISHES
1. STAINED - FINE SANDED & STAINED - DANISH OIL OR SIMILAR
2. PAINTED - FINE SANDED & PRIMED - 2 TOP COATS
3. POWERCOAT - SELECTED FROM DULUX OR SIMILAR - COLOUR: MATCH FRAME

SASHLESS GLASS UNITS
- FUNCTION - COUNTER BALANCED FRAMELESS GLASS UP/DOWN
- PRODUCT - ANEETA OR SIMILAR APPROVED
- GLAZING - DOUBLE GLAZED U.O.N. (SEE 'GLAZING')
- FRAME +
- BEAD TYPE - POWDERKOTED ALUMINIUM, SELECTED COLOUR
- LOCKING - STANDARD KEY LOCK - SECOND POSITION 100mm HIGHER
- FLYSCREENS - INCLUDE INTEGRATED FLYSCREEN TYPE 1

GLAZING DECALS
- TYPE 1 - PUBLIC AREAS AS SHOWN IN SCHEDULE - ACHIEVING 75MM THICK, SOLID, NON TRANSPARENT CONTRASTING STRIP (MIN. 30% LUMINANCE CONTRAST WHEN VIEWED AGAINST FLOOR OR WALL - APPEARANCE: TBC
- TYPE 2 - APARTMENTS IN GLAZED DOORS - AS ABOVE TO ABOVE - APPEARANCE: TBC

WINDOW FURNISHING
(REFER A.405 FOR TYPICAL WINDOW DETAILS)
- ERB - **EXPOSED** INTERNAL PELMET ROLLER BLIND REFER SCHEDULES FOR PRODUCT + A.405 FOR DETAIL)
- CRB - **CONCEALED** INTERNAL PELMET ROLLER BLIND (REFER SCHEDULES FOR PRODUCT + A.405 FOR DETAIL)
- EB - EXTERNAL BLIND (REFER SCHEDULES FOR PRODUCT + A.405 FOR DETAIL)

TRICKLE VENTILATION
AS NOTED ON SCHEDULE

PRODUCT: PROCTOR VENTENT
ARRANGEMENT: HORIZONTAL WITHIN WINDOW FRAMING SUITE

FOR CONSTRUCTION - 17/12/19

This drawing is copyright and may not be reproduced without written permission. Do not scale this drawing. Figured dimensions only to be taken. Contractor is to verify all dimensions on site before commencing any work. Any discrepancies to be reported to the Architect before proceeding with the work.

ISSUE	DATE	REVISION
D	17/12/19	FOR CONSTRUCTION
C	31/5/19	CONTRACT SET

CLIENT: H.CHARALAMBOUS

Gardiner Architects
7/252 St Georges Rd, Fitzroy North, VIC, 3068
Ph: (03) 9486 4092 E: info@paulgardiner.com.au

DWG: WINDOWS, DOORS & PARTITIONS SCHEDULE
PROJECT: RETAIL/RESIDENTIAL DEVELOPMENT, 752 HIGH STREET, THORNBURY
DRAWN BY: AM
SCALE: 1:100 @ A1
JOB NO: 141211
DWG #: A.503
REV: D

SCHEDULE OF JOINERY FITTINGS, FITMENTS + EQUIPMENT

LEGEND:
BUILDER - SUPPLIED + INSTALLED BY CONTRACTORS
PROP - PROPRIETOR TO SUPPLY
PS - PROVISIONAL SUM; BUILDER TO SUPPLY + INSTALL

ROOM NAME / NO.	ITEM	PRODUCT	SUPPLIED BY:
JOINERY			
	GENERAL	AS DETAILED ON JOINERY DRAWINGS	BUILDER
APPLIANCES			
GENERAL	GENERAL	REFER TO SCHEDULE OF APPLIANCES	BUILDER + PROP
SANITARYWARE			
GENERAL	GENERAL	REFER TO SCHEDULE OF SANITARYWARE	BUILDER
HARDWARE			
CABINETRY	PULL HANDLES ETC	REFER SCHEDULE OF JOINERY HARDWARE (REFER ALSO JOINERY NOTES ON DRAWINGS FOR SCOPE)	PS
DOOR	HANDLES + LOCKS	REFER SCHEDULE OF DOOR HARDWARE (REFER ALSO DOOR SCHEDULE NOTES ON DRAWINGS FOR SCOPE)	PS
FITTINGS + EQUIPMENT			
BATH	MIRROR	AS DETAILED	BUILDER
	SHOWER SCREEN	AS DETAILED	BUILDER
KITCHEN	RANGHOOD	REFER SCHEDULE OF APPLIANCES	BUILDER
	COOK TOP/OVEN	REFER SCHEDULE OF APPLIANCES	BUILDER
	DISHWASHER	REFER SCHEDULE OF APPLIANCES	BUILDER
	FRIDGE	REFER SCHEDULE OF APPLIANCES	PROP
LAUNDRY	WASHING MACHINES	REFER SCHEDULE OF APPLIANCES	PROP
	DRYERS	REFER SCHEDULE OF APPLIANCES	PROP
WALL TILES + SPLASHBACKS			
LAUNDRY	SPLASHBACK	REFER SCHEDULE OF TILES	BUILDER
	FLOOR TILES WHERE APPLICABLE	REFER SCHEDULE OF TILES	BUILDER
BATHROOMS	WALL TILES	REFER SCHEDULE OF TILES	BUILDER
	FLOOR TILES	REFER SCHEDULE OF TILES	BUILDER
KITCHEN	WALL TILES	REFER SCHEDULE OF TILES	BUILDER
	FLOOR TILES WHERE APPLICABLE	REFER SCHEDULE OF TILES	BUILDER

JOINERY NOTES

GENERAL

1. READ IN CONJUNCTION WITH CONTRACT SPECIFICATION
2. CONFIRM ALL MEASUREMENTS PRIOR TO MANUFACTURE
3. SPECIFIC SPECIFICATION
   - ALL VERTICAL LAMINATE SURFACES ARE ASSUMED PRE-FINISHED U.O.N.
   - ALL BENCHTOP LAMINATE SURFACES ARE TO HAVE 1.2mm LAMINATE APPLIED TO MAR SUBSTRATE
   - SQUARE EDGING TO LAMINATE BOARD TO BE MATCHING COLOUR 2mm ABS EDGES
   - DOOR HINGES TO BE BLUM OR SIMILAR 170° U.O.N.
   - LEADING EDGES OF CARCASS TO MATCH DOOR FACE COLOUR;
   - INTERNAL NON-EXPOSED SURFACES TO BE WHITE MELAMINE 16mm THICK TO APARTMENTS 1, 4, 5, 8, 9, 12 AND BLACK MELAMINE TO APARTMENTS 2, 3, 6, 7, 10, 11, 13.
   - PANTRY INTERNALS TO BE LAMINATE AS SHOWN (NOT MELAMINE)
   - COLOUR TO MATCH EXPOSED LAMINATE
   - BACKS TO BE 16mm MELAMINE
   - VENEER PANELS - BUILDER TO ALLOW FOR VENEER TO BE APPLIED TO NOM. 16mm BOARD AND FINISHED WITH MATTE POLYURETHANE SURFACE TREATMENT OR PREFINISHED
   - REFER TO SEPARATE 'SCHEDULE OF JOINERY FINISHES' DOCUMENT FOR SELECTION SPECIFICATION

APPLIANCES

1. CHECK SIZES OF ALL APPLIANCES & EQUIPMENT & ALLOW APPROPRIATE CLEARANCES PRIOR TO MANUFACTURE
2. BUILDER TO INSTALL ALL APPLIANCES IN ACCORDANCE WITH MANUFACTURERS INSTRUCTIONS

STONEWORK

BUILDER TO ALLOW TO PROVIDE TEMPLATE FOR STONE CONTRACTORS WHERE APPLICABLE

CABINET + DRAWER HARDWARE

1. CABINET HARDWARE SUPPLY SUBJECT TO PROVISIONAL SUMS, INSTALLED BY BUILDER
2. BUILDER TO ALLOW FOR INSTALLATION OF ALL JOINERY.
3. ALL DRAWER RUNNERS TO BE 'BLUM TANDEM' RUNNER SYSTEM WITH 'BLUMOTION' SOFT-CLOSING MECHANISM

JOINERY LEGEND

CR	PULL UP CLOTHES RACK	LB	LAUNDRY BASKET
AS	ADJUSTABLE SHELF	FS	FIXED SHELF
OS	OPEN SHELF	CSD	CAVITY SLIDING DOOR
FP	FIXED PANEL	DW	DISH WASHER
FR	FRIDGE	DR	DRAWER
CPD	CUPBOARD	WM	WASHING MACHINE
TD	TUMBLE DRYER	BA	HAND BASIN
TRH	TOILET ROLL HOLDER	TR	TOWEL RAIL
TRG	TROUGH	CT	COOK TOP
MC	MIRROR CABINET	WB	WASH BASIN
V	VANITY	SD	SLIDING DOOR
HR	HANGING RAIL	MIRR	MIRROR
BH	BULKHEAD	HTR	HEATED TOWEL RAIL
HT	HAND TOWEL HOLDER	HK	HOOK
HD	HAND DRYER		

SS	STAINLESS STEEL	PA1	SELECTED PAINT FINISH
VEN1	SELECTED VENEER	LAM1	SELECTED LAMINATE
TIL1	SELECTED TILE	VIN1	SELECTED VINYL
STO1	SELECTED STONE	PLY	SELECTED PLYWOOD
FP1	FACTORY PAINT FINISH	MIRR	MIRROR (to detail)
FP2	AS FP1 ON SPLIT BATT	CSPL	COLOURBACK GLASS SPLASHBACK
CGP	COLOUR GLASS PANEL	CG	CLEAR GLASS
TIM	SOLID TIMBER	MELA	BLACK MELAMINE
CONC	CONCRETE SURFACE	TIM(FF)	SOLID KDHW TIMBER (STAINED TO MATCH FLOORING)

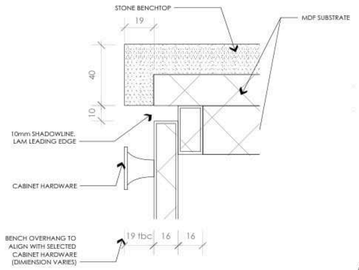

A1 JOINERY DETAIL A - TYPICAL STONE BENCH EDGE
1:2

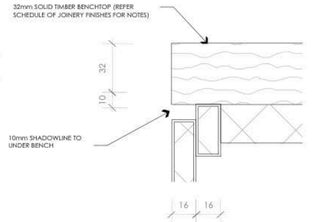

A2 JOINERY DETAIL A - TYPICAL TIMBER BENCH EDGE
1:2

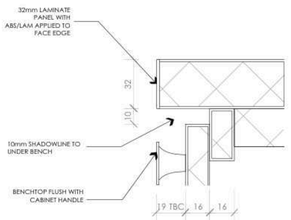

A3 JOINERY DETAIL A - TYPICAL LAMINATE BENCH EDGE
1:2

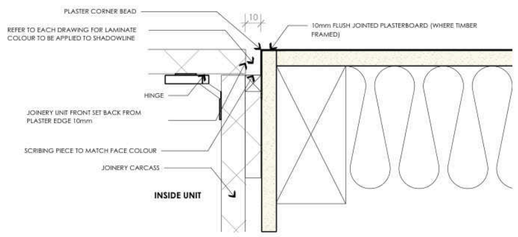

B JOINERY DETAIL B - JOINERY SHADOWLINE (JAMB)
1:2

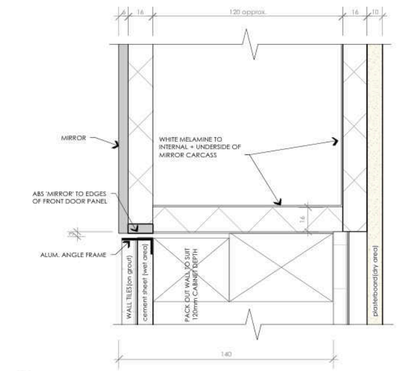

C JOINERY DETAIL C - RECESSED CABINET (MIRRORED)
1:2

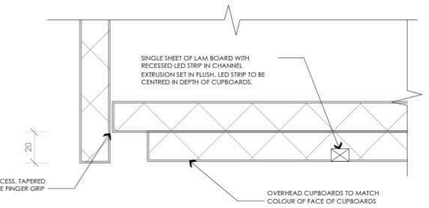

D JOINERY DETAIL D - OVERHEAD CUP'D'S FINGER PULL
1:2

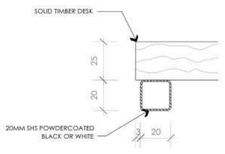

E JOINERY DETAIL E - TIMBER DESK EDGE
1:2

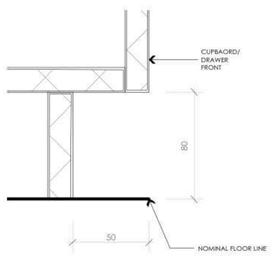

F1 JOINERY DETAIL F - KICKER TYPE 1
1:1

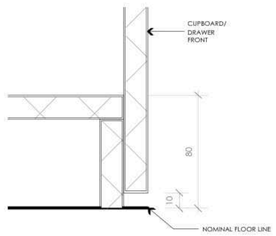

F2 JOINERY DETAIL F - KICKER TYPE 2
1:1

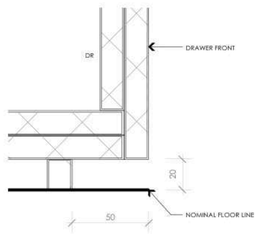

F3 JOINERY DETAIL F - KICKER TYPE 3
1:1

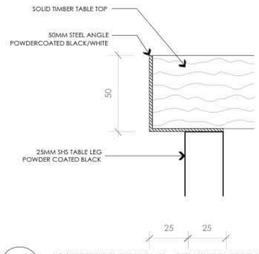

G JOINERY DETAIL F - TIMBER TABLE EDGE
1:2

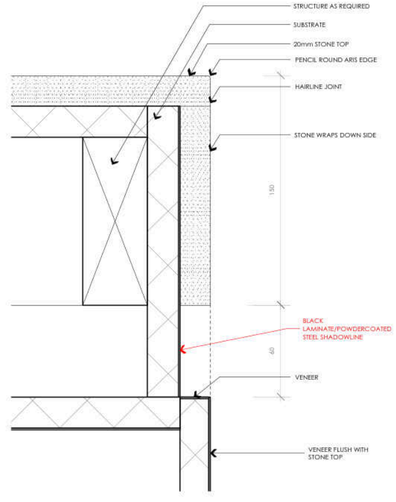

H JOINERY DETAIL H - ISLAND BENCH EDGE
1:5

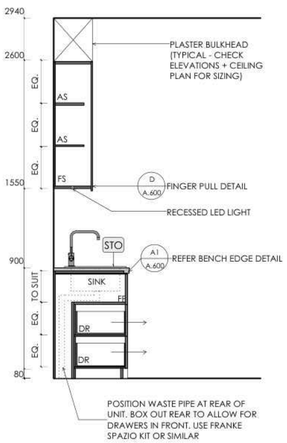

I JOINERY DETAIL I - KITCHEN SINK (TYPICAL)
1:25

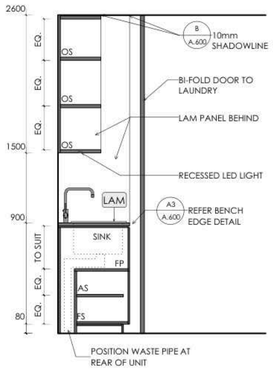

J JOINERY DETAIL J - LAUNDRY (TYPICAL)
1:25

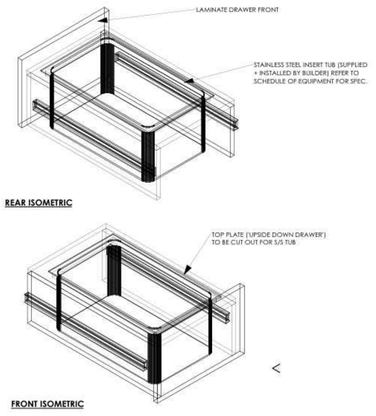

K JOINERY DETAIL L - COMPOST DRAWER
1:10

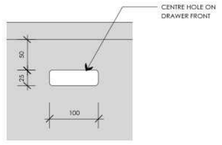

L JOINERY DETAIL L - CUT OUT DRAWER
1:5

FOR CONSTRUCTION - 17/12/19

ISSUE	DATE	REVISION
D	17/12/19	FOR CONSTRUCTION
C	31/5/19	CONTRACT SET

This drawing to be read in conjunction with the other contract documents including the Specification. Any discrepancies found in these documents during the course of the contract, Contractor must notify all dimensions on site before commencing any work. Do not scale any dimensions from drawings. Allow for thickness of construction and all finishes.

CLIENT H.CHARALAMBOUS

Gardiner Architects
7/252 St Georges Rd, Fitzroy North, VIC, 3068
Ph: (03) 9486 4092 E: info@paulgardiner.com.au

DWG **JOINERY SCHEDULE & TYPICAL DETAILS**
PROJECT RETAIL/RESIDENTIAL DEVELOPMENT
752 HIGH STREET, THORNBURY

JOB NO 141211
DRAWN BY AM
SCALE 1:100
DWG # A.600
REV # D

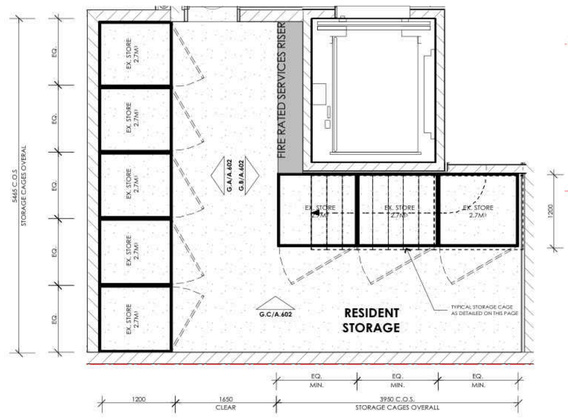

1 GROUND FLOOR - STORAGE CAGE
SCALE: 1:50

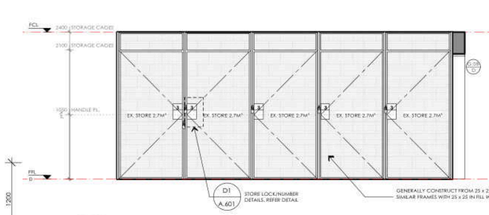

G.A GROUND FLOOR - ELEVATION
SCALE: 1:50

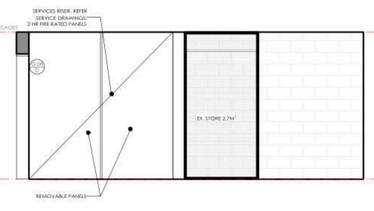

G.B GROUND FLOOR - ELEVATION
SCALE: 1:50

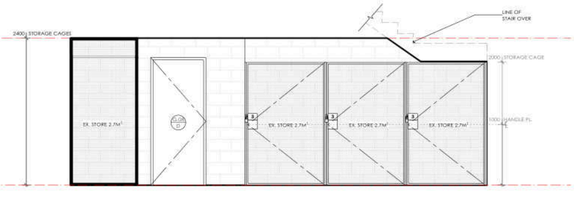

G.C GROUND FLOOR - ELEVATION
SCALE: 1:50

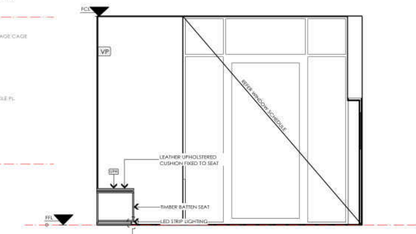

G.H GROUND FLOOR - ELEVATION
SCALE: 1:50

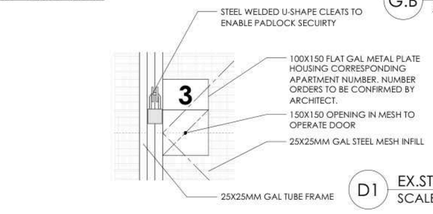

D1 EX.STORE LOCK/NUMBER DETAIL
SCALE: 1:10

JOINERY NOTES

1. READ IN CONJUNCTION WITH FINISHES PLAN A.205 + A.206
2. READ IN CONJUNCTION WITH STAIRWELL DETAILS A.411

LEGEND

TLB 2 INTERNAL TIMBER LINING BOARDS+ OIL FINISH (REFER A.109/A.110 FOR DETAILS +
VP VITRAPANEL (PRE-FINISHED CEMENT SHEET) REFER A.106 FOR DETAIL
UPH LEATHER UPHOLSTERY REFER SCHEDULES FOR PRODUCT

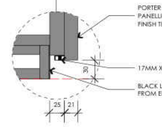

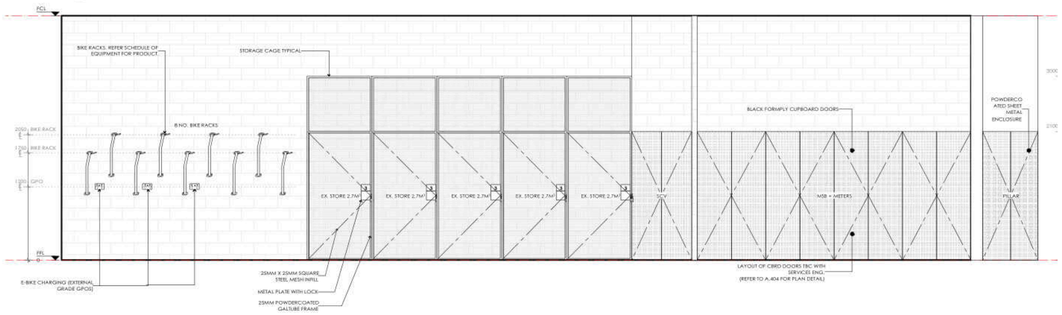

G.D GROUND FLOOR - ELEVATION
SCALE: 1:50

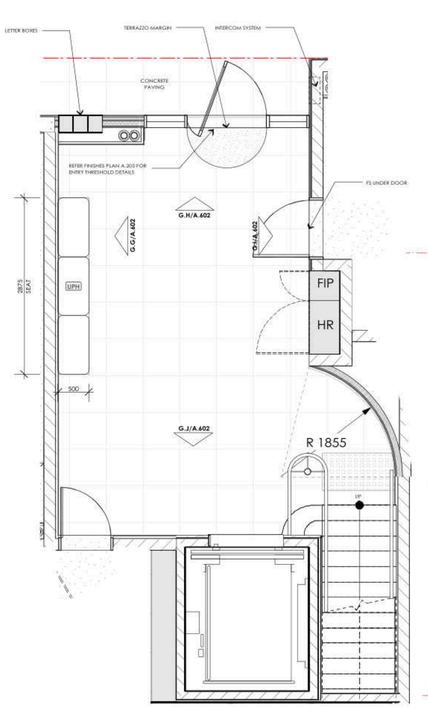

2 GROUND FLOOR - STORAGE CAGE
SCALE: 1:50

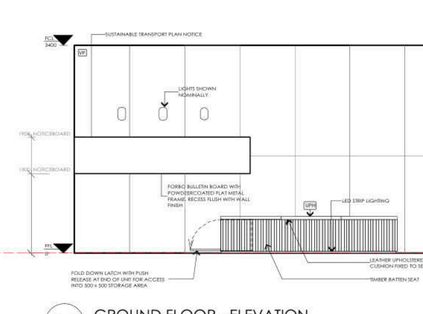

G.G GROUND FLOOR - ELEVATION
SCALE: 1:50

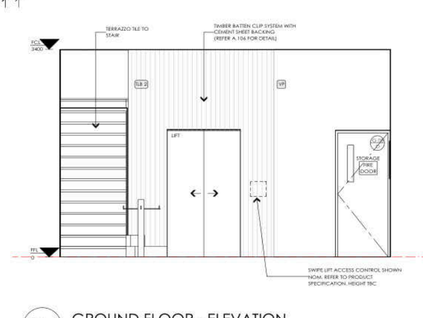

G.J GROUND FLOOR - ELEVATION
SCALE: 1:50

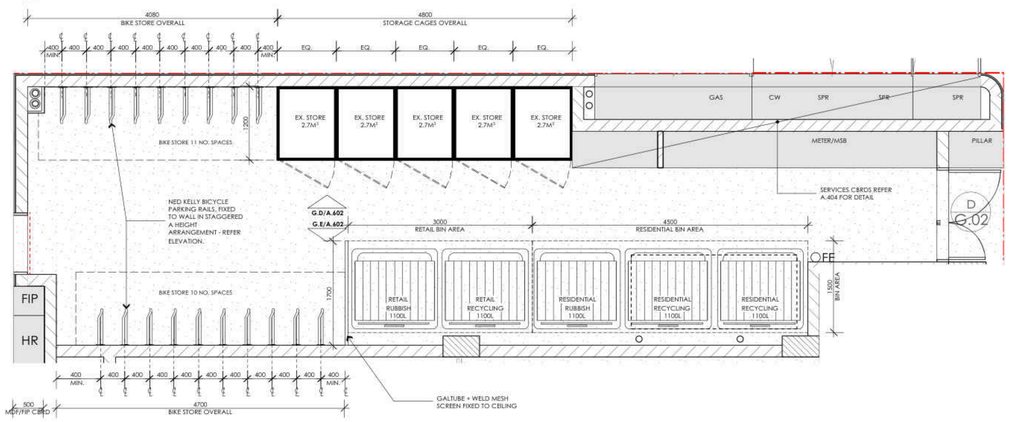

3 GROUND FLOOR - STORAGE CAGES + BIN AREA
SCALE: 1:50

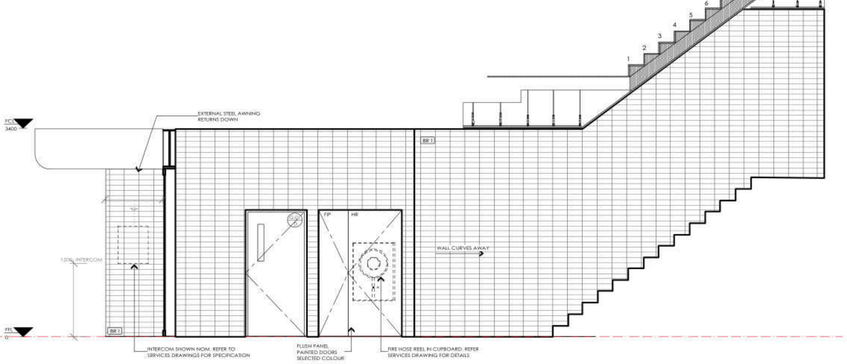

G.I GROUND FLOOR - ELEVATION
SCALE: 1:50

NOTES:

1. REFER TO A.205 FOR FLOOR FINISHES + THRESHOLD DETAILS
2. REFER TO SCHEDULES FOR SPECIFICATION OF LETTER BOXES + SIGNAGE

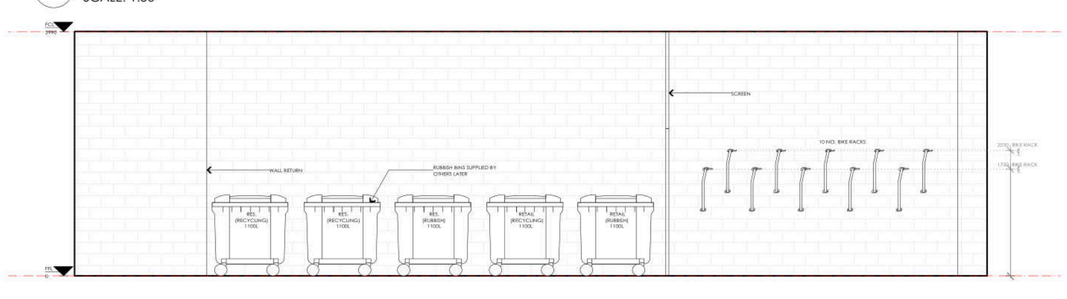

G.E GROUND FLOOR - ELEVATION
SCALE: 1:50

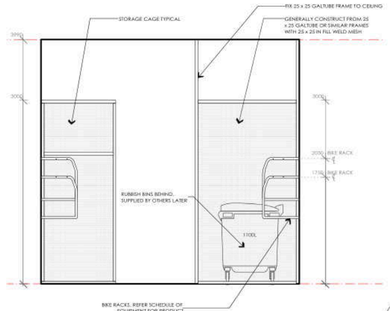

G.F GROUND FLOOR - ELEVATION
SCALE: 1:50

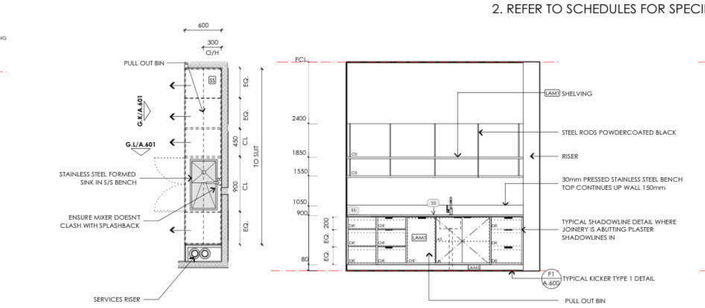

4 GROUND FLOOR - RETAIL KITCHENETTE
SCALE: 1:50

G.K GROUND FLOOR - RETAIL KITCHENETTE
SCALE: 1:50

G.L GROUND FLOOR - KITCHENETTE
SCALE: 1:50

FOR CONSTRUCTION - 17/12/19

ISSUE	DATE	REVISION
D	17/12/19	FOR CONSTRUCTION
C	31/5/19	CONTRACT SET

CLIENT H.CHARALAMBOUS

Gardiner Architects
7/252 St George's Rd, Fitzroy North, VIC, 3068.
Ph: (03) 9486 4092 E: info@paulgardiner.com.au

DWG **JOINERY PLANS & ELEVATIONS - LEVEL GR**
PROJECT RETAIL/RESIDENTIAL DEVELOPMENT
752 HIGH STREET, THORNBURY
DRAWN BY AM
SCALE AS SHOWN
JOB NO 141211
A.601
DWG # REV# D

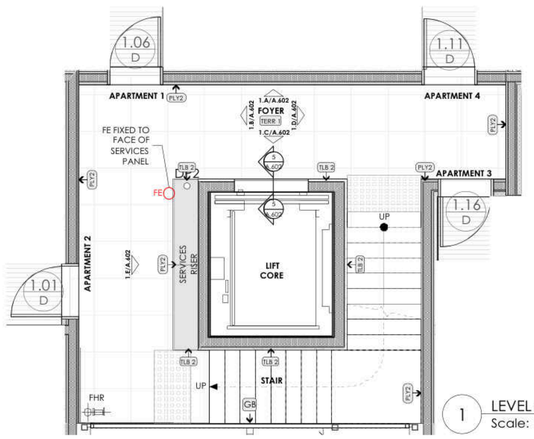

1 LEVEL 01 - FOYER
Scale: 1:50

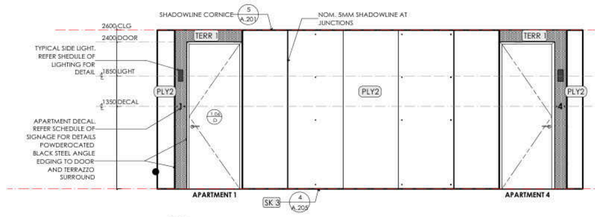

1A LEVEL 01 - FOYER
Scale: 1:50

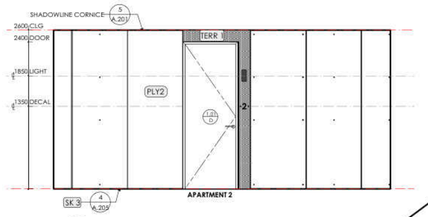

1B LEVEL 01 - FOYER
Scale: 1:50

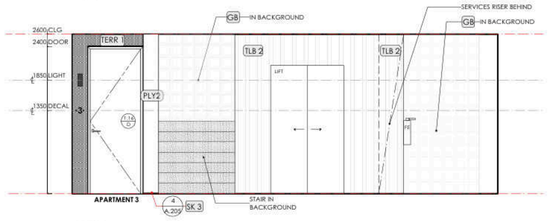

1C LEVEL 01 - FOYER
Scale: 1:50

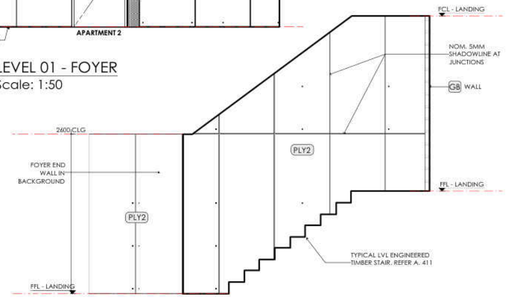

1/2D LEVEL 01 + 02 - FOYER
Scale: 1:50

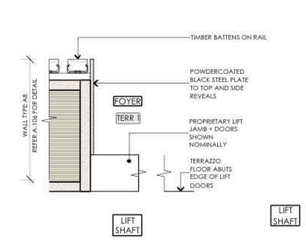

5 LIFT - TYPICAL REVEAL DETAIL
Scale: 1:5

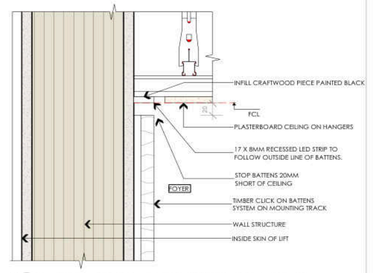

6 LIFT - TYPICAL LED LIGHTING DETAIL
Scale: 1:5

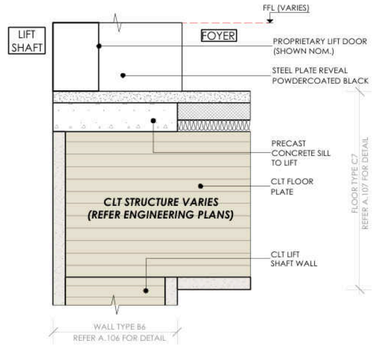

7 LIFT - TYPICAL THRESHOLD DETAIL
Scale: 1:4

JOINERY NOTES

1. READ IN CONJUNCTION WITH FINISHES PLAN A.205 + A.206
2. READ IN CONJUNCTION WITH STAIRWELL DETAILS A.411

LEGEND

- WALL LIGHT - REFER SCHEDULE OF LIGHTING
- APARTMENT NO. DECAL - REFER SCHEDULE OF SIGNAGE
- FE — FIRE EXTINGUISHER
- FHR — FIRE HOSE REEL
- TERR 1 — SELECTED TERRAZZO STONE TILE (600MM x 600MM x 15MM THICK NOM.) (REFER SCHEDULE OF FLOOR FINISHES FOR PRODUCT)
- PLY — PLYWOOD SHEET NOM. 2700 X 900 X 12MM THICK. 5MM GAPS NAILED TO SUBSTRATE (EXPOSED SMALL HEAD NAILS) SHADOWLINE AT SHEET JUNCTIONS. SANDED (PENCIL ROUND SHEET CORNERS) + OIL FINISH. REFER A. 109/A.110 FOR DETAILS + SCHEDULES FOR FINISHES)
- TLB 2 — INTERNAL TIMBER LINING BOARDS+ OIL FINISH (REFER A. 109/A.110 FOR DETAILS +
- SK 3 — SKIRTING TYPE 3 - FOYER SKIRTING (REFER TYPICAL SKIRTING DETAIL)
- GB — EXTERNAL GLASS BLOCK WALL
- VP — VITRAPANEL (PRE-FINISHED CEMENT SHEET) REFER A.106 FOR DETAIL.

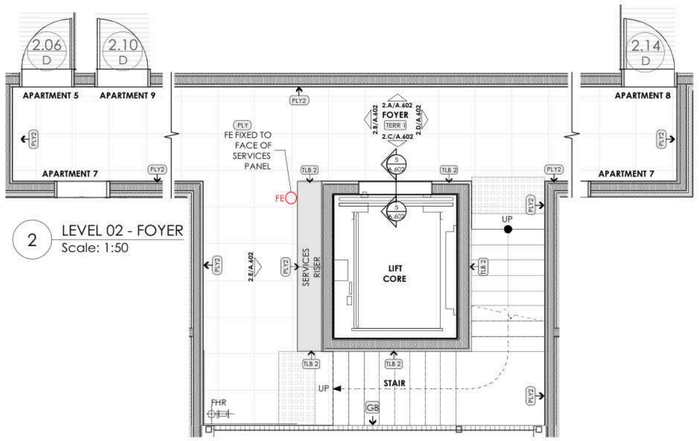

2 LEVEL 02 - FOYER
Scale: 1:50

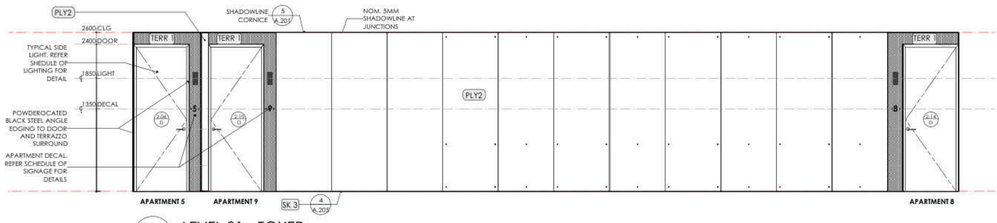

2A LEVEL 01 - FOYER
Scale: 1:50

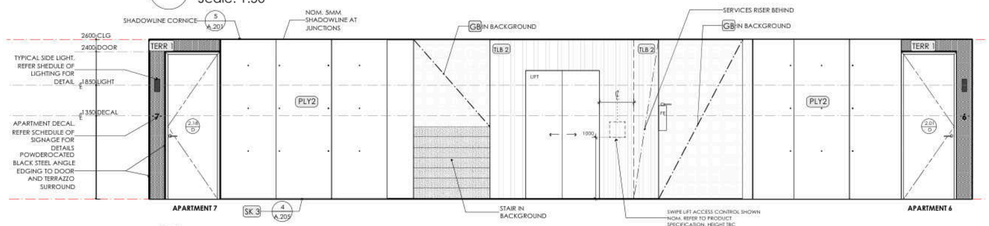

2C LEVEL 01 - FOYER
Scale: 1:50

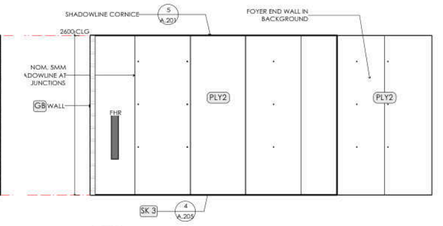

2B LEVEL 01 - FOYER
Scale: 1:50

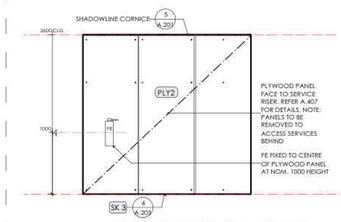

1/2/3/4 E LEVEL 01/02/03/04 - FOYER
Scale: 1:50

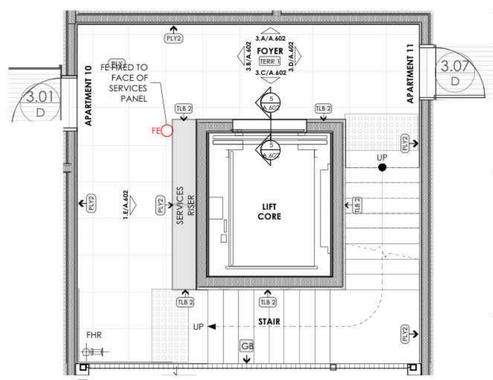

3 LEVEL 03 - FOYER
Scale: 1:50

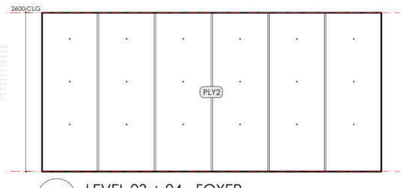

3/4A LEVEL 03 + 04 - FOYER
Scale: 1:50

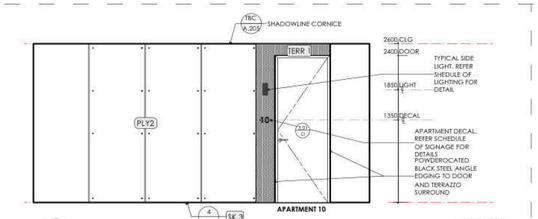

3B LEVEL 03 - FOYER
Scale: 1:50

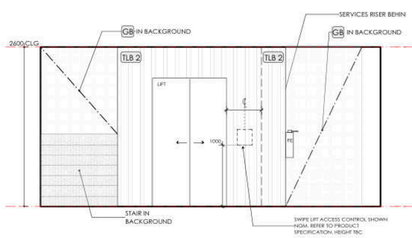

3/4C LEVEL 03 + 04 - FOYER
Scale: 1:50

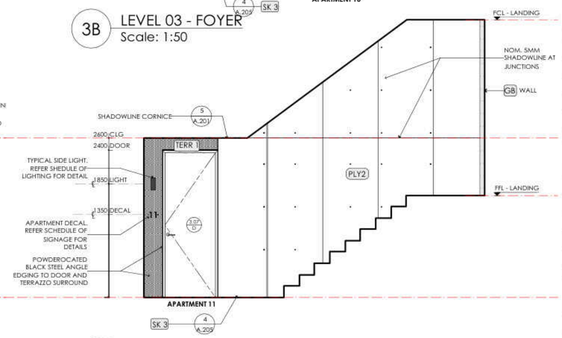

3D LEVEL 01 - FOYER
Scale: 1:50

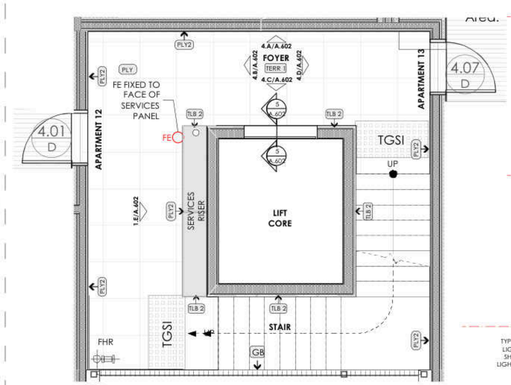

4 LEVEL 04 - FOYER
Scale: 1:50

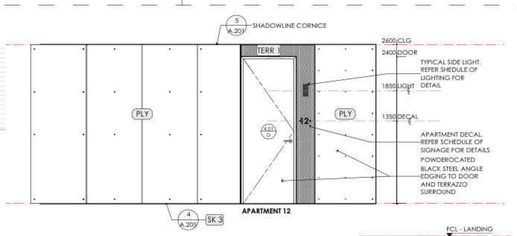

4A LEVEL 04 - FOYER
Scale: 1:50

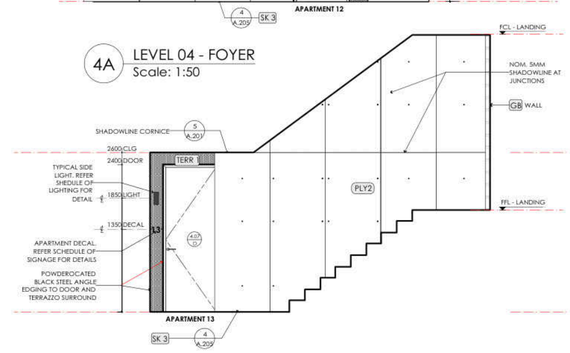

4D LEVEL 04 - FOYER
Scale: 1:50

FOR CONSTRUCTION - 17/12/19

ISSUE	DATE	REVISION
D	17/12/19	FOR CONSTRUCTION
C	31/5/19	CONTRACT SET

This drawing is to be read in conjuction with the other contract documents including the specification. All dimensions are to be verified on site during the course of the contract. Contractors must notify all dimensional discrepancies before proceeding with the work. Do not scale any dimensions from drawings. Any errors, omissions or discrepancies are to be reported to the architect.

CLIENT H.CHARALAMBOUS

Gardiner Architects
7/252 St Georges Rd, Fitzroy North, VIC, 3068
Ph: (03) 9486 4592 E: info@paulgardiner.com.au

DWG JOINERY PLANS & ELEVATIONS - FOYER LVL 01-05
PROJECT RETAIL/RESIDENTIAL DEVELOPMENT, 752 HIGH STREET, THORNBURY
DRAWN BY AM
SCALE 1:50 @ A1
JOB NO 141211
A.602
DWG #
REV# D

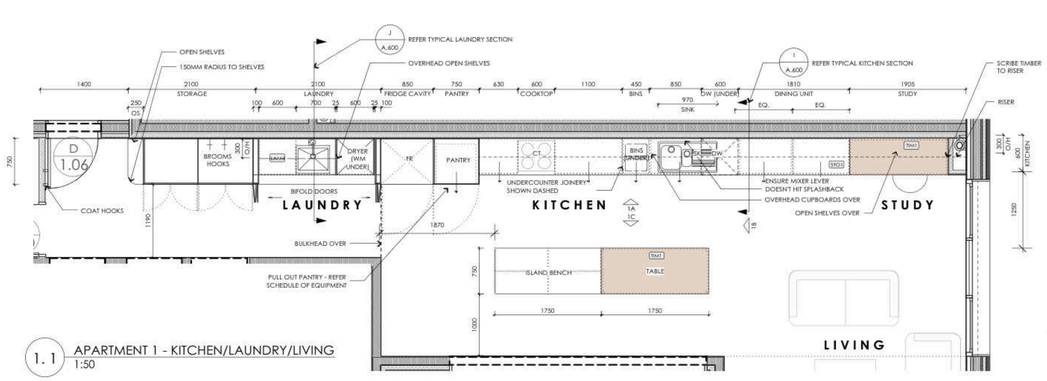

1.1 APARTMENT 1 - KITCHEN/LAUNDRY/LIVING
1:50

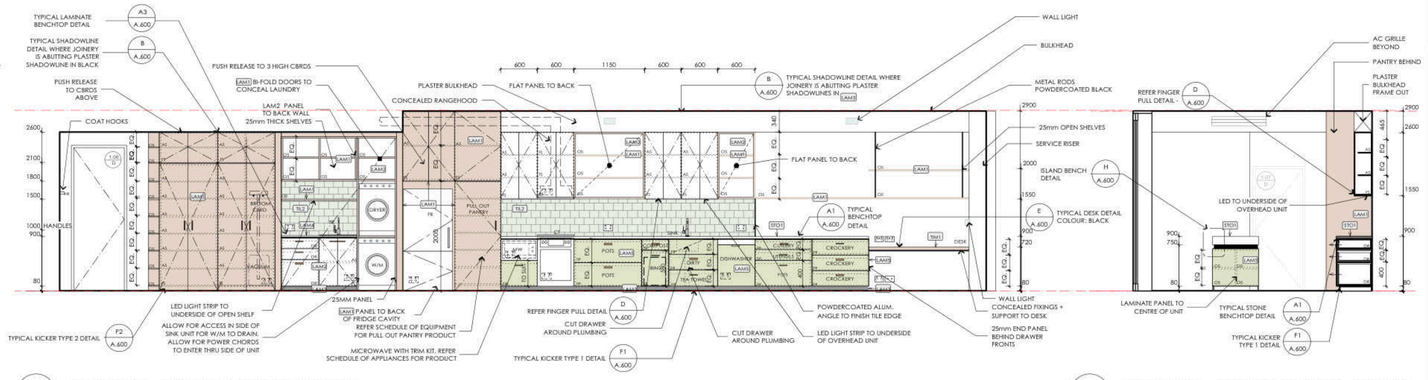

1A APARTMENT 1 - STORAGE, LAUNDRY + KITCHEN
1:50

1B APARTMENT 1 - STORAGE, LAUNDRY + KITCHEN
1:50

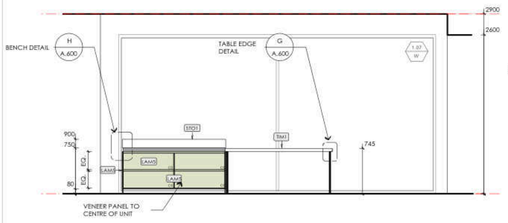

1C APARTMENT 1 - STORAGE, LAUNDRY + KITCHEN
1:50

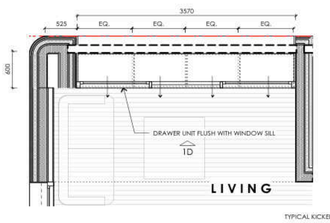

1. 2 APARTMENT 1 - LIVING
1:50

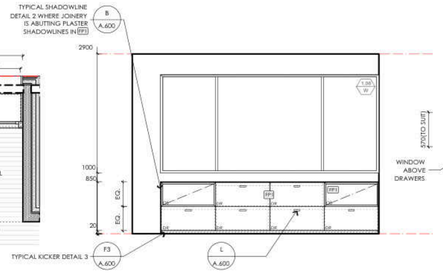

1D APARTMENT 1 - LIVING
1:50

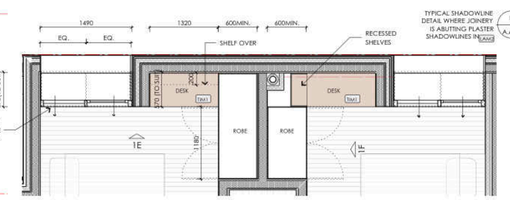

1. 3 APARTMENT 1 - BED 1 + 2
1:50

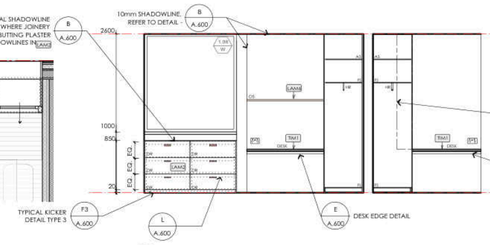

1E APARTMENT 1 - BED 1 + 2
1:50

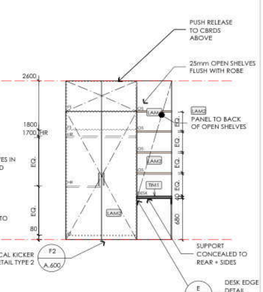

1F APARTMENT 1 - BED 1 + 2
1:50

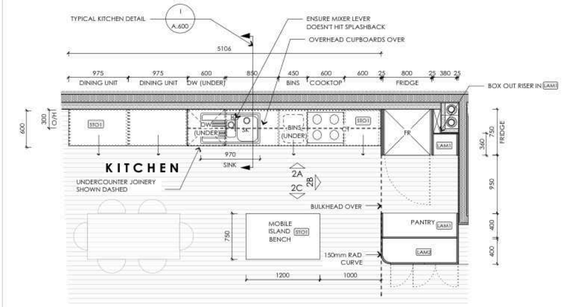

2. 1 APARTMENT 2 - KITCHEN
1:50

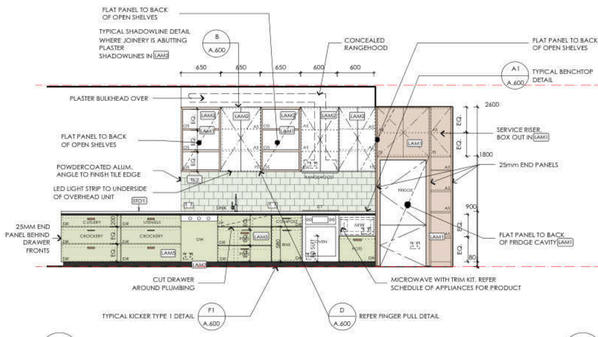

2A APARTMENT 2 - KITCHEN
1:50

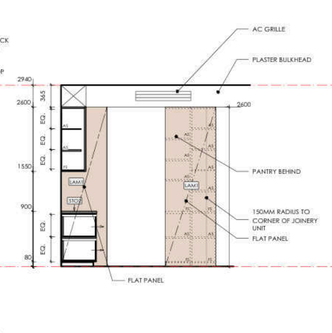

2B APARTMENT 2 - KITCHEN
1:50

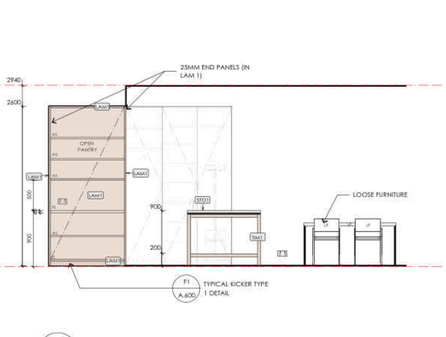

2C APARTMENT 2 - KITCHEN
1:50

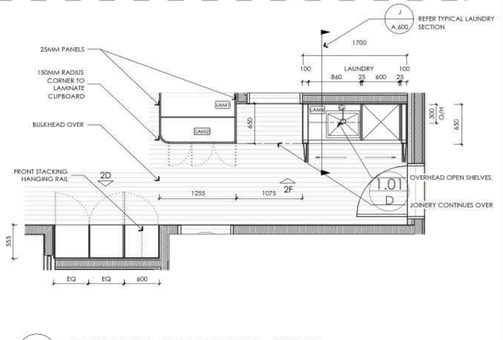

2. 4 APARTMENT 2 - STORAGE CBRD + LNDRY
1:50

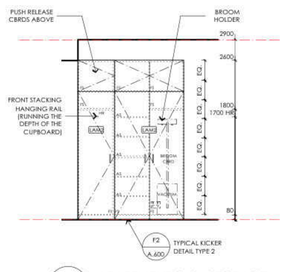

2D APARTMENT 2+3 - STORAGE
1:50

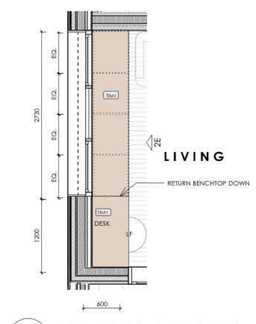

2. 3 APARTMENT 2 - STUDY/LIVING
1:50

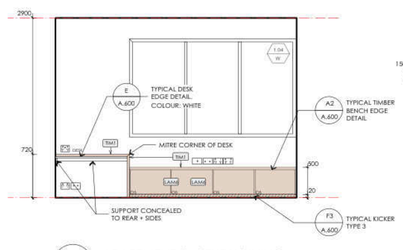

2E APARTMENT 2 - STUDY/LIVING
1:50

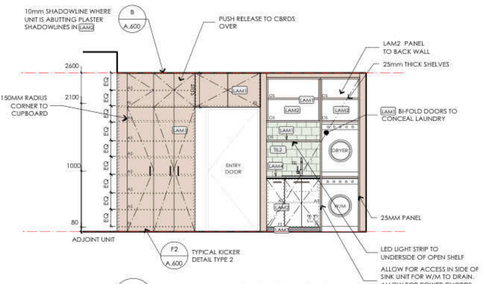

2F APARTMENT 2 - STORAGE CBRD
1:50

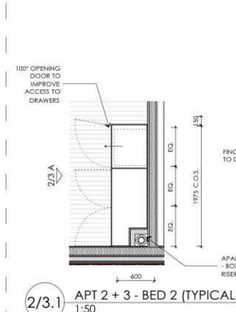

2/3.1 APT 2 + 3 - BED 2 (TYPICAL)
1:50

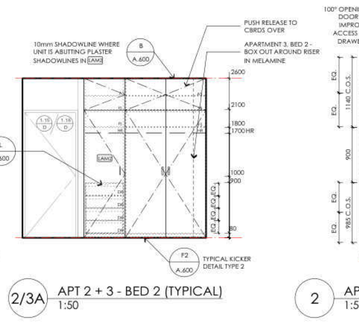

2/3A APT 2 + 3 - BED 2 (TYPICAL)
1:50

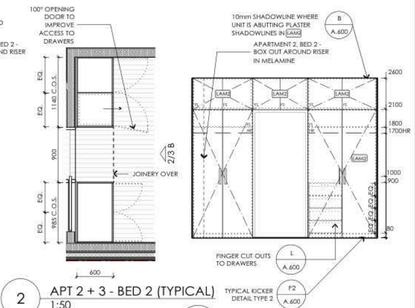

2 APT 2 + 3 - BED 2 (TYPICAL)
1:50

2/3B APT 2 + 3 - BED 1 (TYPICAL)
1:50

FOR CONSTRUCTION - 17/12/19

ISSUE	DATE	REVISION
D	17/12/19	FOR CONSTRUCTION
C	31/5/19	CONTRACT SET

This drawing is read in conjunction with the other architect documents including the specification and all relevant consultant's documents. Do not scale any dimensions from the drawing. Contractors must verify all dimensions on site before commencing any work or shop drawings. Report any discrepancies or omissions.

CLIENT H.CHARALAMBOUS

Gardiner Architects
7/252 St Georges Rd, Fitzroy North, VIC, 3068
Ph: (03) 9486 4592 E: info@paulgardiner.com.au

DWG JOINERY PLANS & ELEVATIONS - LEVEL 01
PROJECT RETAIL/RESIDENTIAL DEVELOPMENT
752 HIGH STREET, THORNBURY
DRAWN BY AM
SCALE 1:100
JOB NO 141211
A.603
DWG #
REV# D

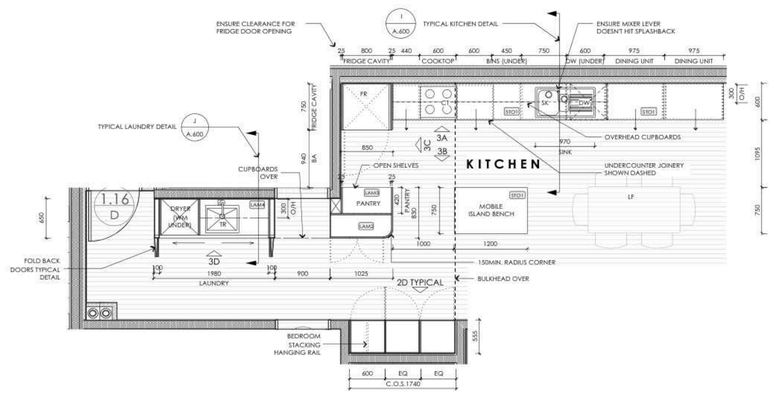

3.1 APARTMENT 3 - KITCHEN/LAUNDRY
1:50

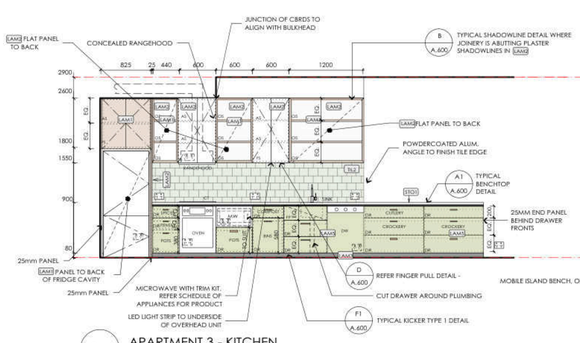

3A APARTMENT 3 - KITCHEN
1:50

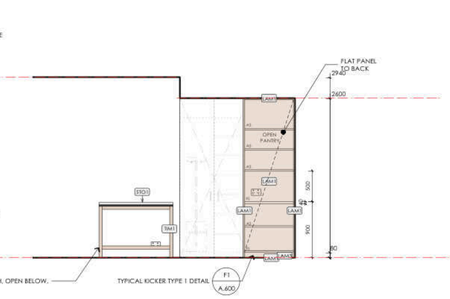

3B APARTMENT 3 - KITCHEN
1:50

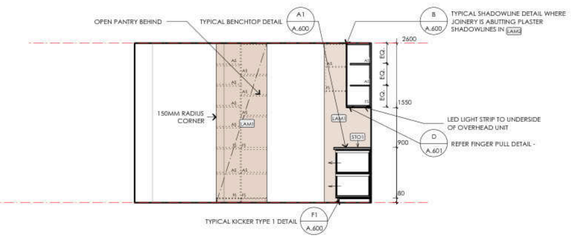

3C APARTMENT 3 - KITCHEN
1:50

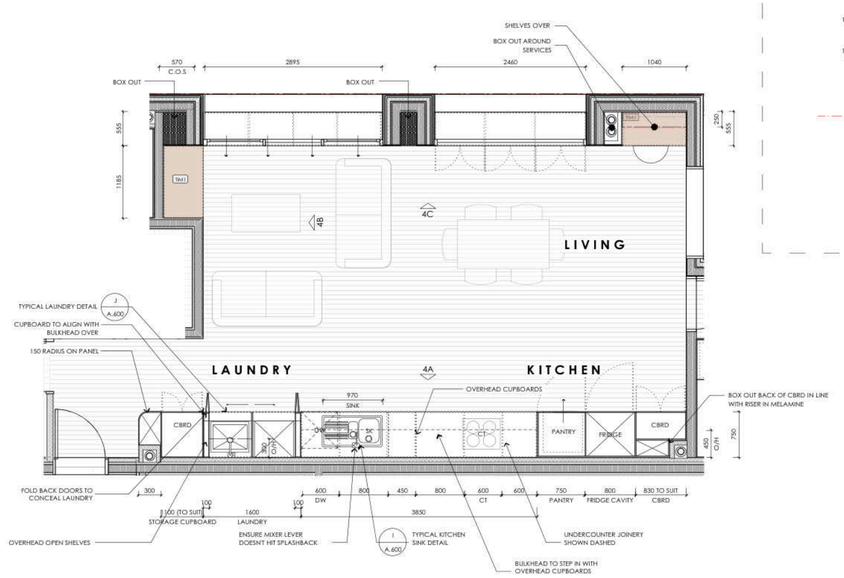

4. 1 APARTMENT 4 - KITCHEN/LAUNDRY/LIVING
1:50

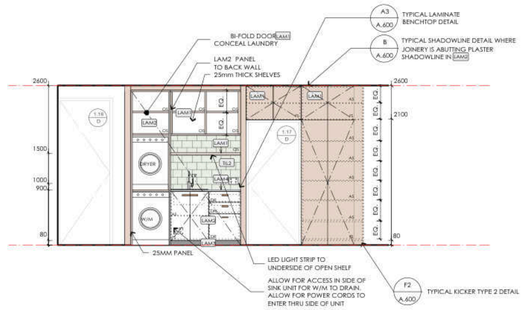

3D APARTMENT 3 - LAUNDRY/STORAGE
1:50

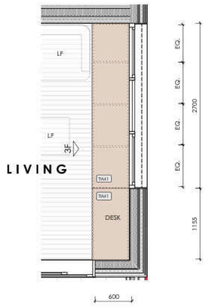

3. 2 APARTMENT 3 - STUDY/LIVING
1:50

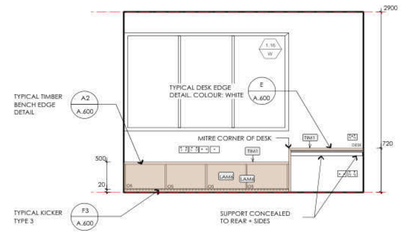

3F APARTMENT 3 - STUDY/LIVING
1:50

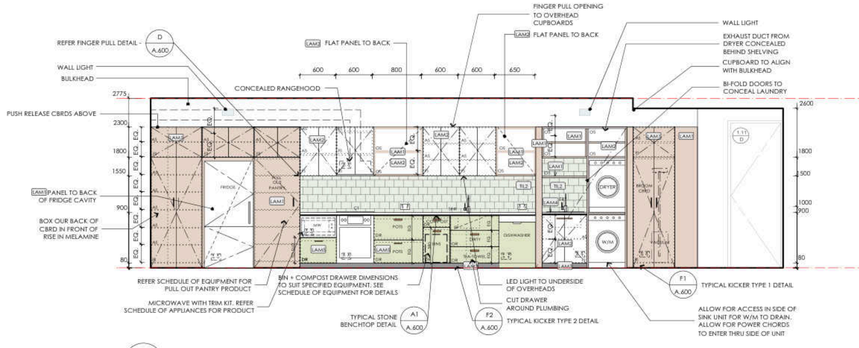

4A APARTMENT 4 - KITCHEN/LIVING
1:50

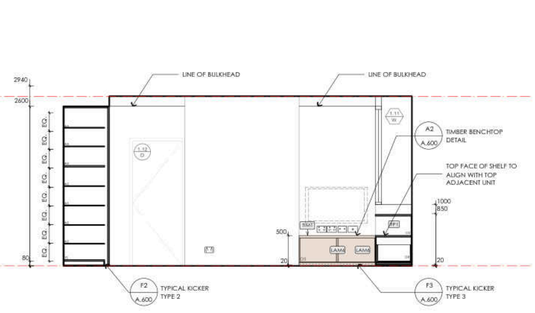

4B APARTMENT 4 - KITCHEN/LIVING
1:50

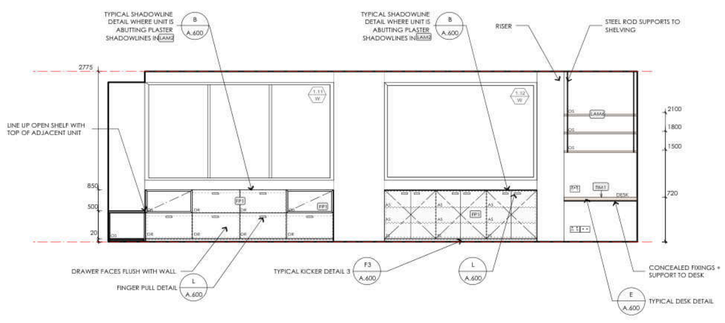

4C APARTMENT 4 - LIVING
1:50

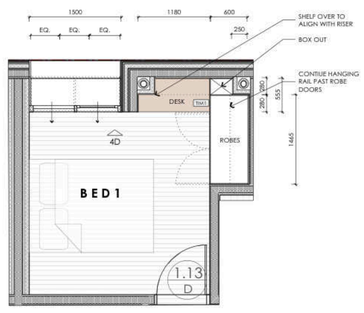

4. 2 APARTMENT 4 - BED 1
1:50

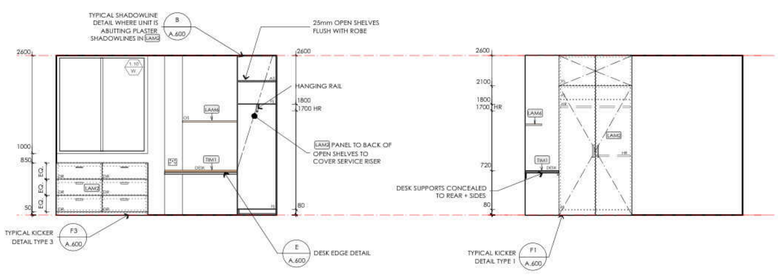

4D APARTMENT 4 - BED 1
1:50

4E APARTMENT 4 - BED 1
1:50

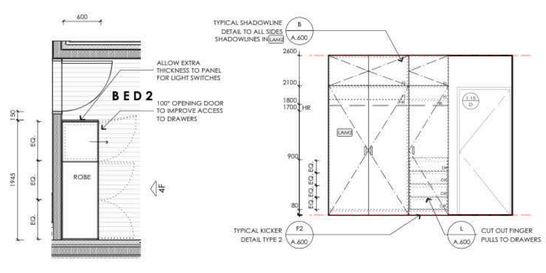

4. 3 APARTMENT 4 - BED 2
1:50

4F APARTMENT 4 - BED 2
1:50

FOR CONSTRUCTION - 17/12/19

ISSUE	DATE	REVISION
D	17/12/19	FOR CONSTRUCTION
C	31/5/19	CONTRACT SET

CLIENT: H.CHARALAMBOUS

Gardiner Architects
7/252 St George's Rd, Fitzroy North, VIC 3068
Ph: (03) 9486 4092, E: info@paulgardiner.com.au

DWG: JOINERY PLANS & ELEVATIONS - LEVEL 01 + LEVEL 02
PROJECT: RETAIL/RESIDENTIAL DEVELOPMENT, 752 HIGH STREET, THORNBURY
DRAWN BY: AM
SCALE: 1:100
JOB NO: 141211
A.604
DWG #
REV# D

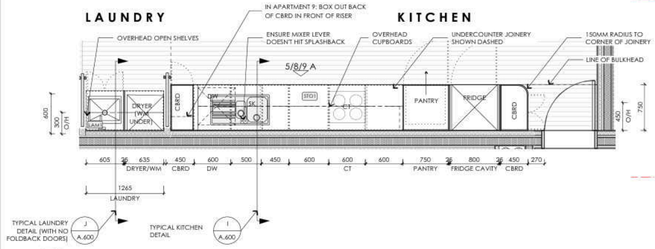

5/8/9. 1 APARTMENT 5/8/9 - KITCHEN/LAUNDRY (TYPICAL)
1:50

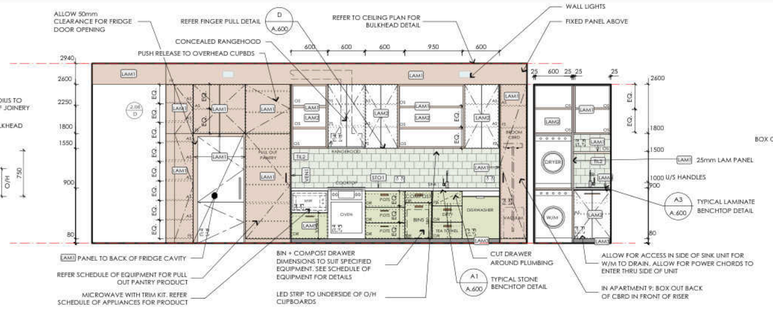

5/8/9A APARTMENT 5/8/9 - KITCHEN/LAUNDRY (TYPICAL)
1:50

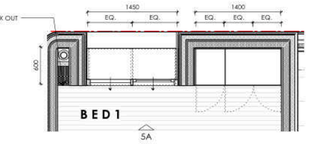

5.1 APARTMENT 5 - BED 1
1:50

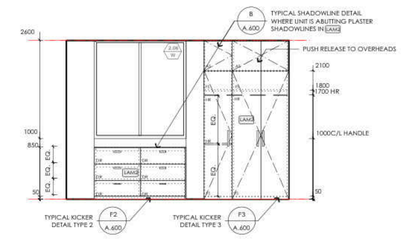

5A APARTMENT 5 - BED 1
1:50

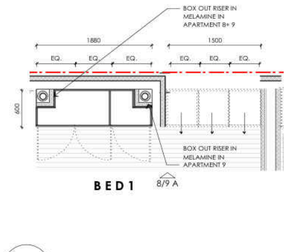

8/9. 1 APARTMENT 8/9 - BED 1 (TYPICAL)
1:50

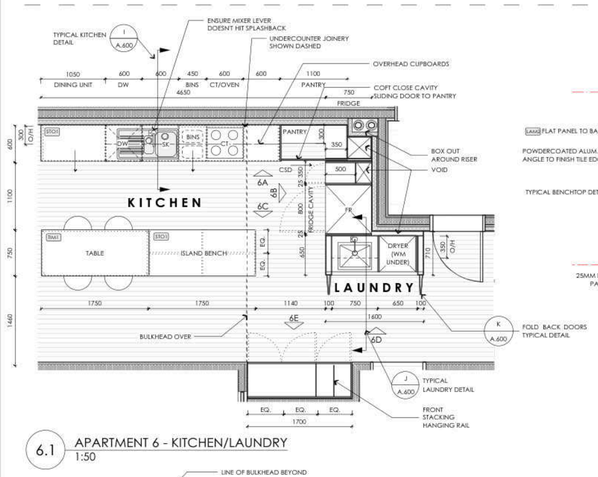

6.1 APARTMENT 6 - KITCHEN/LAUNDRY
1:50

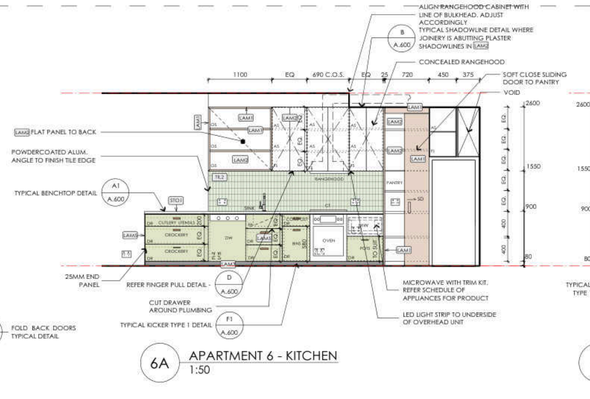

6A APARTMENT 6 - KITCHEN
1:50

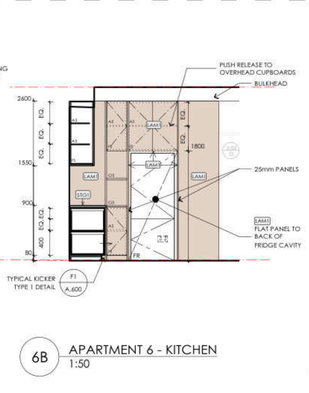

6B APARTMENT 6 - KITCHEN
1:50

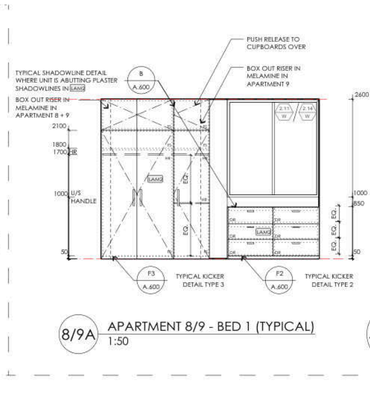

8/9A APARTMENT 8/9 - BED 1 (TYPICAL)
1:50

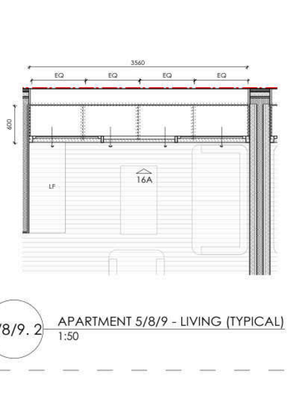

5/8/9. 2 APARTMENT 5/8/9 - LIVING (TYPICAL)
1:50

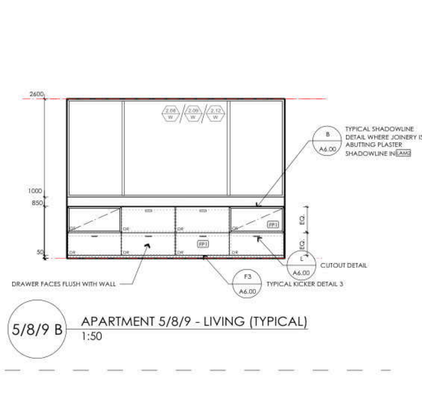

5/8/9 B APARTMENT 5/8/9 - LIVING (TYPICAL)
1:50

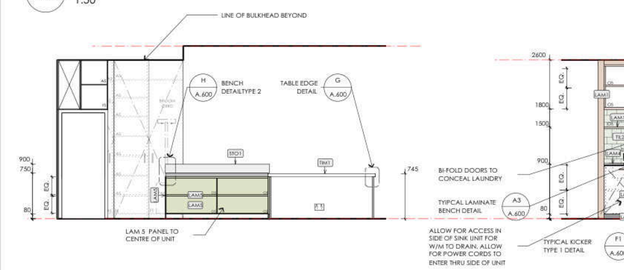

6C APARTMENT 6 - KITCHEN
1:50

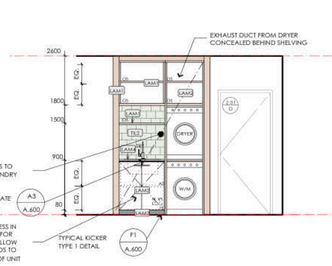

6D APARTMENT 6 - LAUNDRY
1:50

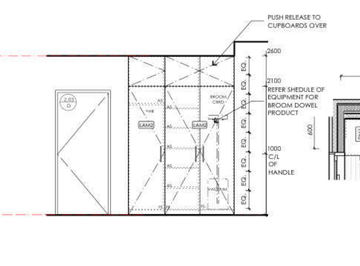

6E APARTMENT 6 - STORAGE
1:50

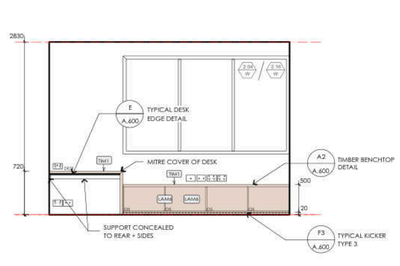

6/7. 1 APARTMENT 6 + 7 - LIVING (TYPICAL)
1:50

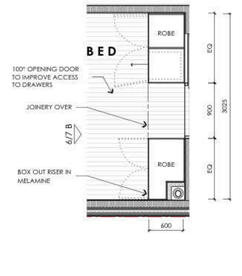

6/7 A APARTMENT 6 + 7 - LIVING (TYPICAL)
1:50

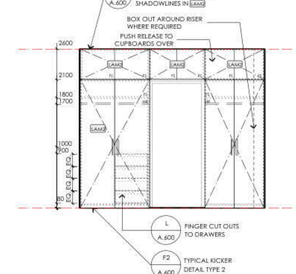

6/7. 2 APARTMENT 6 + 7 - BED 1 + 2 (TYPICAL)
1:50

6/7 B APT 6 + 7 - BED 1 + 2 (TYPICAL)
1:50

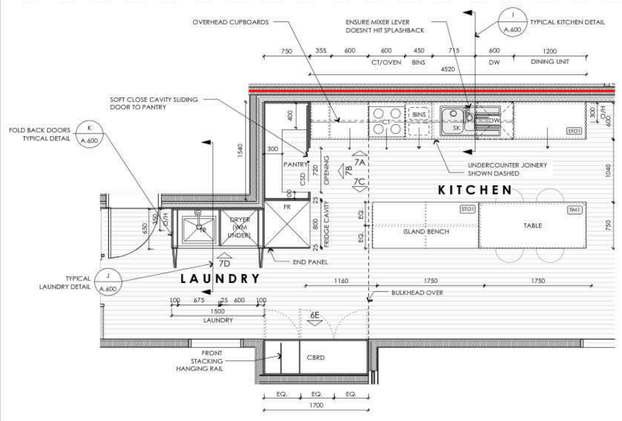

7.1 APARTMENT 7 - KITCHEN/LAUNDRY
1:50

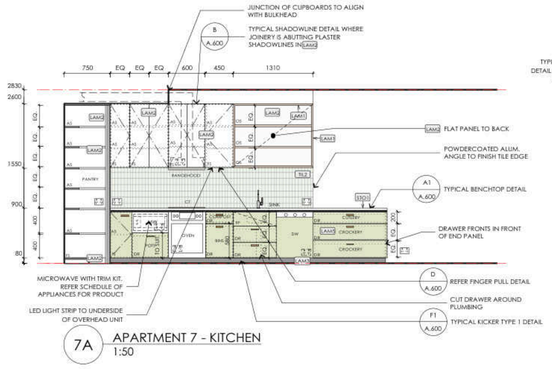

7A APARTMENT 7 - KITCHEN
1:50

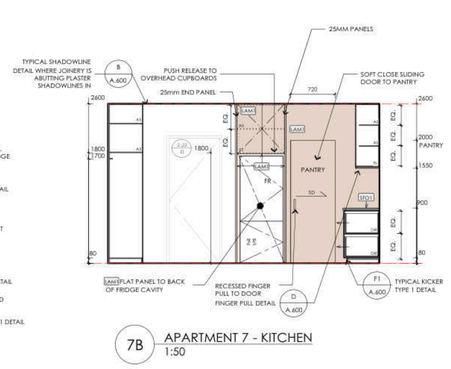

7B APARTMENT 7 - KITCHEN
1:50

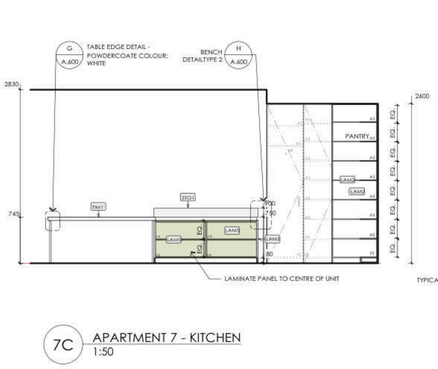

7C APARTMENT 7 - KITCHEN
1:50

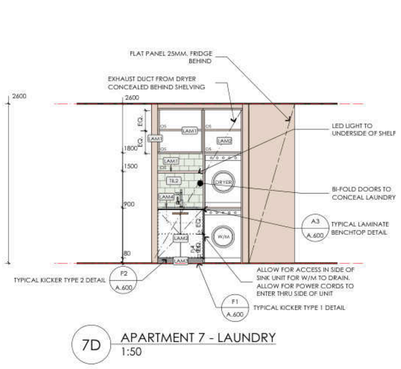

7D APARTMENT 7 - LAUNDRY
1:50

FOR CONSTRUCTION - 17/12/19

D	17/12/19	FOR CONSTRUCTION	
C	31/5/19	CONTRACT SET	
ISSUE	DATE	REVISION	

This drawing to require conjunction with the relevant project documentation, specification, project specification and any instructions issued during the course of the contract. Contractor to check all dimensions on site before commencing any work. Do not scale from drawing. Figured dimensions to be taken in preference to scaled measurements.

CLIENT H.CHARALAMBOUS

Gardiner Architects
7/252 St Georges Rd, Fitzroy North, VIC, 3068
Ph: (03) 9486 4092 E: info@paulgardiner.com.au

DWG JOINERY PLANS & ELEVATIONS - LEVEL 02 + LEVEL 03
JOB NO 141211
PROJECT RETAIL/RESIDENTIAL DEVELOPMENT
752 HIGH STREET, THORNBURY
DRAWN BY AM
SCALE 1:100
DWG # A.605
REV# D

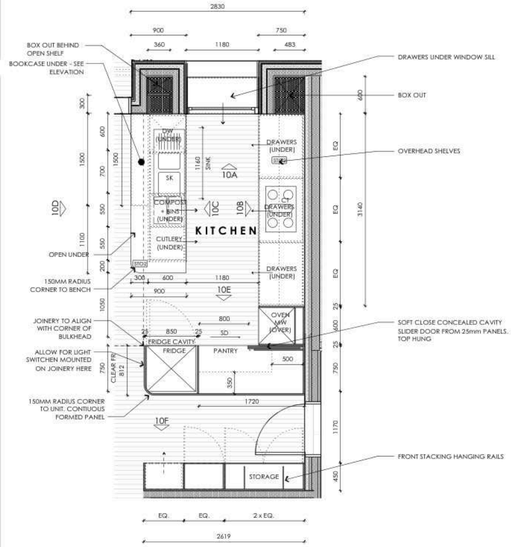

10. 1 APARTMENT 10 - KITCHEN/STORAGE
1:50

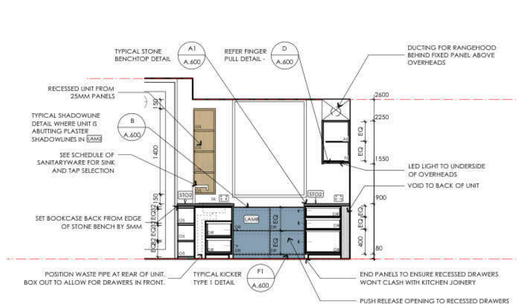

10A APARTMENT 10 - KITCHEN
1:50

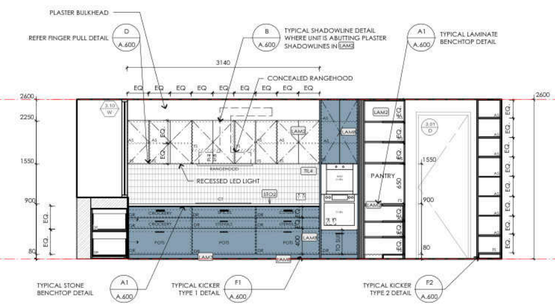

10B APARTMENT 10 - KITCHEN
1:50

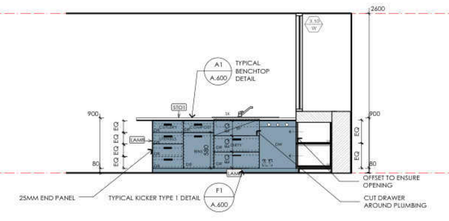

21C APARTMENT 10 - KITCHEN
1:50

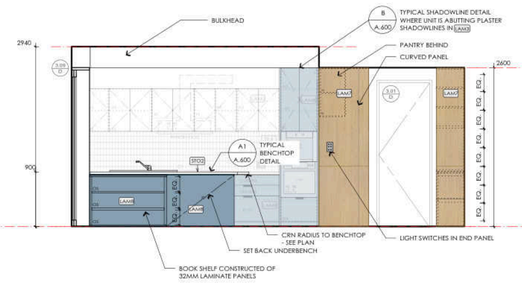

10D APARTMENT 10 - KITCHEN
1:50

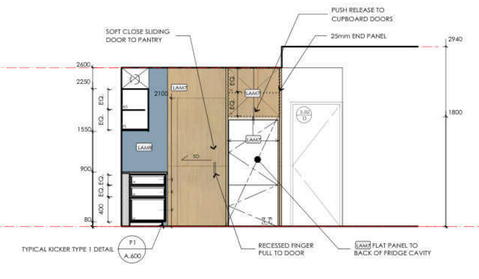

10E APARTMENT 10 - KITCHEN
1:50

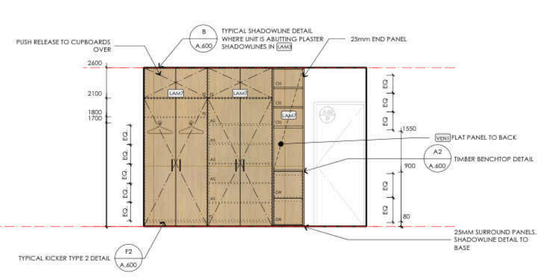

10F APARTMENT 10 - STORAGE
1:50

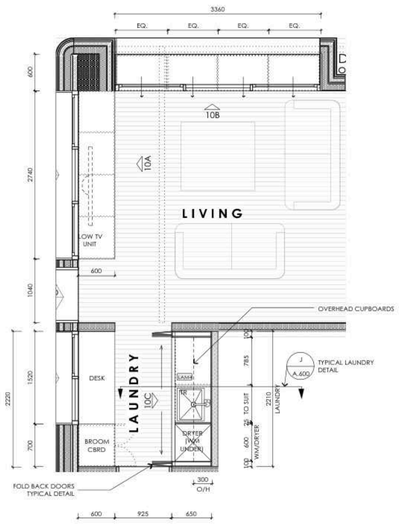

10.2 APARTMENT 10 - LIVING/LAUNDRY
1:50

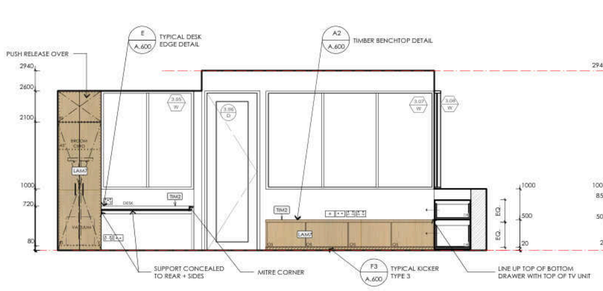

10A APARTMENT 10 - LIVING/LAUNDRY
1:50

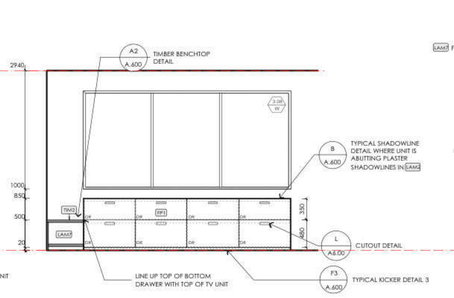

10B APARTMENT 10 - LIVING/LAUNDRY
1:50

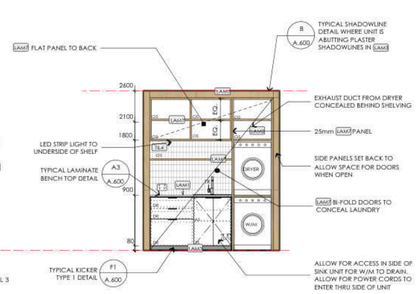

10C APARTMENT 10 - LIVING/LAUNDRY
1:50

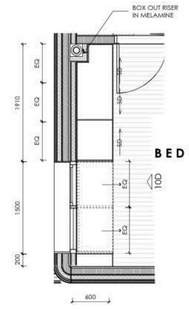

10. 2 APARTMENT 10 - BED 1
1:50

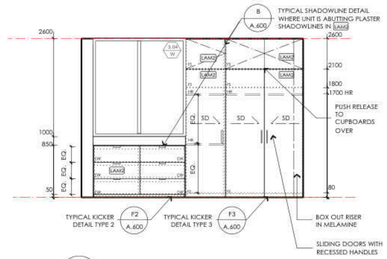

10D APARTMENT 10 - BED 1
1:50

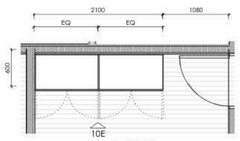

10. 4 APARTMENT 10 - BED 2
1:50

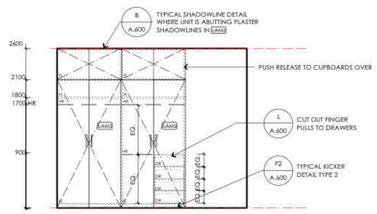

10E APARTMENT 10 - BED 2
1:50

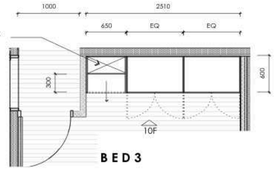

10. 4 APARTMENT 10 - BED 3
1:50

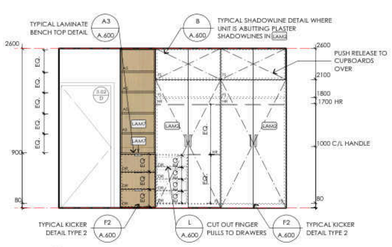

10F APARTMENT 10 - BED 3
1:50

FOR CONSTRUCTION - 17/12/19

This drawing is read in conjunction with the project specification and any instructions issued during the course of the contract. Contractor to verify all dimensions on site before commencing any work. Do not scale any dimensions from this drawing. Refer to Architectural drawings as required.

ISSUE	DATE	REVISION
D	17/12/19	FOR CONSTRUCTION
C	31/5/19	CONTRACT SET

CLIENT H.CHARALAMBOUS

Gardiner Architects
77252 St George's Rd, Fitzroy North, VIC, 3068
Ph: (03) 9486 4092 E: info@paulgardiner.com.au

DWG JOINERY PLANS & ELEVATIONS - LEVEL 03 + LEVEL 04
PROJECT RETAIL/RESIDENTIAL DEVELOPMENT 752 HIGH STREET, THORNBURY
DRAWN BY AM
SCALE 1:100
JOB NO 141211
A.606
DWG # REV# D

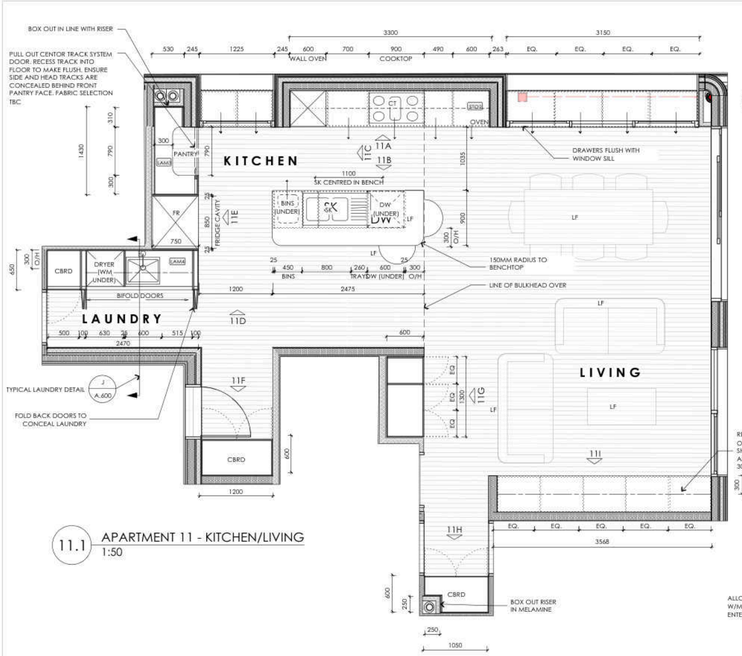

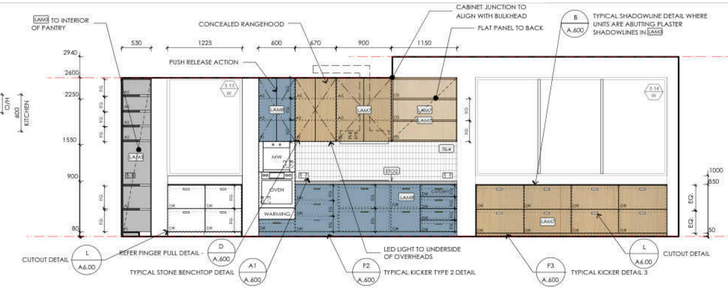

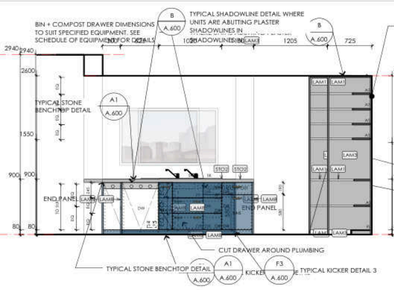

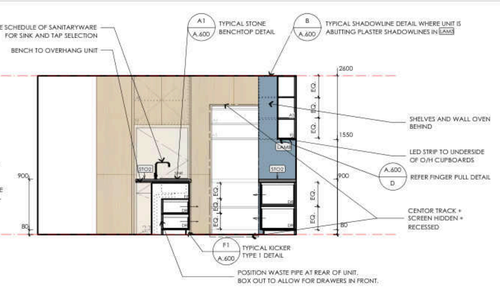

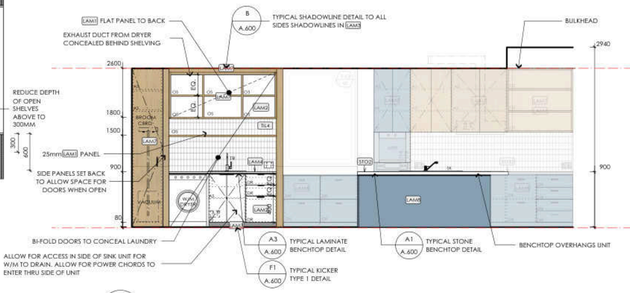

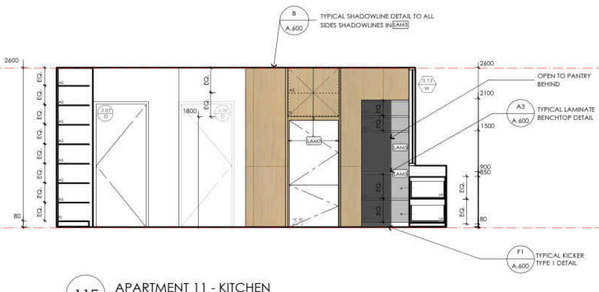

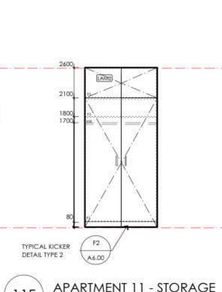

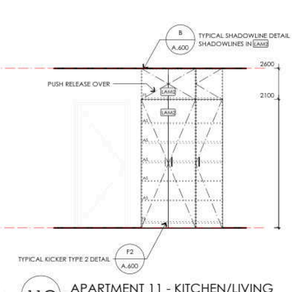

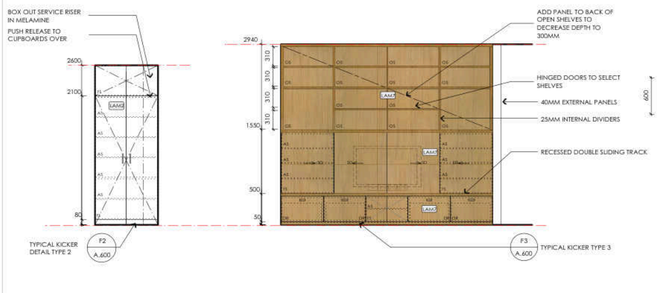

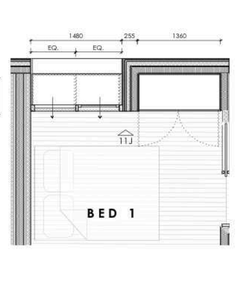

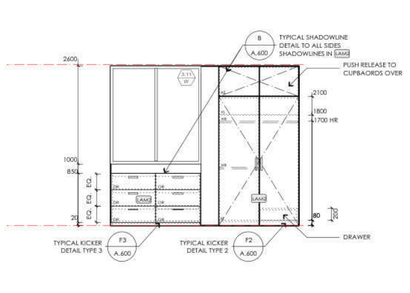

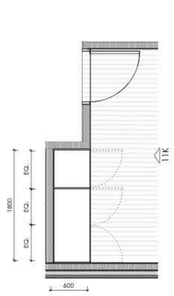

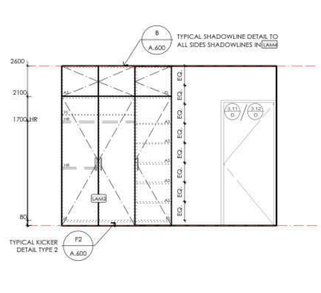

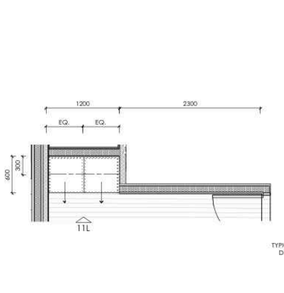

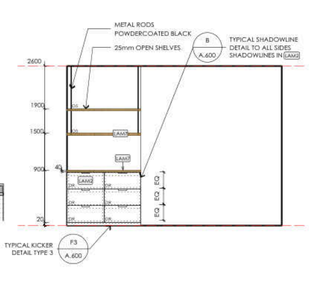

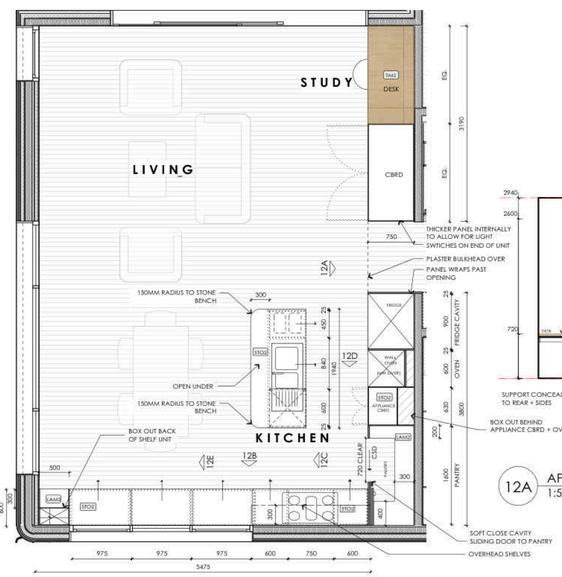

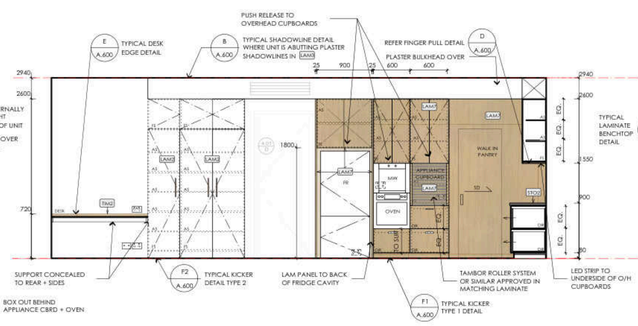

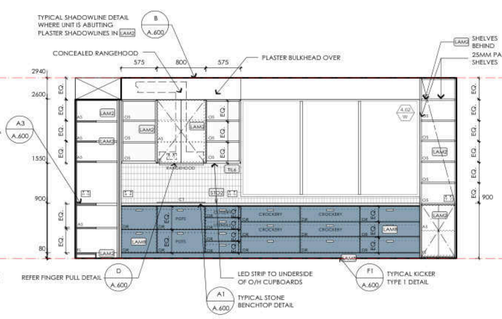

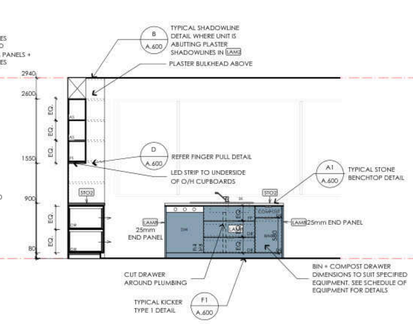

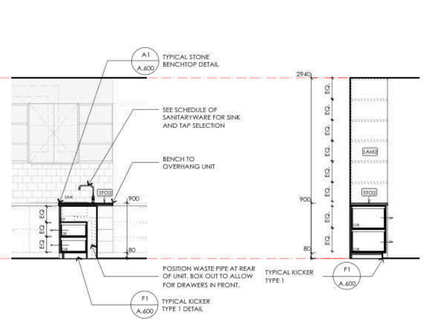

FOR CONSTRUCTION - 17/12/19

ISSUE	DATE	REVISION
D	17/12/19	FOR CONSTRUCTION
C	31/5/19	CONTRACT SET

This drawing is to be read in conjunction with the other contract documents including the specification and all other relevant consultants drawings. Any discrepancies found during the course of the contract are to be brought immediately to the attention of the Contract Administrator. All dimensions are to be checked on site prior to commencement of any work. Do not scale any dimensions from this drawing. Drawings are to be read in conjunction with all relevant consultants documentation.

CLIENT H.CHARALAMBOUS

Gardiner Architects
7/252 St Georges Rd, Fitzroy North, VIC, 3068
Ph: (03) 9486 4592 E: info@paulgardiner.com.au

DWG JOINERY PLANS & ELEVATIONS - LEVEL 04

PROJECT RETAIL/RESIDENTIAL DEVELOPMENT
752 HIGH STREET, THORNBURY

DRAWN BY AM
SCALE 1:100

JOB NO 141211
A.607
DWG #
REV# D

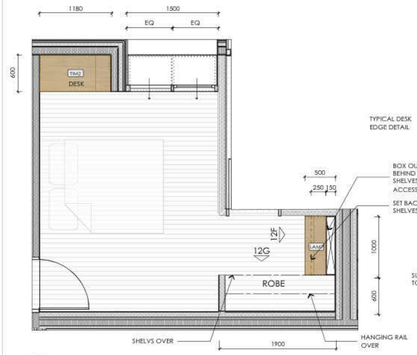

12. 2 APARTMENT 12 - BED 1
1:50

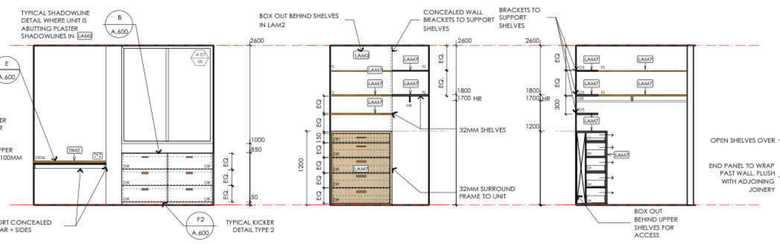

12E APARTMENT 12 - BED 1
1:50

12F APARTMENT 12 - BED 1
1:50

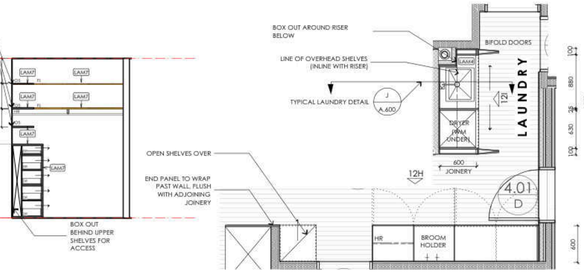

12. 3 APARTMENT 12 - LAUNDRY/STORAGE
1:50

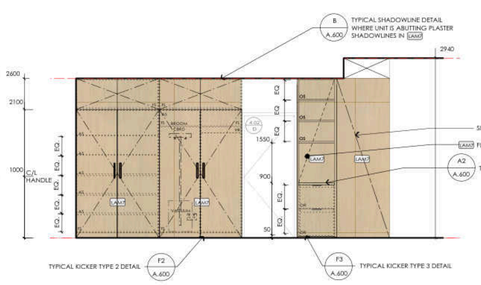

12H APARTMENT 12 - LAUNDRY/STORAGE
1:50

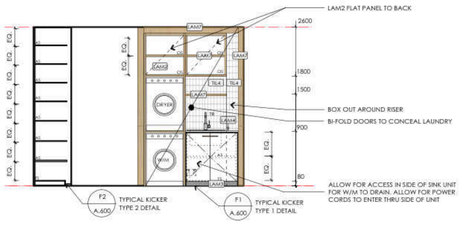

12I APARTMENT 12 - LAUNDRY/STORAGE
1:50

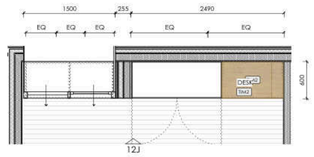

12. 4 APARTMENT 12 - BED 2
1:50

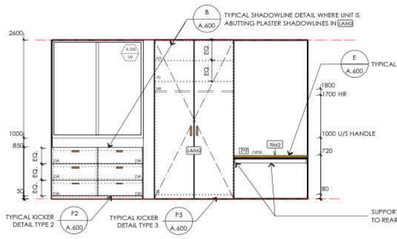

12J APARTMENT 12 - BED 2
1:50

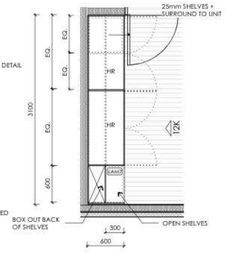

12. 5 APARTMENT 12 - BED 3
1:50

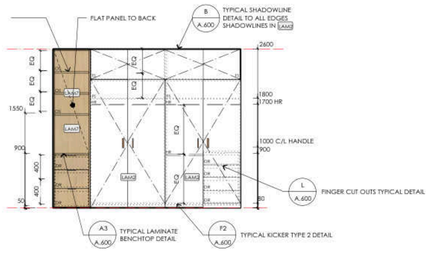

12K APARTMENT 12 - BED 3
1:50

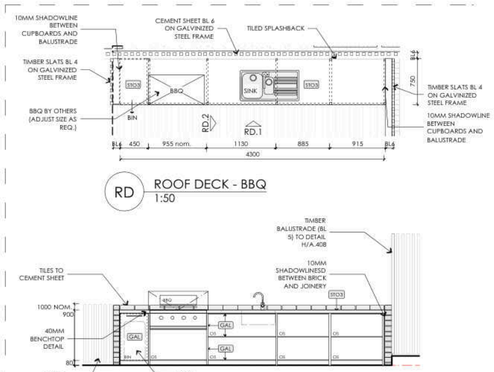

RD ROOF DECK - BBQ
1:50

RD1 ROOF DECK - BBQ ELEVATION
1:50

RD2 ROOF DECK - BBQ TYPICAL SECTION
1:50

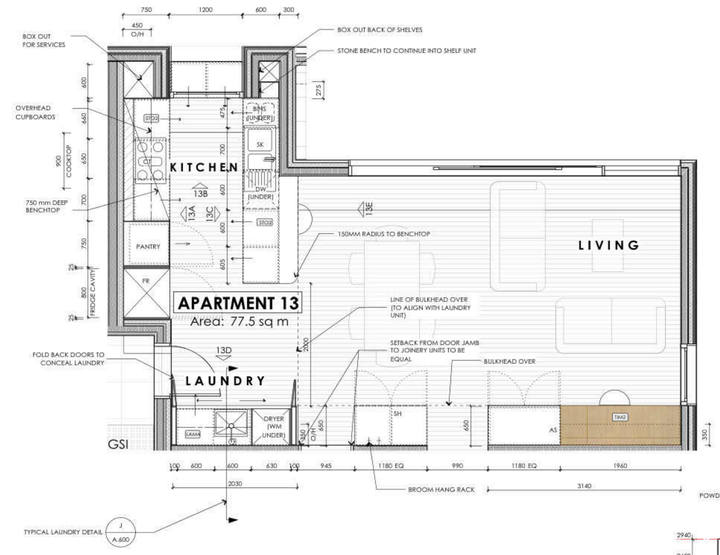

13.1 APARTMENT 13 - KITCHEN/LIVING/DINING/LAUNDRY
1:50

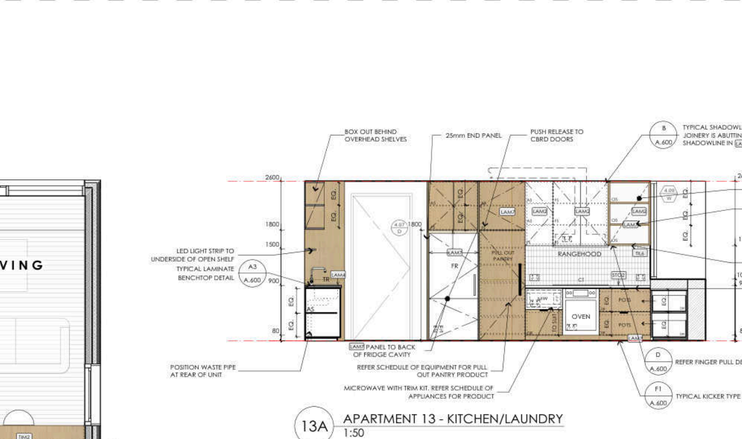

13A APARTMENT 13 - KITCHEN/LAUNDRY
1:50

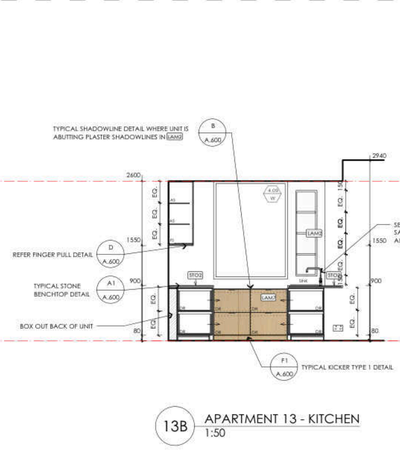

13B APARTMENT 13 - KITCHEN
1:50

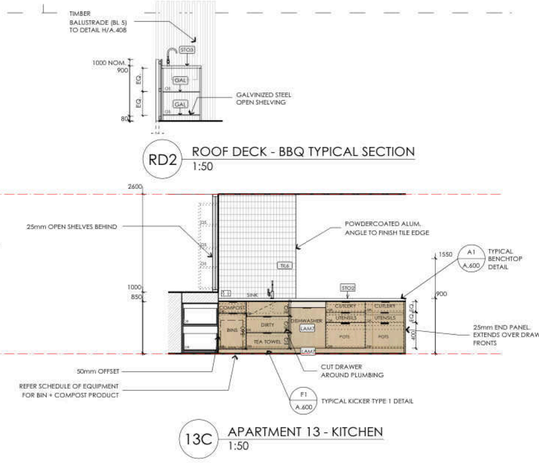

13C APARTMENT 13 - KITCHEN
1:50

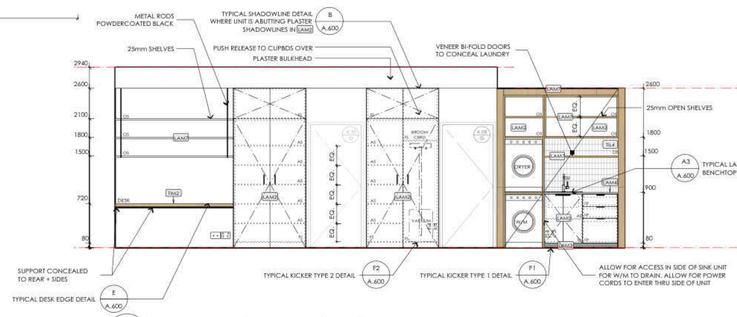

13D APARTMENT 13 - LAUNDRY/LIVING
1:50

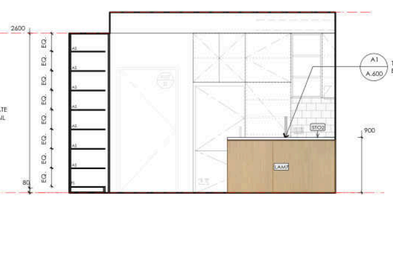

13E APARTMENT 13 - KITCHEN/LAUNDRY
1:50

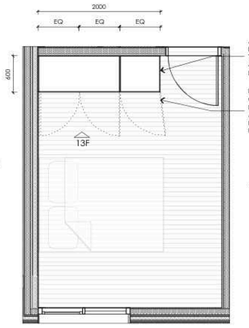

13. 2 APARTMENT 13 - BED 1/2 (TYPICAL)
1:50

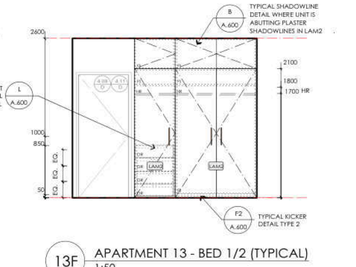

13F APARTMENT 13 - BED 1/2 (TYPICAL)
1:50

FOR CONSTRUCTION - 17/12/19

ISSUE	DATE	REVISION
D	17/12/19	FOR CONSTRUCTION
C	31/5/19	CONTRACT SET

This drawing is read in conjuction with the project specification and any instructions issued during the course of the contract. Do not scale any dimensions from drawing. Notify discrepancies in documents before commencing any work. Do not scale any dimensions from drawing. Notify discrepancies in documents.

CLIENT H.CHARALAMBOUS

Gardiner Architects
7/252 St George's Rd, Fitzroy North, VIC 3068
Ph: (03) 9486 4092, E: info@paulgardiner.com.au

DWG **JOINERY PLANS & ELEVATIONS - LEVEL 05**
PROJECT RETAIL/RESIDENTIAL DEVELOPMENT
752 HIGH STREET, THORNBURY
DRAWN BY AM
SCALE 1:50 @ A1
JOB NO. 141211
A.608
DWG #
REV# D

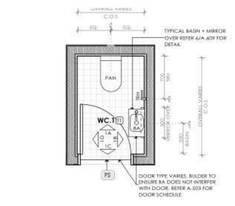

1 WC.1 (APT. 1/4)
1:50

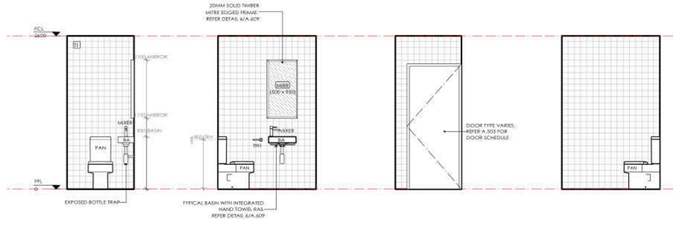

1A ELEVATION
1:50

1B ELEVATION
1:50

1C ELEVATION
1:50

1D ELEVATION
1:50

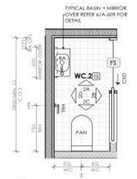

2 WC.2 (APT.13)
1:50

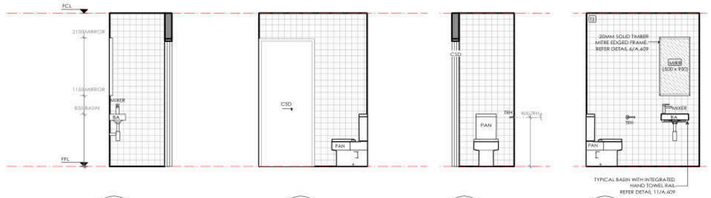

5A ELEVATION
1:50

5B ELEVATION
1:50

5C ELEVATION
1:50

5D ELEVATION
1:50

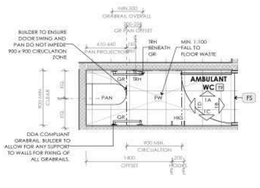

3 GROUND FLOOR AMBULANT TYPICAL
1:50

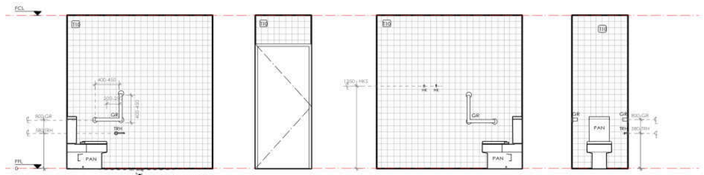

A ELEVATION
1:50

B ELEVATION
1:50

C ELEVATION
1:50

D ELEVATION
1:50

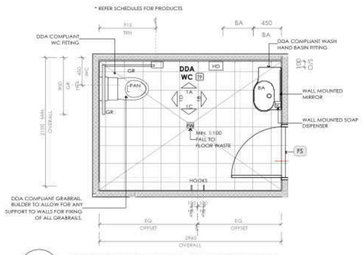

4 GROUND FLOOR ACCESSIBLE WC
1:50

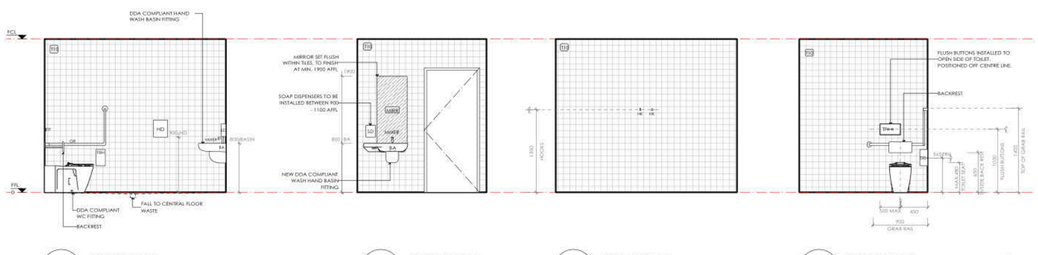

A ELEVATION
1:50

B ELEVATION
1:50

C ELEVATION
1:50

D ELEVATION
1:50

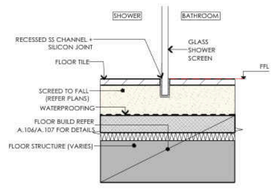

TYPICAL SECTION FLOOR JUNCTION

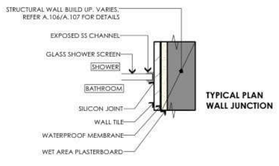

TYPICAL PLAN WALL JUNCTION

7 SHOWER SCREEN TYPICAL DETAIL
1:5

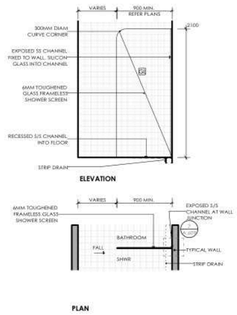

8 TYPICAL SHOWER SCREEN TYPE 1
1:50

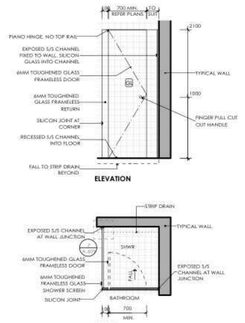

9 TYPICAL SHOWER SCREEN TYPE 2
1:50

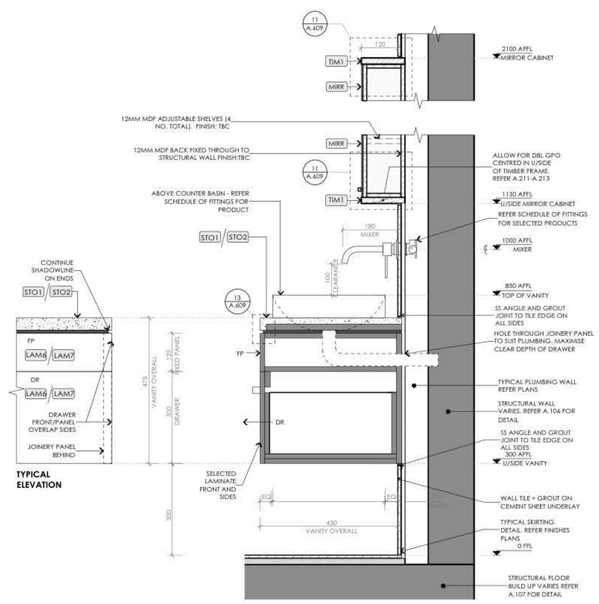

5 TYPICAL VANITY DETAIL
1:10

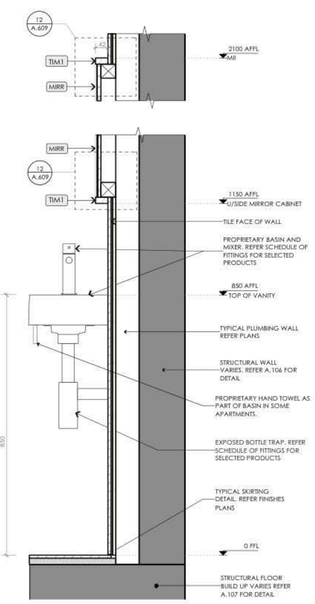

6 TYPICAL BASIN WITH MIRROR DETAIL
1:10

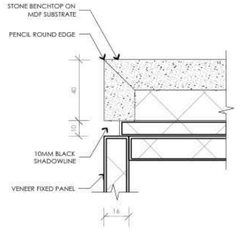

13 BATHROOM VANITY DETAIL TYPICAL
1:2

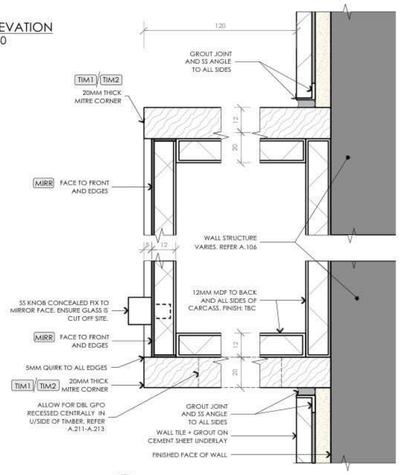

11 MIRROR C'PUD TYPICAL DETAIL
1:2

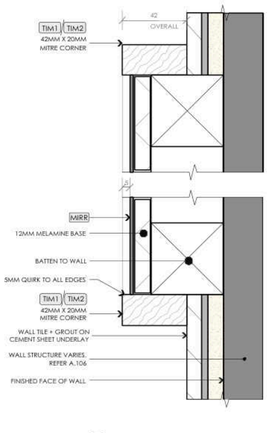

12 MIRROR DETAIL TYPICAL
1:2

JOINERY NOTES

GENERAL

1. READ IN CONJUNCTION WITH CONTRACT SPECIFICATION
2. CONFIRM ALL MEASUREMENTS PRIOR TO MANUFACTURE
3. SPECIFIC SPECIFICATION
   - ALL VERTICAL LAMINATE SURFACES ARE ASSUMED PRE-FINISHED U.O.N.
   - ALL BENCHTOP LAMINATE SURFACES ARE TO HAVE 1.2mm LAMINATE APPLIED TO MR SUBSTRATE
   - SQUARE EDGING TO LAMINATE BOARD TO BE MATCHING COLOUR 2mm ABS EDGES
   - DOOR HINGES TO BE BLUM OR SIMILAR 170° U.O.N.
   - LEADING EDGES OF CARCASS TO MATCH DOOR FACE COLOUR.
   - INTERNAL NON-EXPOSED SURFACES TO BE WHITE MELAMINE 16mm THICK TO APARTMENTS 1, 4, 5, 8, 9, 12 AND BLACK MELAMINE TO APARTMENTS 2, 3, 6, 7, 10, 11, 13.
   - PANTRY INTERNALS TO BE LAMINATE AS SHOWN (NOT MELAMINE)
   - COLOUR TO MATCH EXPOSED LAMINATE.
   - BACKS TO BE 16mm MELAMINE
   - VENEER PANELS - BUILDER TO ALLOW FOR VENEER TO BE APPLIED TO NOM. 16mm BOARD AND FINISHED WITH MATTE POLYURETHANE SURFACE TREATMENT OR PREFINISHED
   - REFER TO SEPARATE 'SCHEDULE OF JOINERY FINISHES' DOCUMENT FOR SELECTION SPECIFICASON

APPLIANCES

1. CHECK SIZES OF ALL APPLIANCES & EQUIPMENT & ALLOW APPROPRIATE CLEARANCES PRIOR TO MANUFACTURE
2. BUILDER TO INSTALL ALL APPLIANCES IN ACCORDANCE WITH MANUFACTURERS INSTRUCTIONS

STONEWORK

BUILDER TO ALLOW TO PROVIDE TEMPLATE FOR STONE CONTRACTORS WHERE APPLICABLE

CABINET + DRAWER HARDWARE

1. CABINET HARDWARE SUPPLY SUBJECT TO PROVISIONAL SUMS, INSTALLED BY BUILDER
2. BUILDER TO ALOW FOR INSTALLATION OF ALL JOINERY.
3. ALL DRAWER RUNNERS TO BE 'BLUM TANDEM' RUNNER SYSTEM WITH 'BLUMOTION' SOFT-CLOSING MECHANISM

JOINERY LEGEND

CR	PULL UP CLOTHES RACK	LB	LAUNDRY BASKET
AS	ADJUSTABLE SHELF	FS	FIXED SHELF
OS	OPEN SHELF	CSD	CAVITY SLIDING DOOR
FP	FIXED PANEL	DW	DISH WASHER
FR	FRIDGE	DR	DRAWER
CPD	CUPBOARD	WM	WASHING MACHINE
TD	TUMBLE DRYER	BA	HAND BASIN
TRH	TOILET ROLL HOLDER	TR	TOWEL RAIL
TRG	TROUGH	CT	COOK TOP
MC	MIRROR CABINET	WB	WASH BASIN
V	VANITY	SD	SLIDING DOOR
HR	HANGING RAIL	MIRR	MIRROR
BH1	BULKHEAD	HTR	HEATED TOWEL RAIL
HT	HAND TOWEL HOLDER	HK	HOOK
HD	HAND DRYER		

JOINERY LEGEND

STO1	SELECTED STONE BENCHTOP	[REFER SCHEDULE OF JOINERY FINISHED FOR PRODUCT]
STO2	SELECTED STONE BENCHTOP	[REFER SCHEDULE OF JOINERY FINISHED FOR PRODUCT]
LAM6	SELECTED VENEER	[REFER SCHEDULE OF JOINERY FINISHED FOR PRODUCT]
LAM7	SELECTED VENEER	[REFER SCHEDULE OF JOINERY FINISHED FOR PRODUCT]
TIM1	SELECTED SOLID TIMBER	[REFER SCHEDULE OF JOINERY FINISHED FOR PRODUCT]
TIM2	SELECTED SOLID TIMBER	[REFER SCHEDULE OF JOINERY FINISHED FOR PRODUCT]
MIRR	SELECTED MIRROR	[REFER SCHEDULE OF JOINERY FINISHED FOR PRODUCT]
FS	SELECTED FLOOR STRIP	[REFER A.205 FOR TYPICAL THRESHOLD DETAILS]
GL	GLASS SHOWER SCREEN	[REFER A.609 FOR TYPICAL DETAILS]
T1 → T9	SELECTED WET AREA TILE	[REFER SCHEDULE OF TILES FOR PRODUCT]

This drawing to be read in conjunction with the other contract documents forming the contract. Contractor to verify all dimensions on site before commencing any work or shop drawings. Do not scale any dimensions from drawings. Advise Architect of all discrepancies or omissions.

ISSUE	DATE	REVISION
D	17/12/19	FOR CONSTRUCTION
C	31/5/19	CONTRACT SET

FOR CONSTRUCTION - 17/12/19

CLIENT CHALLEN

Gardiner Architects
77252 1 Georgas Rd, Fitzroy North, VIC, 3068
Ph: (03) 9486 4092 E: info@paulgardiner.com.au

DWG JOINERY PLANS & ELEVATIONS-TYPICAL WET AREAS
PROJECT RETAIL/RESIDENTIAL DEVELOPMENT 752 HIGH STREET, THORNBURY
DRAWN BY AM
SCALE 1:100
JOB NO 141211
DWG # A.609
REV# D

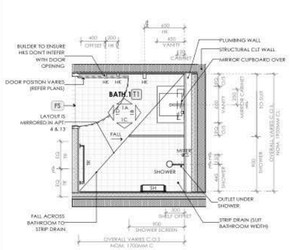

1 BATH.1 (APT. 1/4/13)
1:50

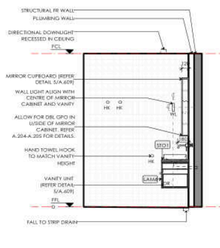

1A ELEVATION
1:50

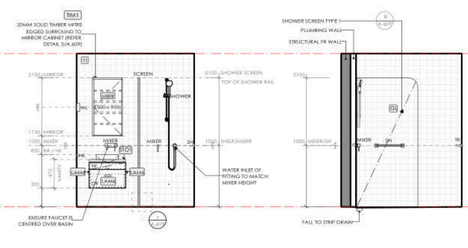

1B ELEVATION
1:50

1C ELEVATION
1:50

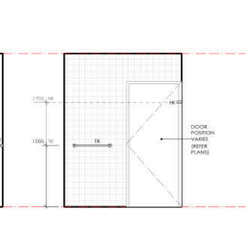

1D ELEVATION
1:50

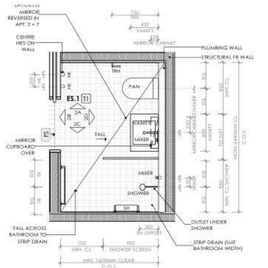

2 ES.1 (APT. 2/3/6/7)
1:50

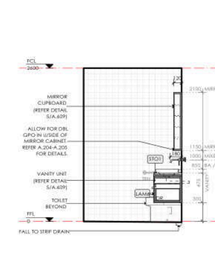

2A ELEVATION
1:50

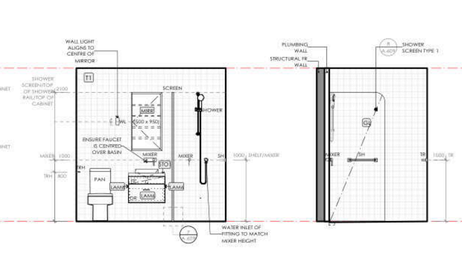

2B ELEVATION
1:50

2C ELEVATION
1:50

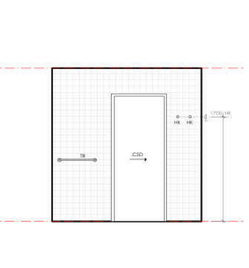

2D ELEVATION
1:50

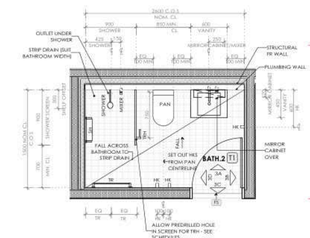

3 BATH.2 (APT. 2/3)
1:50

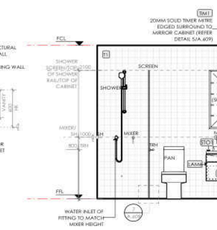

3A ELEVATION
1:50

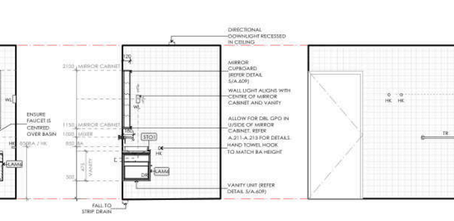

3B ELEVATION
1:50

3C ELEVATION
1:50

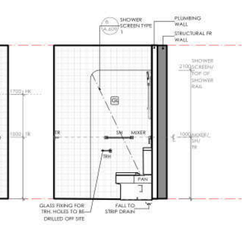

3D ELEVATION
1:50

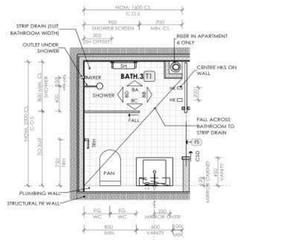

4 BATH.3 (APT. 6/7)
1:50

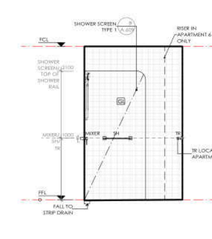

4A ELEVATION
1:50

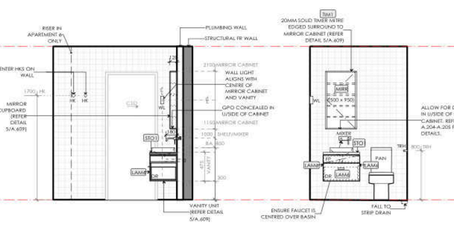

4B ELEVATION
1:50

4C ELEVATION
1:50

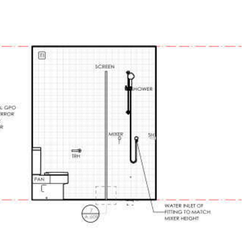

4D ELEVATION
1:50

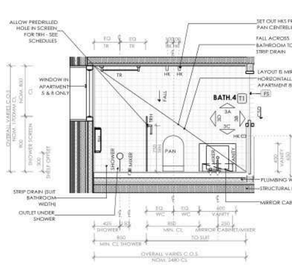

5 BATH.4 (APT. 5/8/9)
1:50

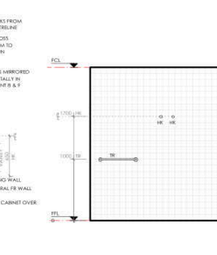

5A ELEVATION
1:50

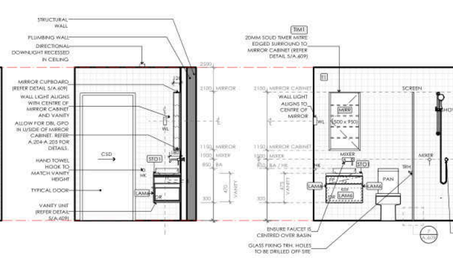

5B ELEVATION
1:50

5C ELEVATION
1:50

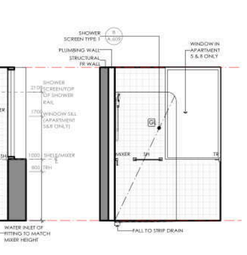

5D ELEVATION
1:50

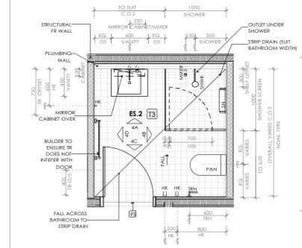

6 ES.2 (APT. 10)
1:50

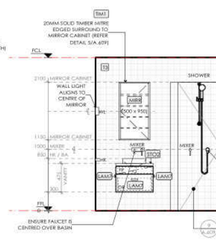

6A ELEVATION
1:50

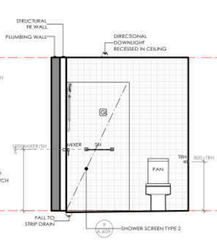

6B ELEVATION
1:50

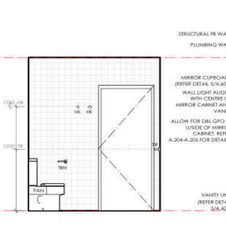

6C ELEVATION
1:50

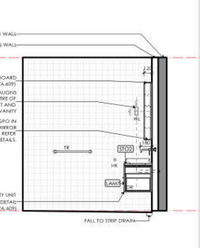

6D ELEVATION
1:50

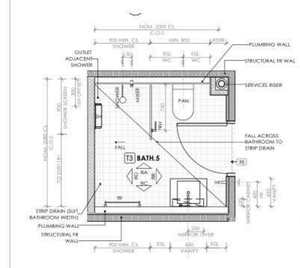

7 BATH.5 (APT. 10)
1:50

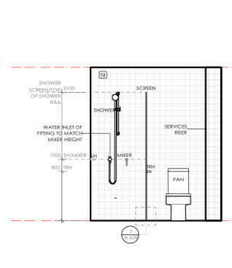

7A ELEVATION
1:50

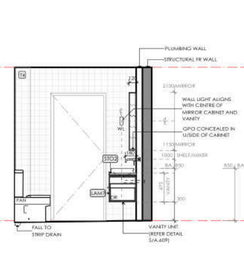

7B ELEVATION
1:50

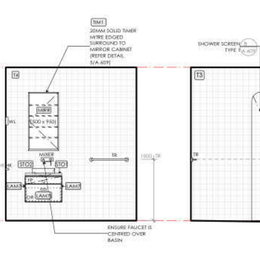

7C ELEVATION
1:50

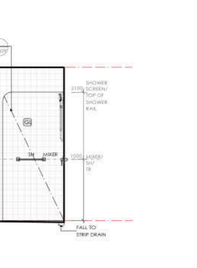

7D ELEVATION
1:50

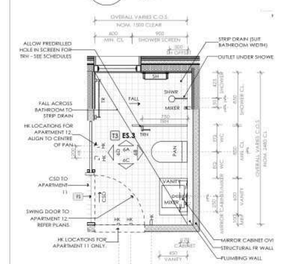

8 ES.3 (APT. 11/12)
1:50

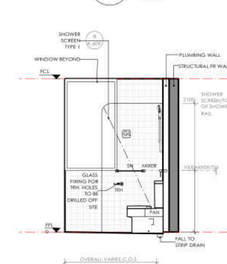

8A ELEVATION
1:50

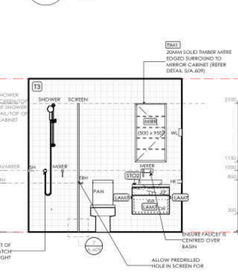

8B ELEVATION
1:50

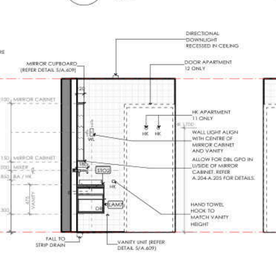

8C ELEVATION
1:50

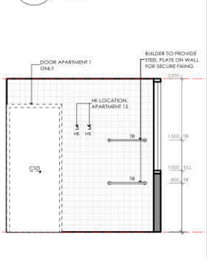

8D ELEVATION
1:50

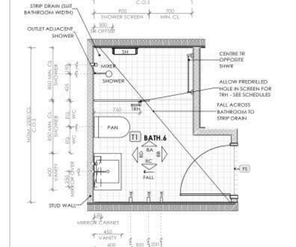

9 BATH.6 (APT. 11)
1:50

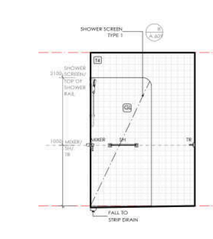

9A ELEVATION
1:50

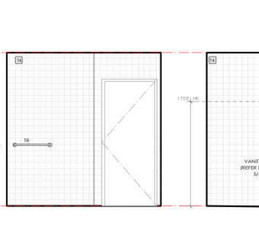

9B ELEVATION
1:50

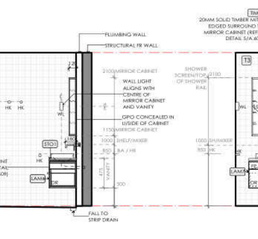

9C ELEVATION
1:50

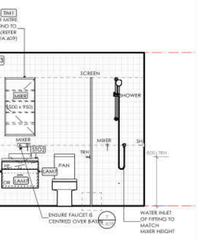

9D ELEVATION
1:50

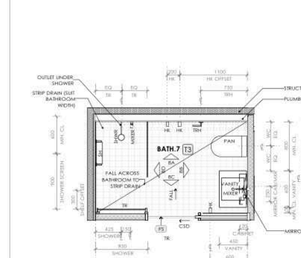

10 BATH.7 (APT. 12)
1:50

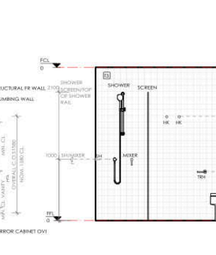

10A ELEVATION
1:50

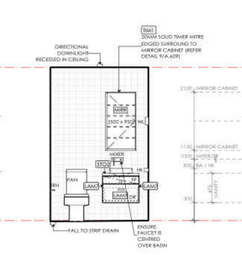

10B ELEVATION
1:50

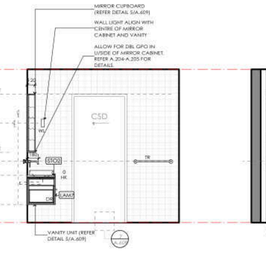

10C ELEVATION
1:50

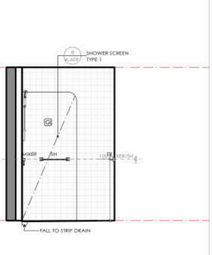

10D ELEVATION
1:50

FOR CONSTRUCTION - 17/12/19

ISSUE	DATE	REVISION
D	17/12/19	FOR CONSTRUCTION
C	31/5/19	CONTRACT SET

This drawing to require conjunction with the architect's drawings and with the project specification and any instructions issued during the course of the contract. Contractor must verify all dimensions on site before commencing any work. Do not scale from this drawing. Please advise Architect of full discrepancies in documents.

Gardiner Architects
7/252 St Georges Rd, Fitzroy North, VIC, 3068
Ph: (03) 9486 4092 E: info@paulgardiner.com.au

CLIENT CHALLEN

PROJECT RETAIL/RESIDENTIAL DEVELOPMENT
752 HIGH STREET, THORNBURY

DWG JOINERY PLANS & ELEVATIONS-TYPICAL WET AREAS

DRAWN BY AM
SCALE 1:100

JOB NO 141211
A.610
DWG #
REV# D

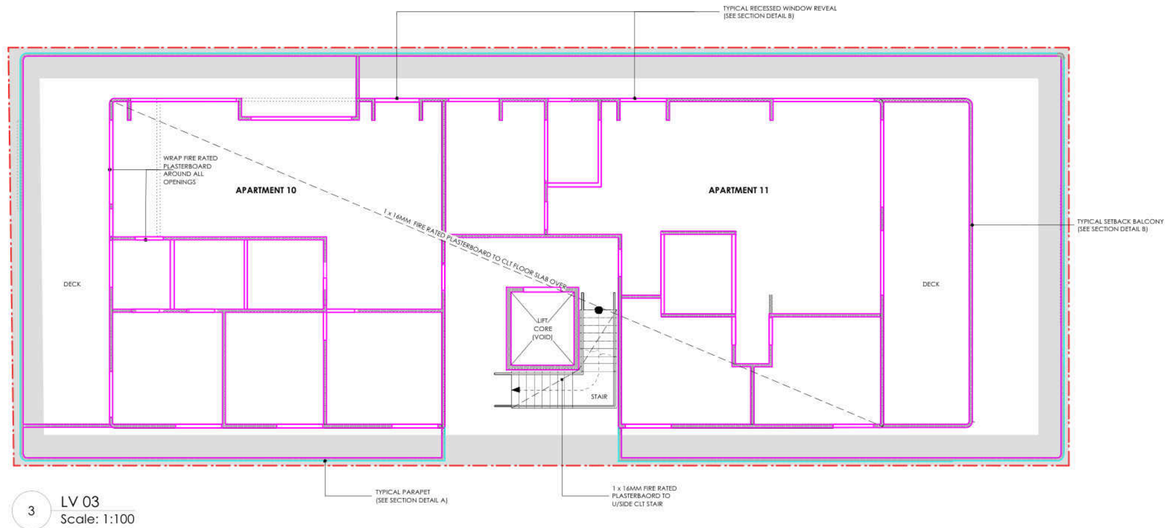

3 LV 03
Scale: 1:100

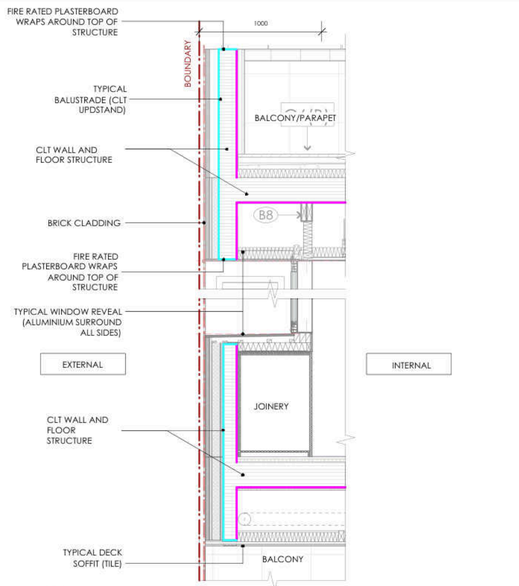

A LV 01/02/03 (TYPICAL BALCONY/PARAPET/WINDOW REVEAL)
NOT TO SCALE

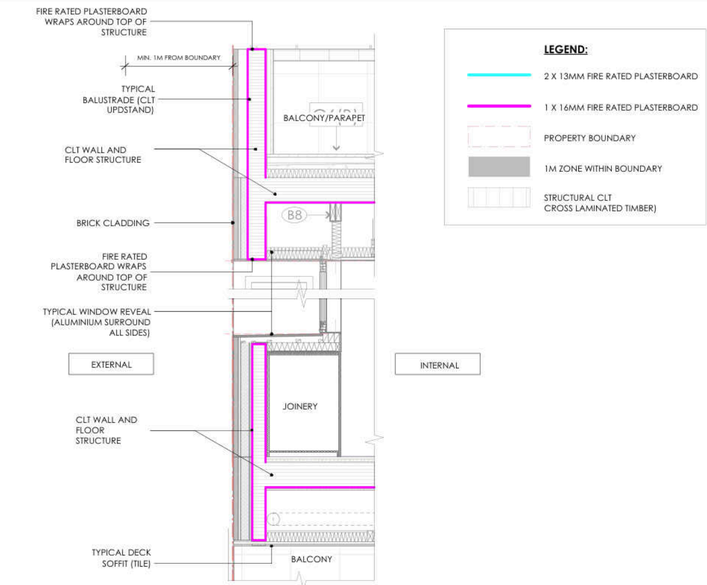

B LV 03/04/05 (TYPICAL BALCONY/PARAPET/WINDOW REVEAL)
NOT TO SCALE

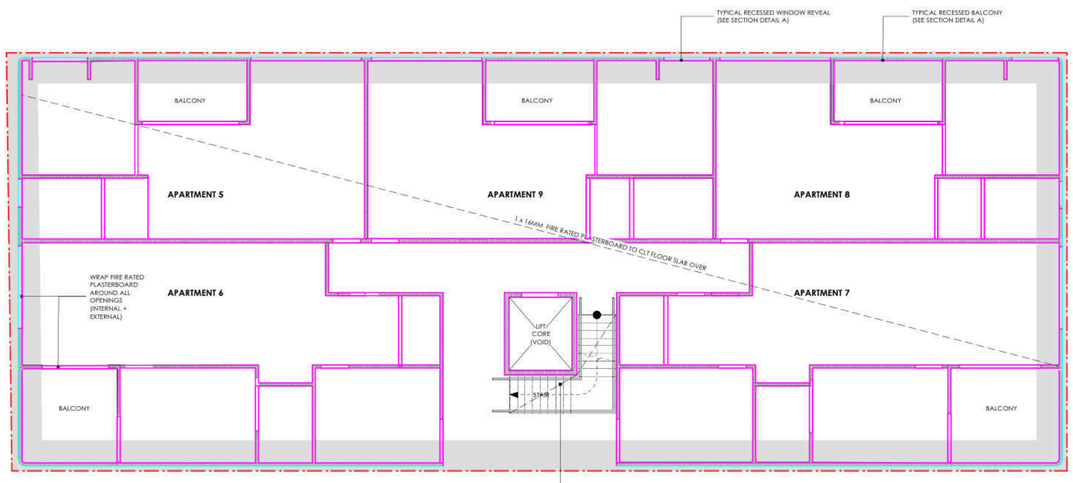

2 LV 02
Scale: 1:100

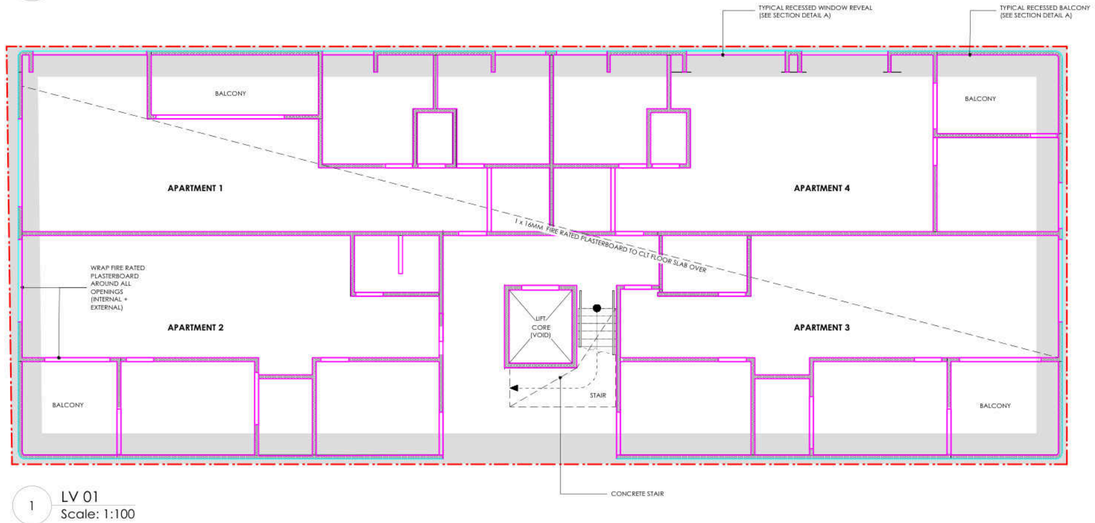

1 LV 01
Scale: 1:100

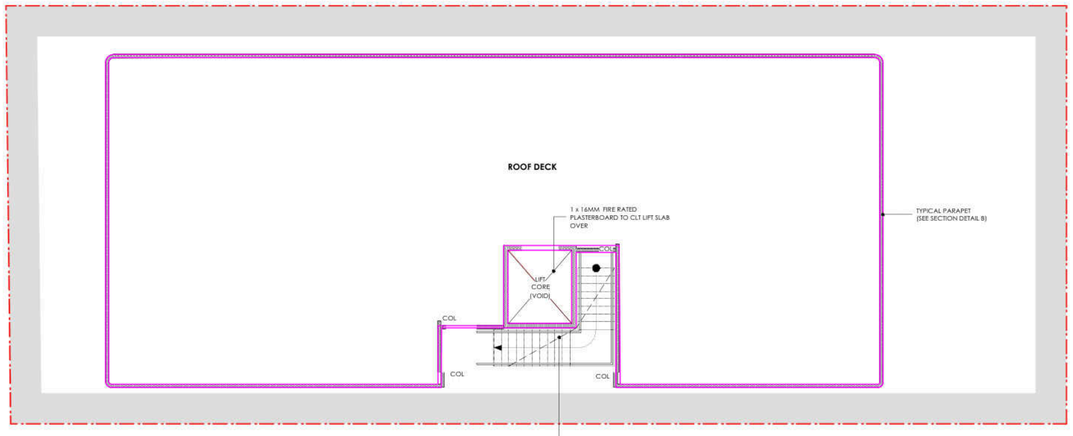

5 LV 05
Scale: 1:100

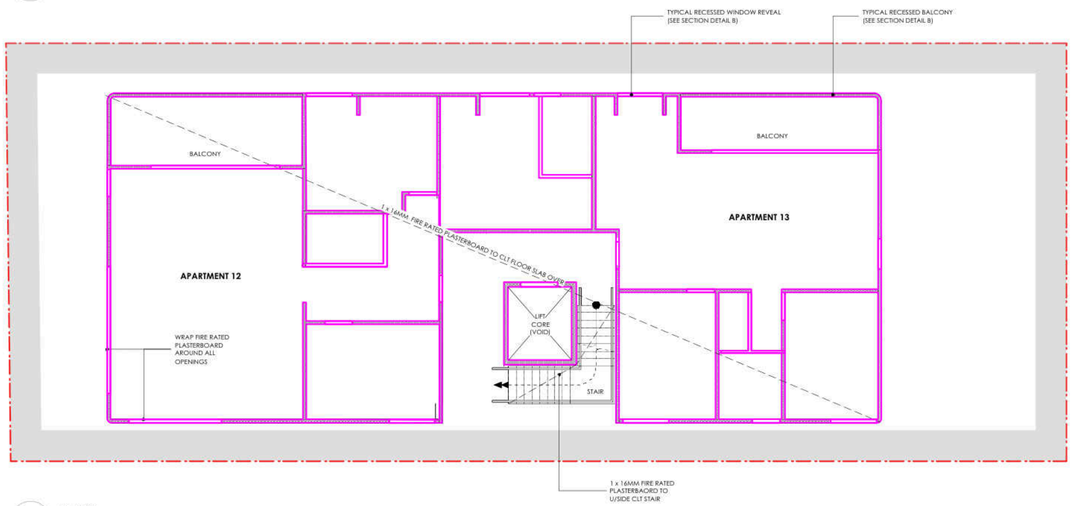

4 LV 04
Scale: 1:100

FOR CONSTRUCTION - 17/12/19

This drawing to be read in conjunction with the other contract documents including the Specification. Any discrepancies found before constructing the course of the contract, Contractor must notify all dimensions on site before commencing any work. Do not scale any dimensions from drawings. Refer to Architect for all discrepancies or enquiries.

ISSUE	DATE	REVISION
A	17/12/19	FOR CONSTRUCTION

CLIENT H.CHARALAMBOUS

Gardiner Architects
7/252 St Georges Rd, Fitzroy North, VIC, 3068
Ph: (03) 9486 4092 E: info@paulgardiner.com.au

DWG FIRE RATED PLASTERBOARD (ALL LEVELS)
PROJECT RETAIL/RESIDENTIAL DEVELOPMENT
752 HIGH STREET, THORNBURY
DRAWN BY AM
SCALE 1:100 @ A1
JOB NO 141211
A.701
DWG # A
REV #